

BILL OF MATERIAL


MARK	QTY	DESCRIPTION	LENGTH	WEIGHT	REMARKS
604B1	1	BEAM			SQ-2
604B1	1	HSS4X4X1/4	6'-0 1/4"	69	GALVANIZED A500-GR.B
p261	2	PL3/8"X4"	0'-4"	3	A572-GR.50
604B2	2	BEAMS			SQ-2
604B2	2	HSS4X4X1/4	9'-6 1/4"	218	GALVANIZED A500-GR.B
p261	4	PL3/8"X4"	0'-4"	7	A572-GR.50
604B3	1	BEAM			SQ-2
604B3	1	HSS4X4X1/4	55'-4 7/8"	635	GALVANIZED A500-GR.B
p287	14	L4X3X3/8	0'-4"	40	A572-GR.50
p258	2	PL3/8"X4"	0'-4"	3	A572-GR.50
		TOTAL WEIGHT THIS DRAWING		976	

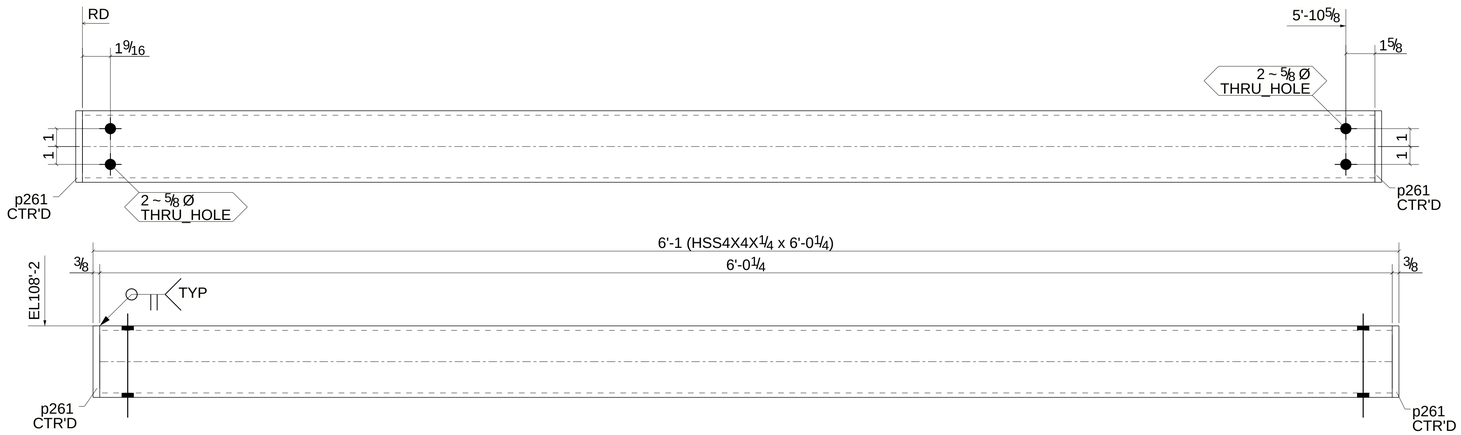

ONE - BEAM - 604B1

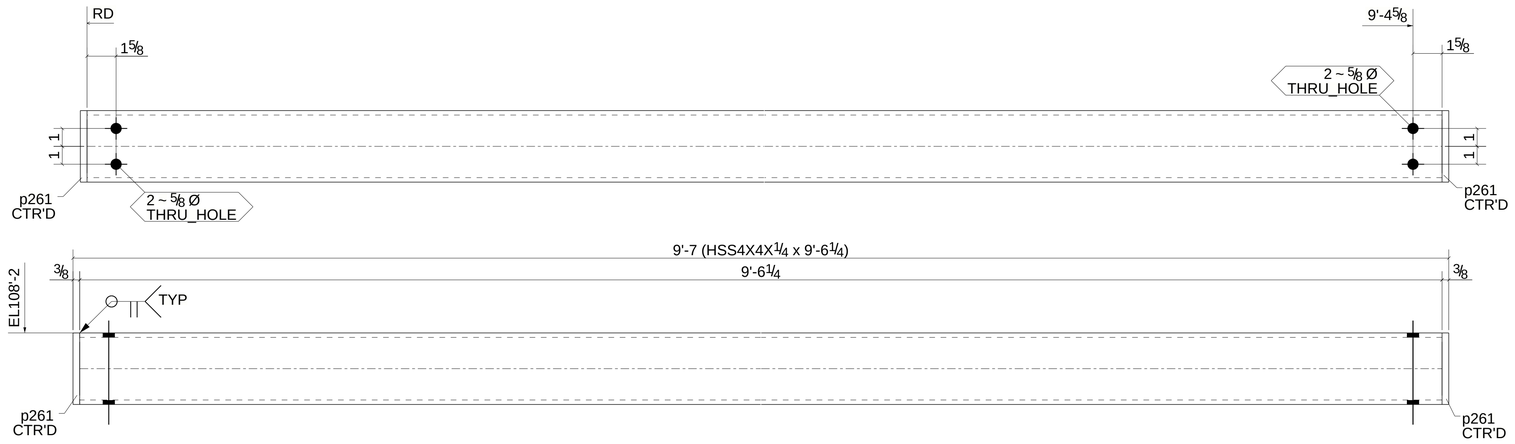

2 - BEAMS - 604B2

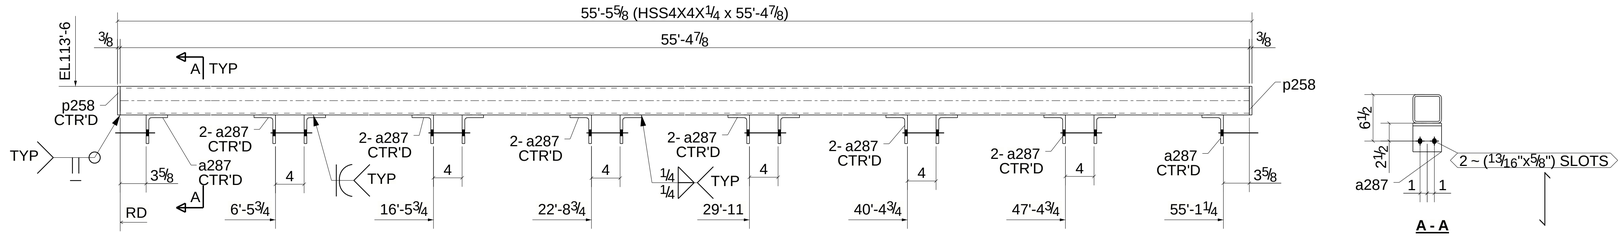

ONE - BEAM - 604B3

REV	DESCRIPTION	ECO	DWN	APPR	APPR	DATE
0	ISSUED FOR FABRICATION					06/09/2026

PROPRIETARY AND CONFIDENTIAL: THIS DRAWING AND ALL INFORMATION AND KNOWLEDGE CONTAINED OR REFERRED HEREIN ARE THE CONFIDENTIAL AND PROPRIETARY PROPERTY OF PRIMA AND AS SUCH ARE INSTRUMENTS OF SERVICE FOR USE SOLELY WITH RESPECT TO THIS PROJECT. THESE INSTRUMENTS OF SERVICE SHALL NOT BE REPRODUCED, TRANSMITTED, DISCLOSED OR USED OTHERWISE IN WHOLE OR IN PART, WITHOUT PRIOR WRITTEN AGREEMENT BY PRIMA AND MUST BE IMMEDIATELY RETURNED OR DESTROYED UPON REQUEST.

Prima Structures

TOLERANCES UNLESS NOTED

DECIMALS	ANGLES
.X	+/- 0.5°
.XX +/- 0.13	FRAC
.XXX +/- 0.062	+/- 1/8"

Miguel Hidalgo, Mexico City

CUSTOMER INFORMATION

1523 HARRISON ST.

1523 HARRISON ST., OAKLAND, CA 94612

DRAWING NUMBER	REVISION
604	0
REF.:	DOC. OWNER:
PROJECT NO. 5220	PART/MATERIAL NO. BEAM
SCALE 1:12	SIZE D
SHEET 1 OF 1	