


| BILL OF MATERIAL |     |                           |            |        |                      |
|------------------|-----|---------------------------|------------|--------|----------------------|
| MARK             | QTY | DESCRIPTION               | LENGTH     | WEIGHT | REMARKS              |
|                  |     |                           |            |        |                      |
| 608B1            | 1   | BEAM                      |            |        | SQ-2                 |
| 608B1            | 1   | HSS4X4X1/4                | 4'-11 3/4" | 57     | GALVANIZED A500-GR.B |
| p261             | 2   | PL3/8"X4"                 | 0'-4"      | 3      | A572-GR.50           |
|                  |     |                           |            |        |                      |
| 608B2            | 1   | BEAM                      |            |        | SQ-2                 |
| 608B2            | 1   | HSS4X4X1/4                | 12'-7 1/8" | 144    | GALVANIZED A500-GR.B |
| a287             | 4   | L4X3X3/8                  | 0'-4"      | 11     | A572-GR.50           |
| p55              | 1   | PL3/8"X4"                 | 0'-4"      | 2      | A572-GR.50           |
|                  |     |                           |            |        |                      |
| 608B3            | 1   | BEAM                      |            |        | SQ-2                 |
| 608B3            | 1   | HSS4X4X1/4                | 6'-8 1/4"  | 77     | GALVANIZED A500-GR.B |
| p261             | 2   | PL3/8"X4"                 | 0'-4"      | 3      | A572-GR.50           |
|                  |     |                           |            |        |                      |
|                  |     | TOTAL WEIGHT THIS DRAWING |            | 298    |                      |

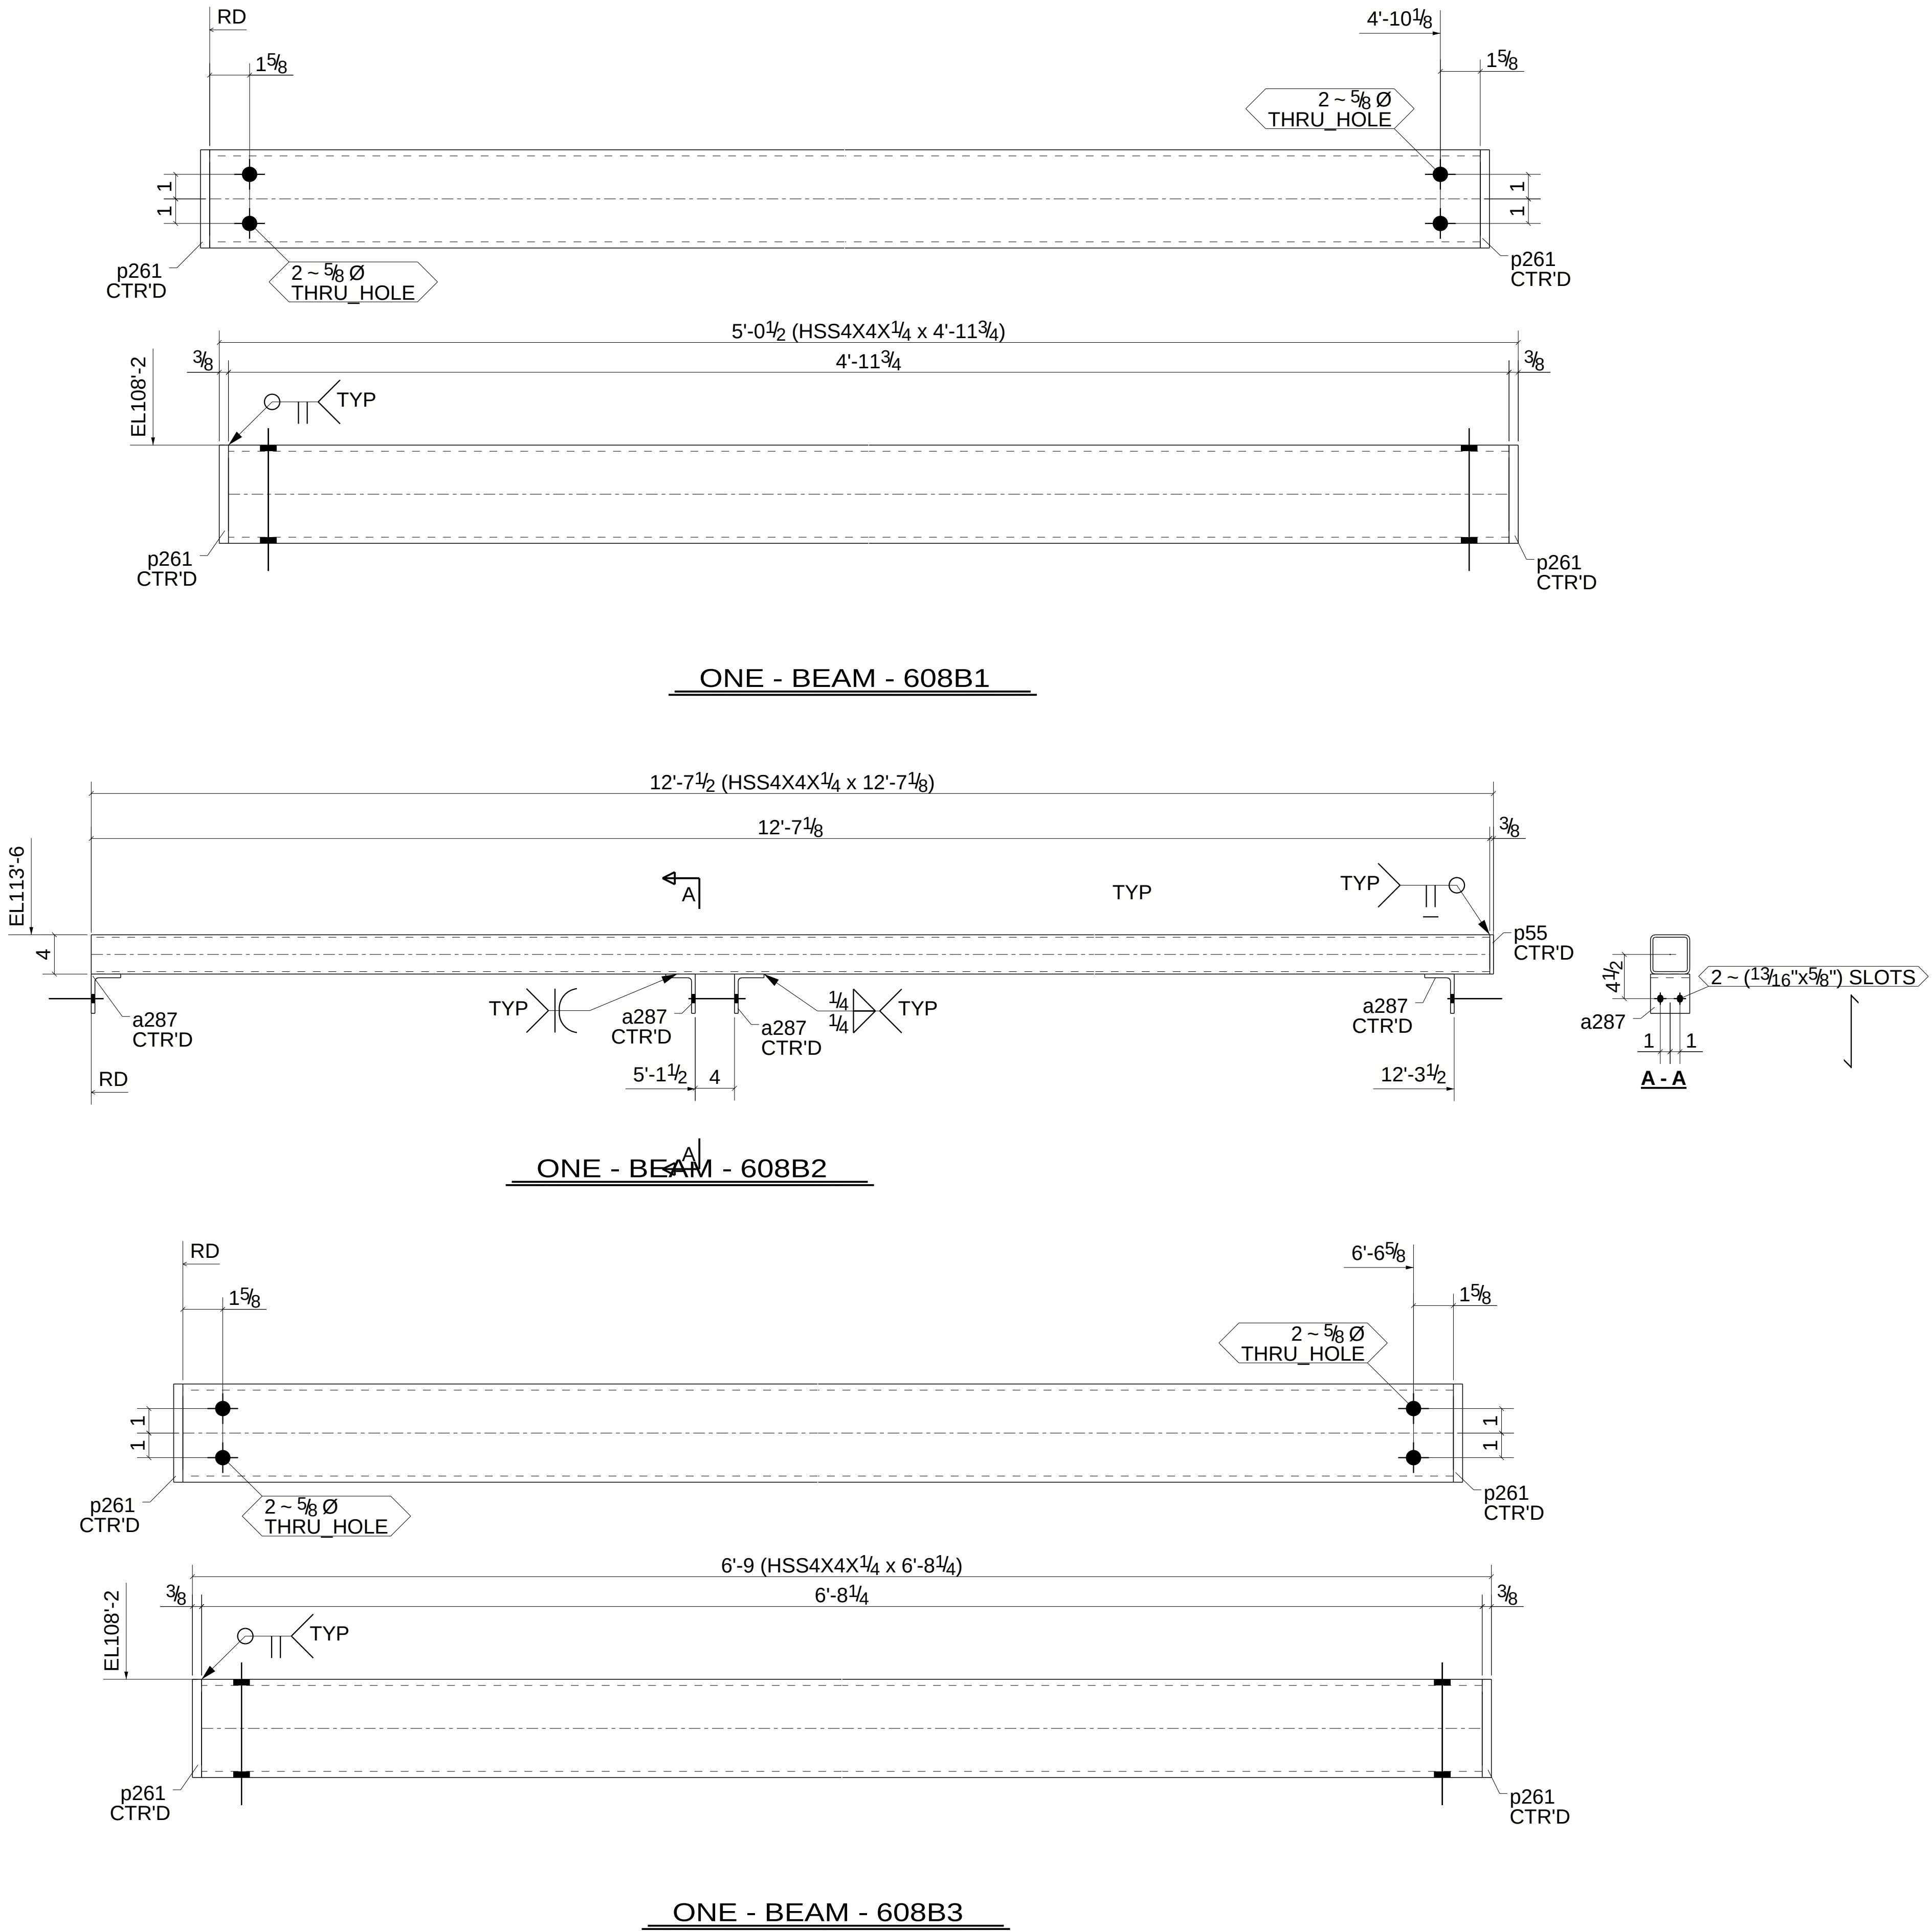

|  |  |  |  |  |  |  |  |  |  |                     |           |                           |      |
|--|--|--|--|--|--|--|--|--|--|---------------------|-----------|---------------------------|------|
|  |  |  |  |  |  |  |  |  |  | DRAWING NUMBER      |           | REVISION                  |      |
|  |  |  |  |  |  |  |  |  |  | 608                 |           | 0                         |      |
|  |  |  |  |  |  |  |  |  |  | REF.:               |           | DOC. OWNER:               |      |
|  |  |  |  |  |  |  |  |  |  | PROJECT NO.<br>5220 |           | PART/MATERIAL NO.<br>BEAM |      |
|  |  |  |  |  |  |  |  |  |  | SCALE<br>1:12       | SIZE<br>D | SHEET<br>1                | OF 1 |

TOLERANCES UNLESS NOTED

DECIMALS  
.X  
.XX +/- 0.13  
.XXX +/- 0.062

ANGLES  
+/- 0.5°  
FRAC  
+/- 1/8"

CUSTOMER INFORMATION

1523 HARRISON ST.  
1523 HARRISON ST., OAKLAND, CA 94612

06/09/2026

ECO DWN APPR APPR

0

ISSUED FOR FABRICATION

PROPRIETARY AND CONFIDENTIAL. THIS DRAWING AND ALL INFORMATION AND KNOWLEDGE CONTAINED OR REFERRED HEREIN ARE THE CONFIDENTIAL AND PROPRIETARY PROPERTY OF PRIMA AND AS SUCH ARE INSTRUMENTS OF SERVICE FOR USE SOLELY WITH RESPECT TO THIS PROJECT. THESE INSTRUMENTS OF SERVICE SHALL NOT BE REPRODUCED, TRANSMITTED, DISCLOSED OR USED OTHERWISE IN WHOLE OR IN PART, WITHOUT PRIOR WRITTEN AGREEMENT BY PRIMA AND MUST BE IMMEDIATELY RETURNED OR DESTROYED UPON REQUEST.