

# BILL OF MATERIAL

| MARK | QTY | DESCRIPTION | LENGTH | WEIGHT | REMARKS |
|---|---|---|---|---|---|
| | | | | | |
| 609B1 | 1 | BEAM | | | SQ-2 |
| 609B1 | 1 | HSS4X4X1/4 | 3'-6 1/4" | 40 | GALVANIZED A500-GR.B |
| p261 | 2 | PL3/8"X4" | 0'-4" | 3 | A572-GR.50 |
| | | | | | |
| 609B2 | 1 | BEAM | | | SQ-2 |
| 609B2 | 1 | HSS4X4X1/4 | 5'-8 1/4" | 65 | GALVANIZED A500-GR.B |
| p261 | 2 | PL3/8"X4" | 0'-4" | 3 | A572-GR.50 |
| | | | | | |
| | | TOTAL WEIGHT THIS DRAWING | | 112 | |

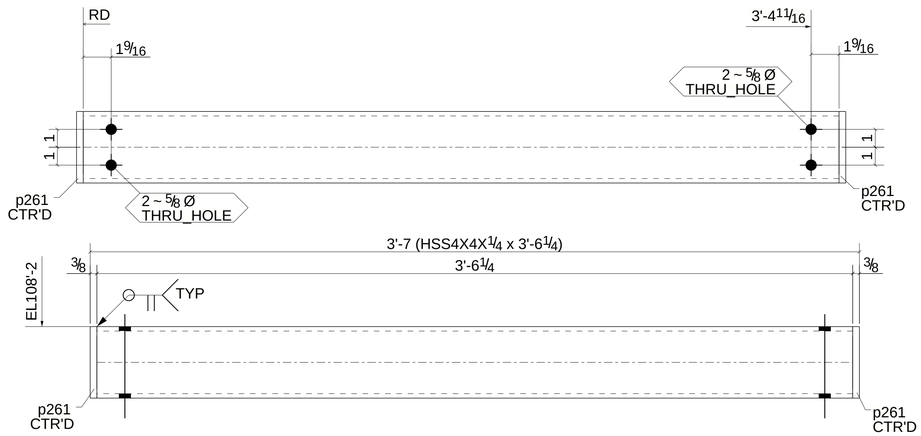


## ONE - BEAM - 609B1

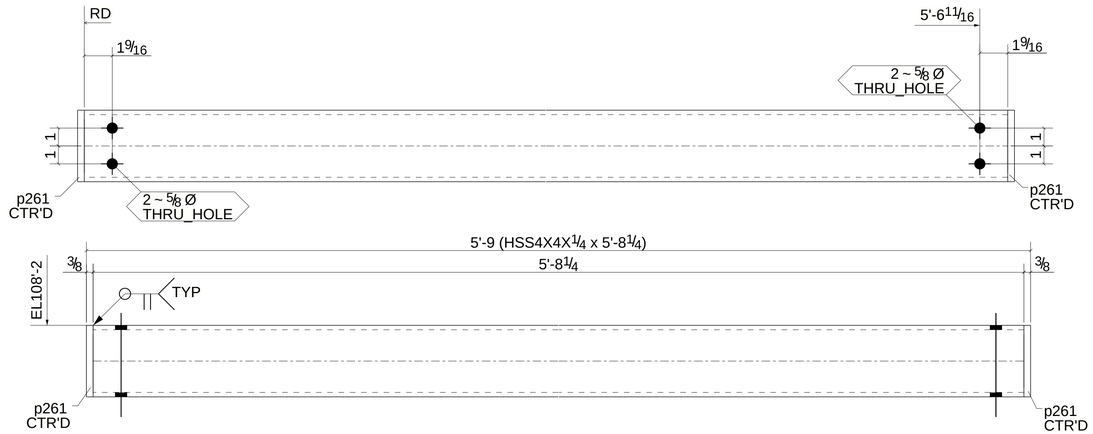


## ONE - BEAM - 609B2

| REV | DESCRIPTION | ECO | DWN | APPR | APPR | DATE |
|---|---|---|---|---|---|---|
| 0 | ISSUED FOR FABRICATION | | | | | 06/09/2026 |


PROPRIETARY AND CONFIDENTIAL: THIS DRAWING AND ALL INFORMATION AND KNOWLEDGE CONTAINED OR REFERRED HEREIN ARE THE CONFIDENTIAL AND PROPRIETARY PROPERTY OF PRIMA AND AS SUCH ARE INSTRUMENTS OF SERVICE FOR USE SOLELY WITH RESPECT TO THIS PROJECT. THESE INSTRUMENTS OF SERVICE SHALL NOT BE REPRODUCED, TRANSMITTED, DISCLOSED OR USED OTHERWISE IN WHOLE OR IN PART, WITHOUT PRIOR WRITTEN AGREEMENT BY PRIMA AND MUST BE IMMEDIATELY RETURNED OR DESTROYED UPON REQUEST.


Tekla Structures

TOLERANCES UNLESS NOTED
DECIMALS .X .XX +/- 0.13 .XXX +/- 0.062
ANGLES +/- 0.5°
FRAC +/- 1/8"

Miguel Hidalgo, Mexico City

CUSTOMER INFORMATION

1523 HARRISON ST.

1523 HARRISON ST., OAKLAND, CA 94612

DRAWING NUMBER: 609
REVISION: 0
REF.:
DOC. OWNER:
PROJECT NO.: 5220
PART/MATERIAL NO.: BEAM
SCALE: 1:12
SIZE: D
SHEET: 1 OF 1