



ONE - BEAM - 611B1

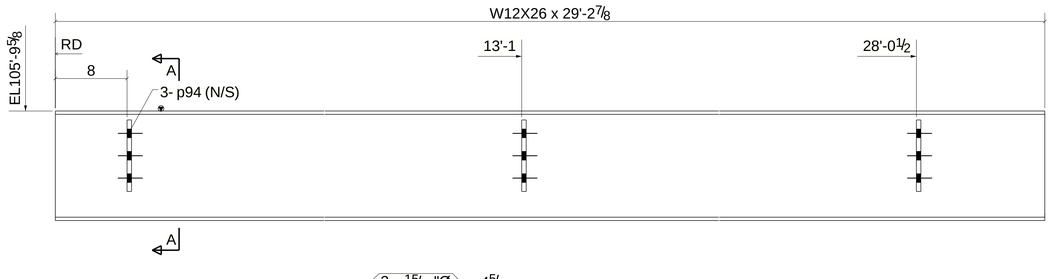


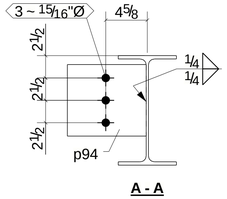


A - A

ONE - BEAM - 611B2

MARK	QTY	DESCRIPTION	LENGTH	WEIGHT	REMARKS
611B1	1	BEAM			SQ-1/BEV-1
611B1	1	HSS4X4X1/4	17'-0 1/8"	195	GALVANIZED A500-GR.B
p89	1	PL3/8"X3 5/8"	0'-3 5/8"	1	A572-GR.50
611B2	1	BEAM			SQ-2
611B2	1	W12X26	29'-2 7/8"	761	SHOP_PRIMER A992
p94	3	PL1/2"X8"	0'-8 13/16"	30	A572-GR.50
611B3	1	BEAM			SQ-2
611B3	1	HSS4X4X1/4	7'-9 1/4"	89	GALVANIZED A500-GR.B
p261	2	PL3/8"X4"	0'-4"	3	A572-GR.50
611B4	1	BEAM			SQ-2
611B4	1	HSS4X4X1/4	8'-9 1/4"	101	GALVANIZED A500-GR.B
p261	2	PL3/8"X4"	0'-4"	3	A572-GR.50
		TOTAL WEIGHT THIS DRAWING		1184	

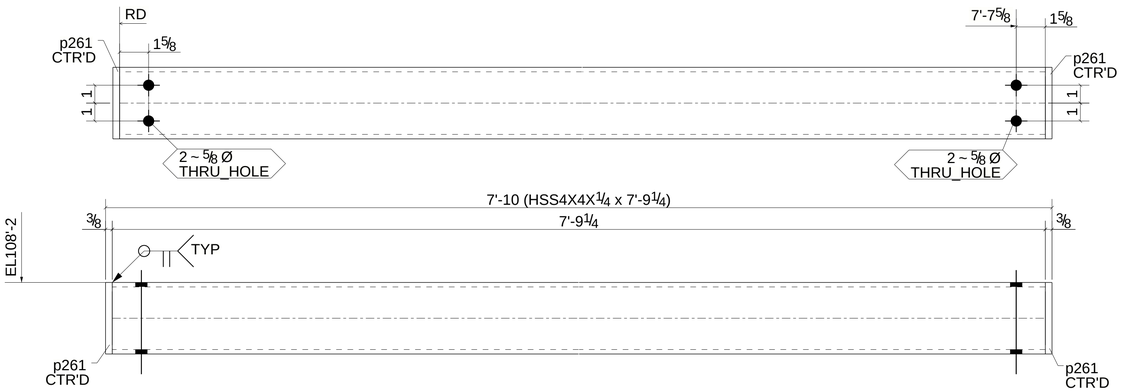

ONE - BEAM - 611B3

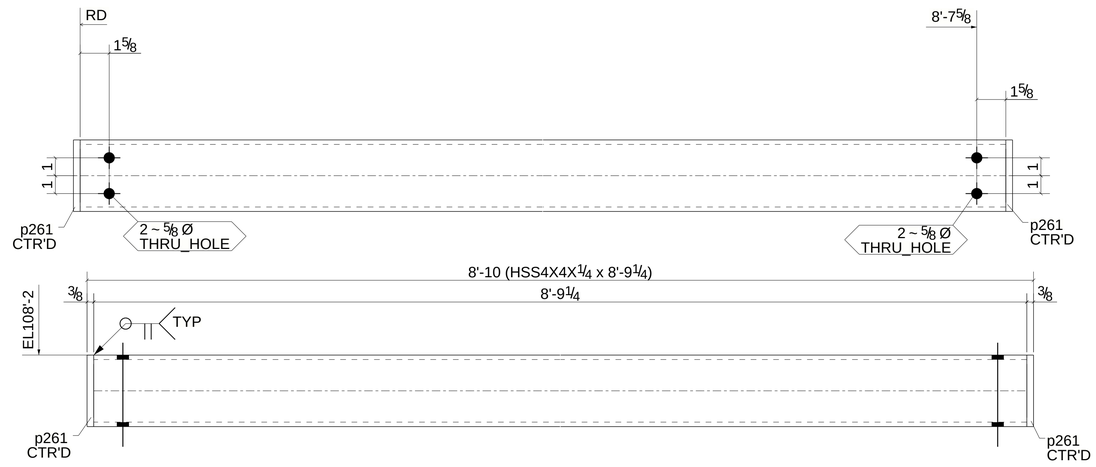

ONE - BEAM - 611B4

REV	DESCRIPTION	ECO	DWN	APPR	APPR	DATE
0	ISSUED FOR FABRICATION					06/09/2026

PROPRIETARY AND CONFIDENTIAL: THIS DRAWING AND ALL INFORMATION AND KNOWLEDGE CONTAINED OR REFERRED HEREIN ARE THE CONFIDENTIAL AND PROPRIETARY PROPERTY OF PRIMA AND AS SUCH ARE INSTRUMENTS OF SERVICE FOR USE SOLELY WITH RESPECT TO THIS PROJECT. THESE INSTRUMENTS OF SERVICE SHALL NOT BE REPRODUCED, TRANSMITTED, DISCLOSED OR USED OTHERWISE IN WHOLE OR IN PART, WITHOUT PRIOR WRITTEN AGREEMENT BY PRIMA AND MUST BE IMMEDIATELY RETURNED OR DESTROYED UPON REQUEST.

Tekla Structures

TOLERANCES UNLESS NOTED
DECIMALS .X .XX +/- 0.13 .XXX +/- 0.062
ANGLES +/- 0.5°
FRAC +/- 1/8"

Miguel Hidalgo, Mexico City

CUSTOMER INFORMATION

1523 HARRISON ST.
1523 HARRISON ST., OAKLAND, CA 94612

DRAWING NUMBER: 611
REVISION: 0
REF.:
DOC. OWNER:
PROJECT NO.: 5220
PART/MATERIAL NO.: BEAM
SCALE: 1:12
SIZE: D
SHEET: 1 OF 1