


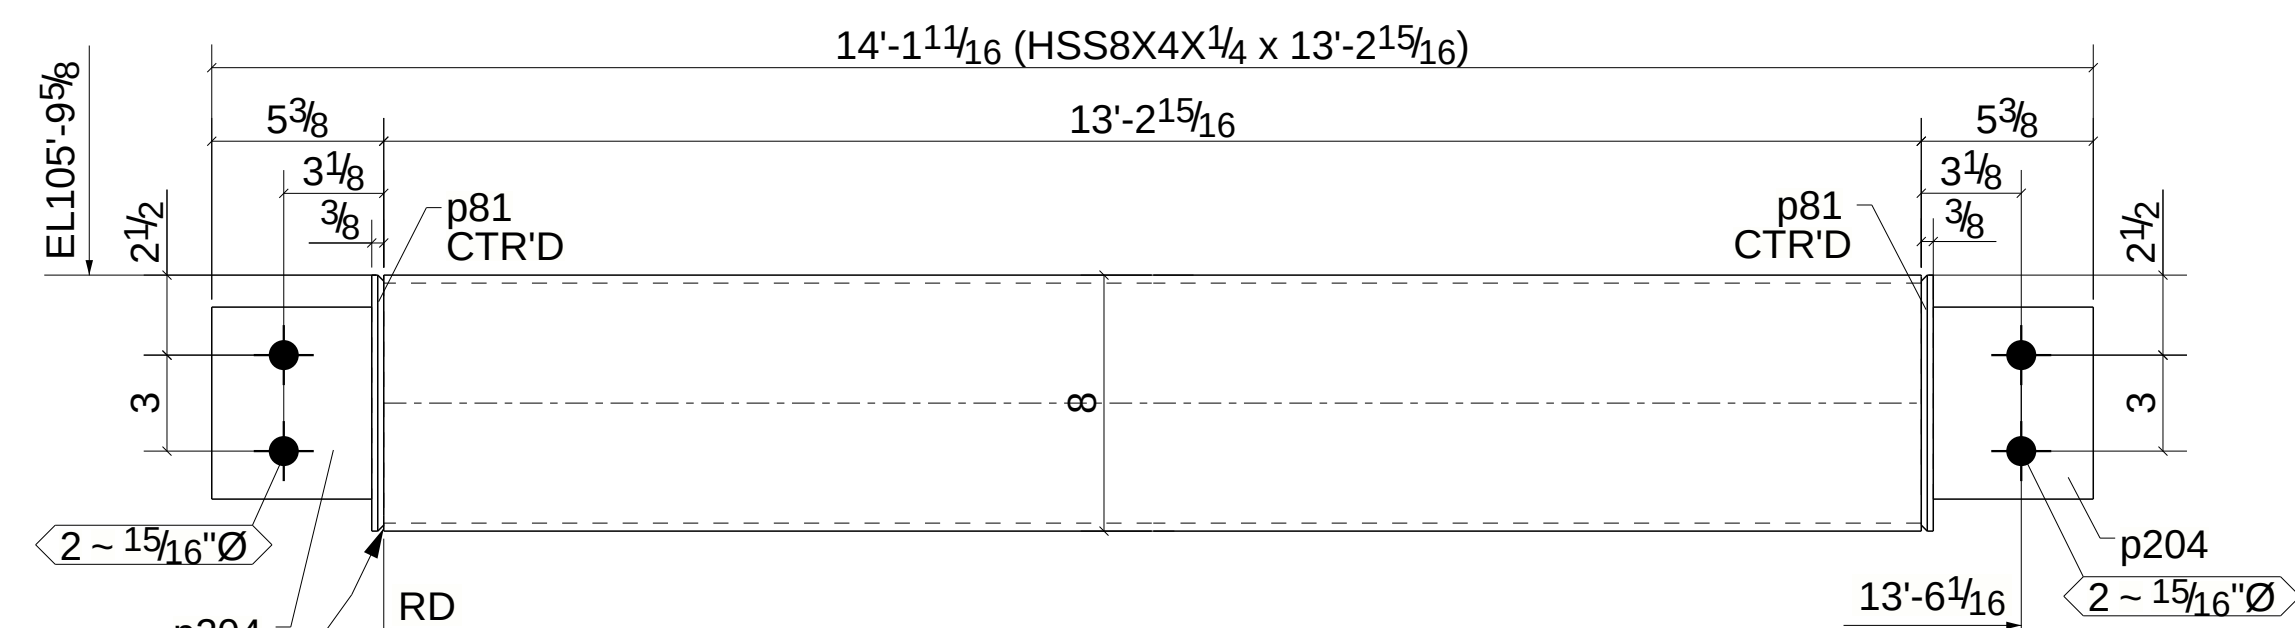


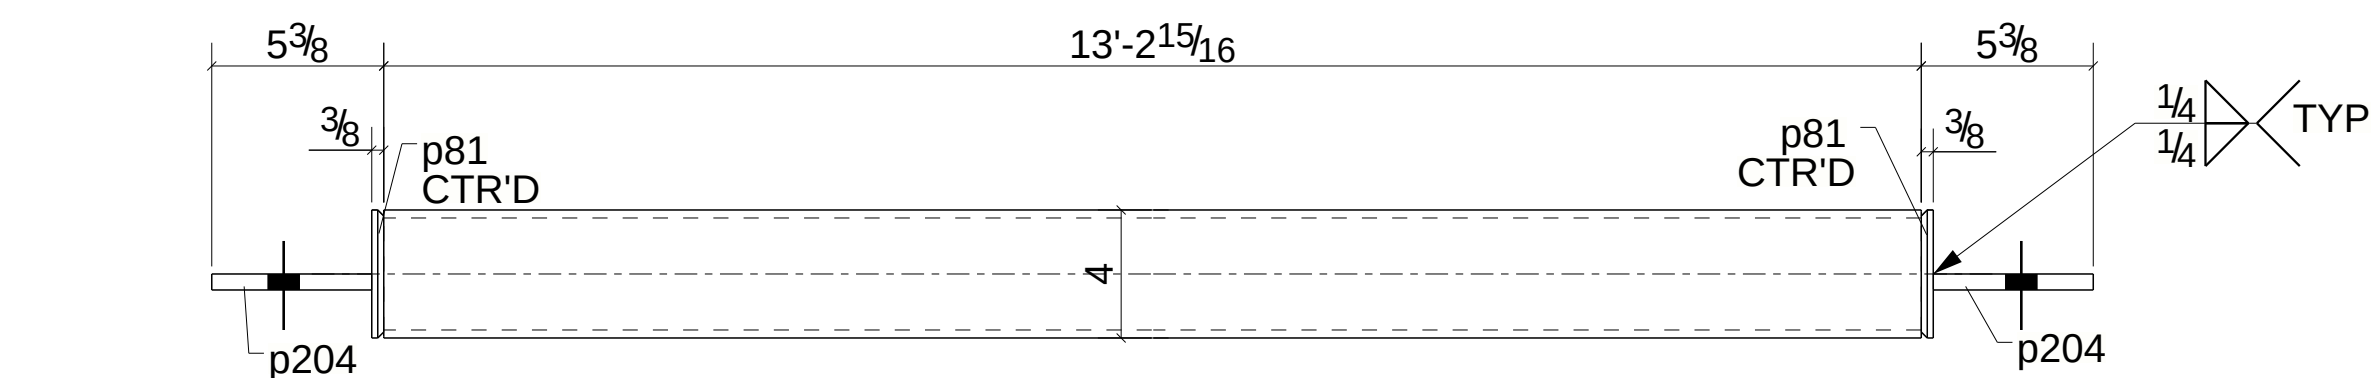

ONE - BEAM - 612B1

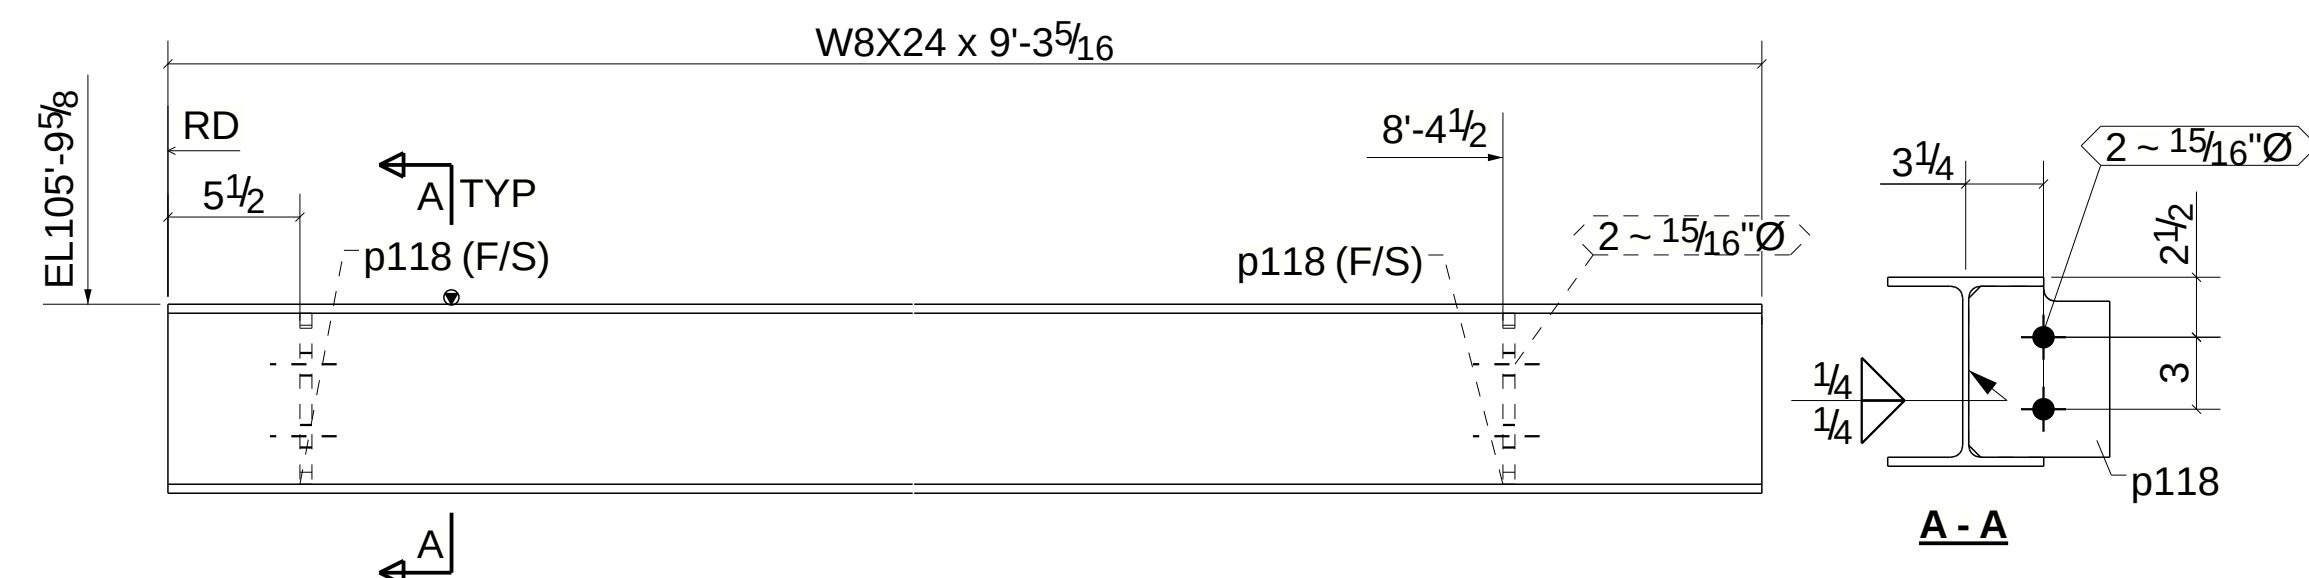

ONE - BEAM - 612B2

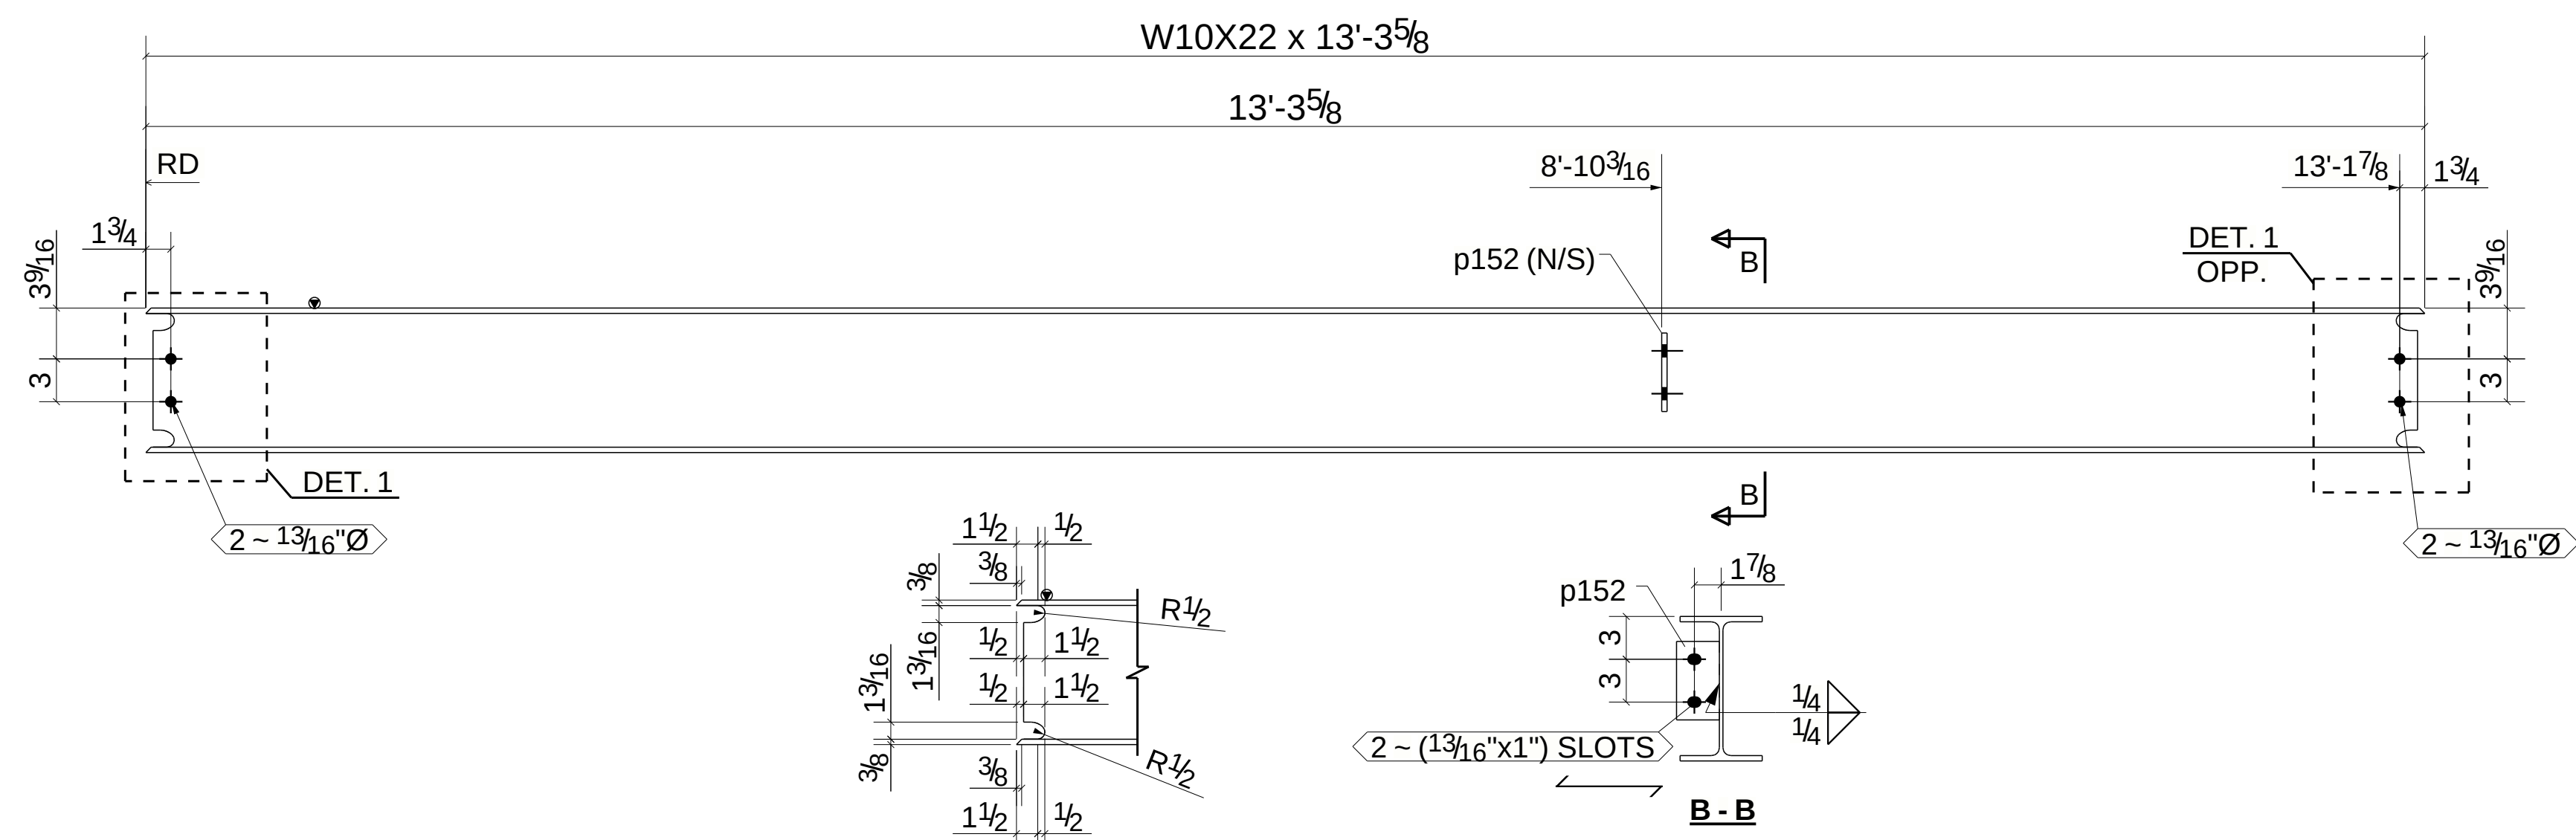

DETAIL 1

ONE - BEAM - 612B3

BILL OF MATERIAL					
MARK	QTY	DESCRIPTION	LENGTH	WEIGHT	REMARKS
612B1	1	BEAM			SQ-2
612B1	1	HSSBx4x1/4	13'-2 15/16"	236	SHOP_PRIMER A500-GR.B
B1	2	PL3/8"x4"	0'-8"	7	A572-GR.50
B204	2	PL1/2"x5"	0'-6"	9	A572-GR.50
612B2	1	BEAM			SQ-2
612B2	1	W8x24	9'-3 5/16"	223	SHOP_PRIMER A992
B118	2	PL1/2"x5 7/8"	0'-7 1/8"	11	A572-GR.50
612B3	1	BEAM			SQ-2
612B3	1	W10x22	13'-3 5/8"	294	GALVANIZED A992
B152	1	PL3/8"x3"	0'-5 1/2"	2	A572-GR.50
		TOTAL WEIGHT THIS DRAWING		782	

--	--	