

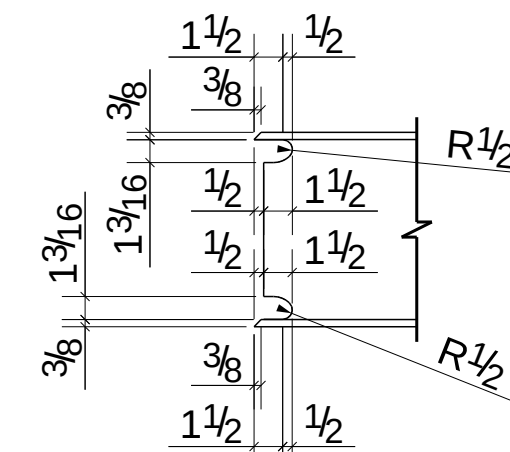
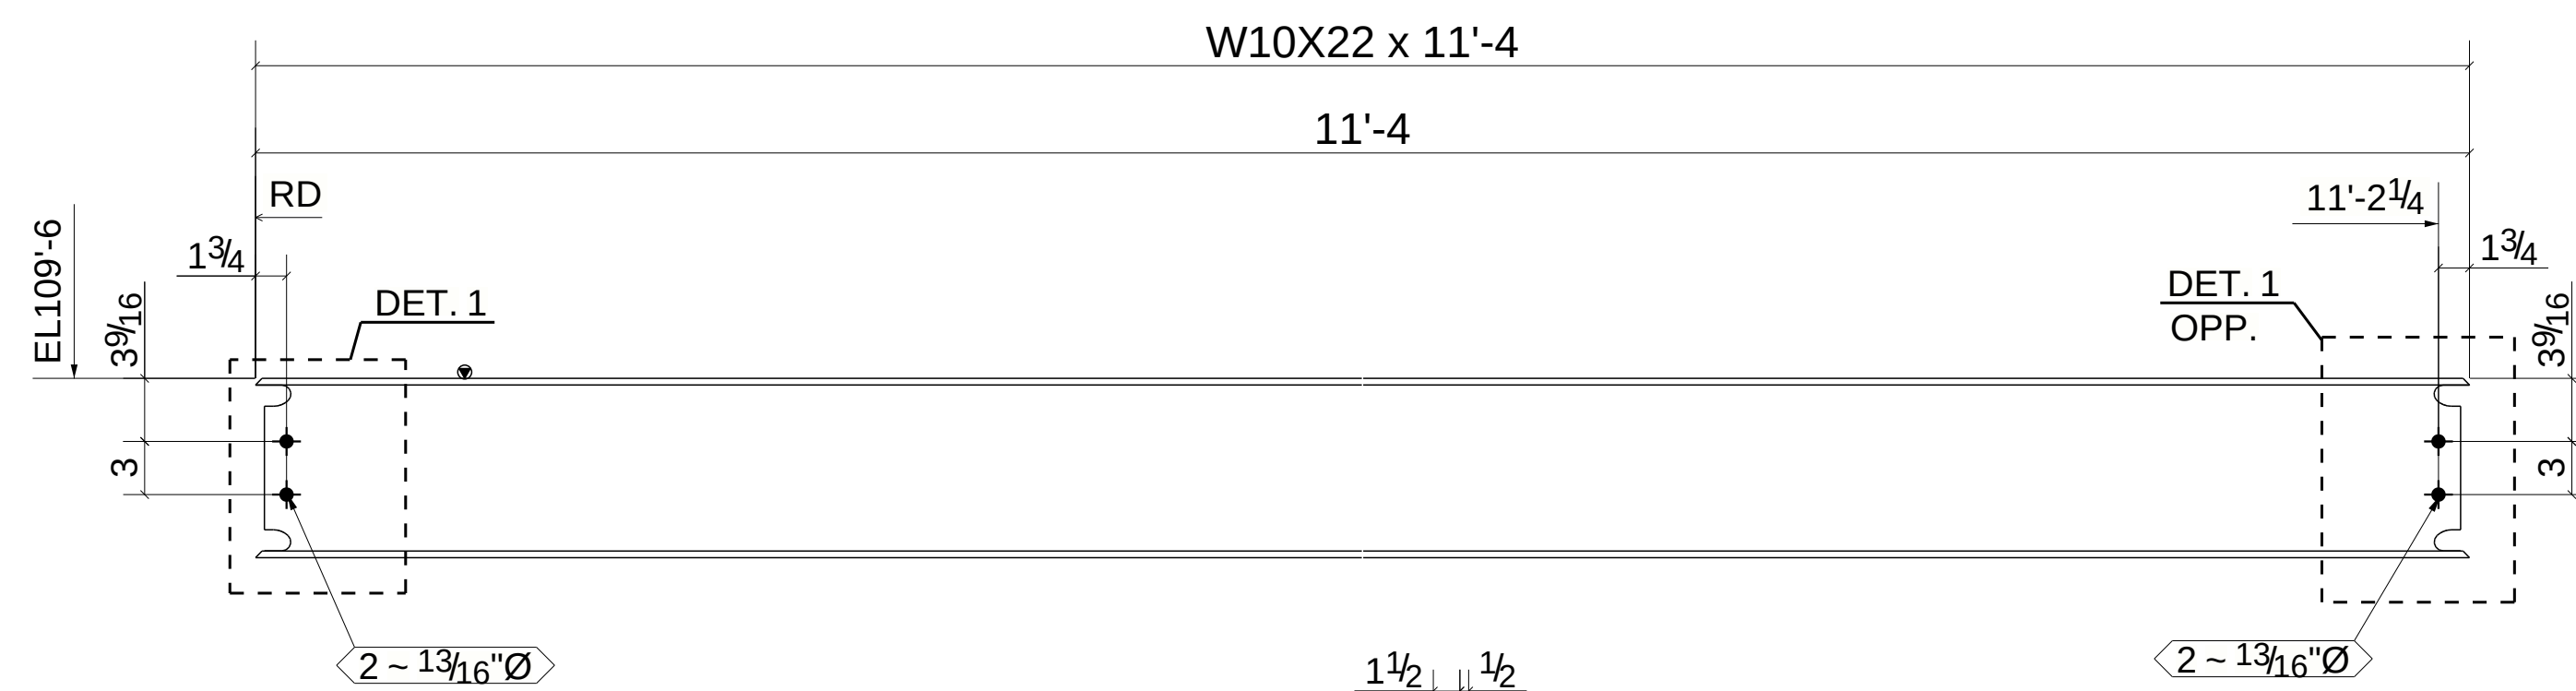
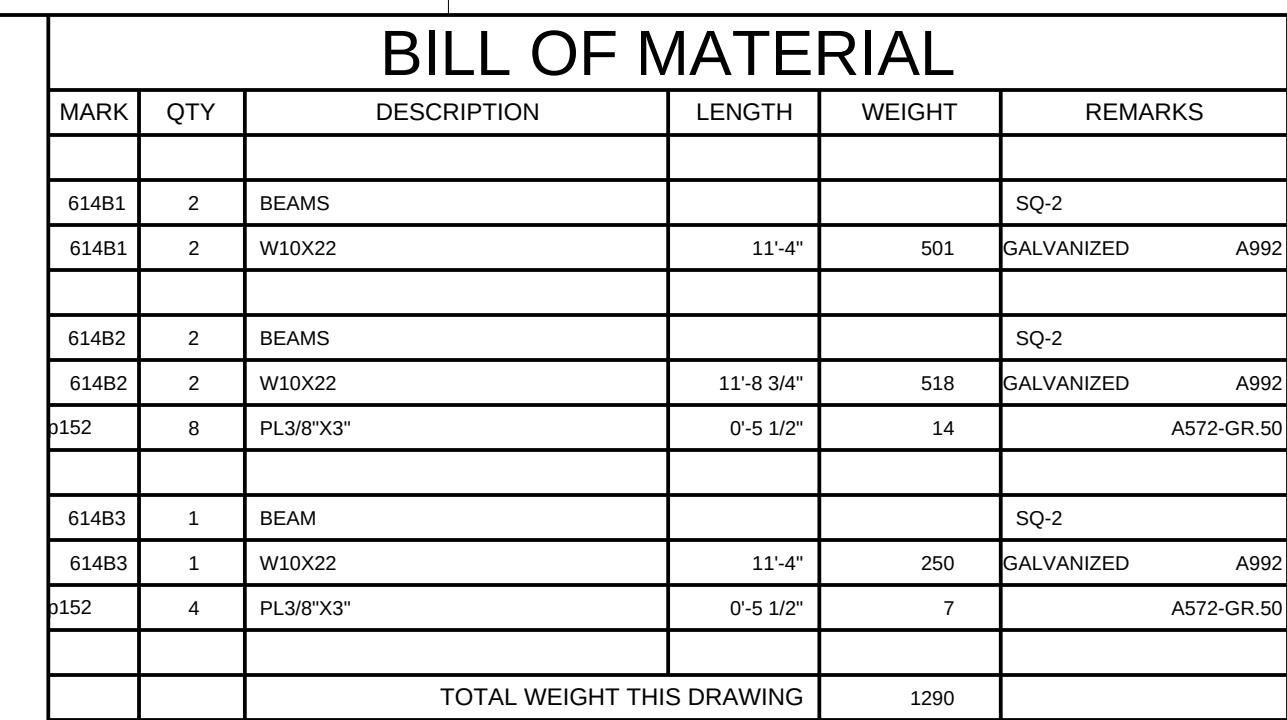



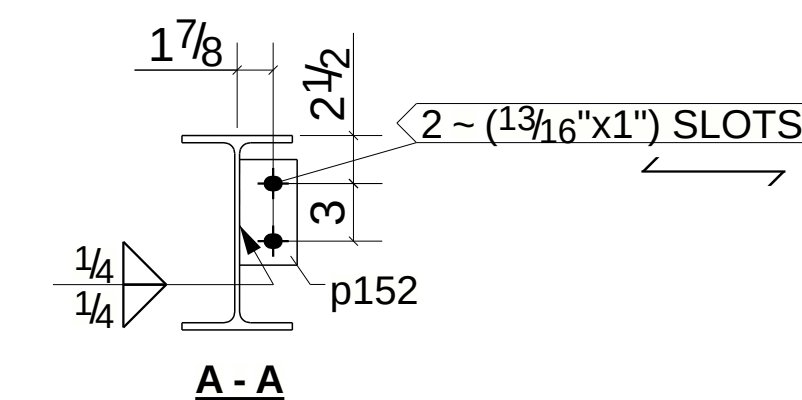


DETAIL 1

2 - BEAMS - 614B1

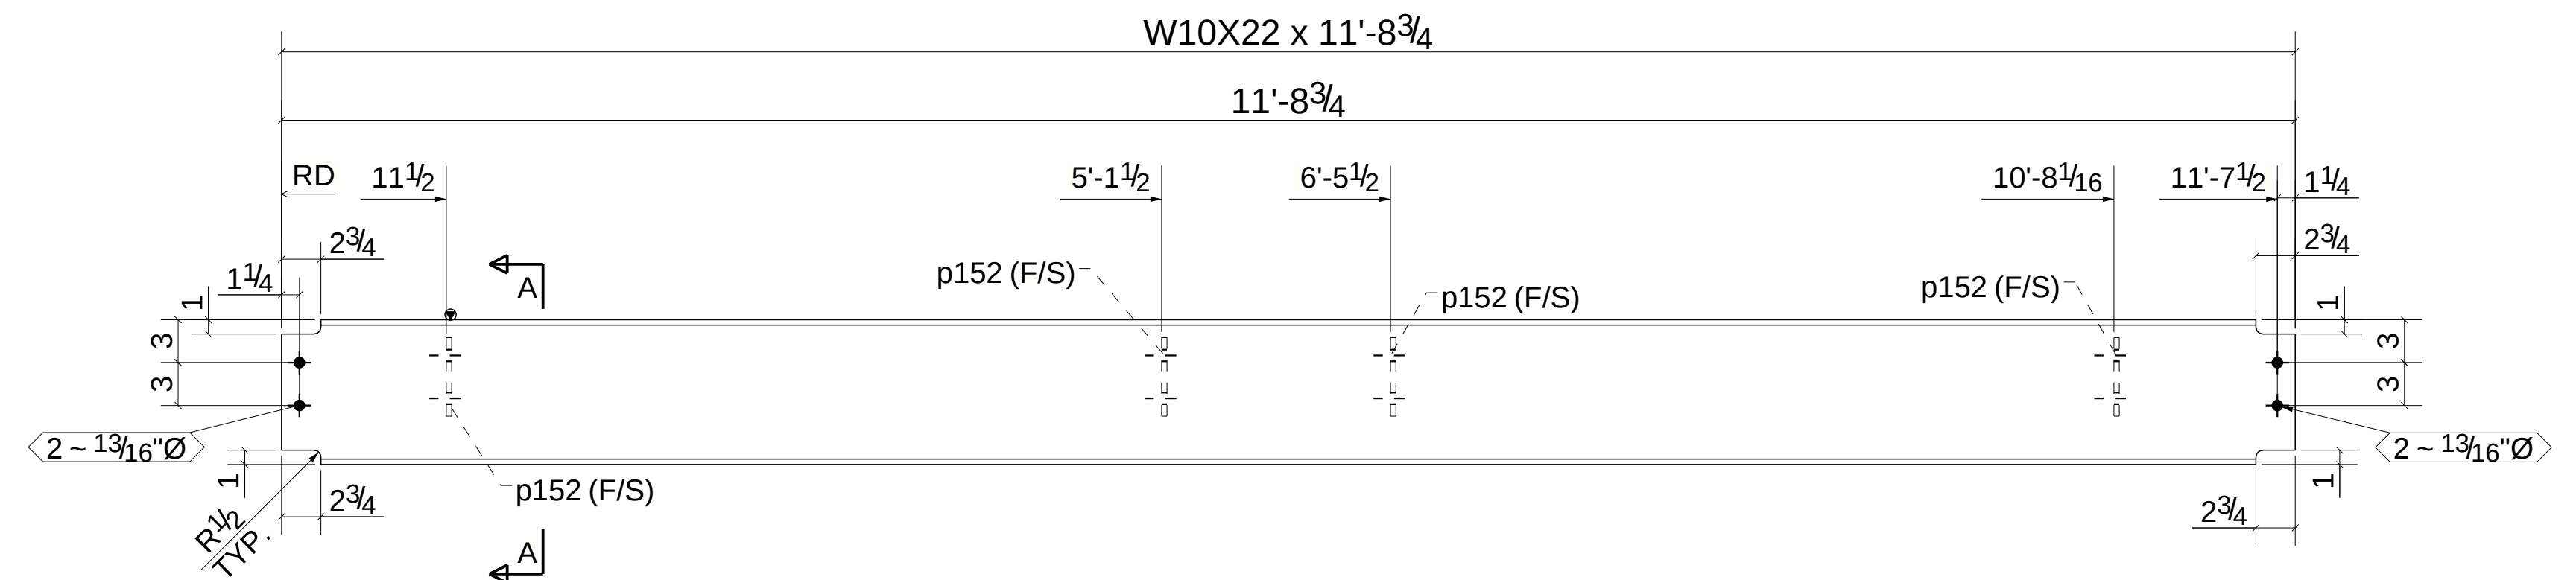

2 - BEAMS - 614B2

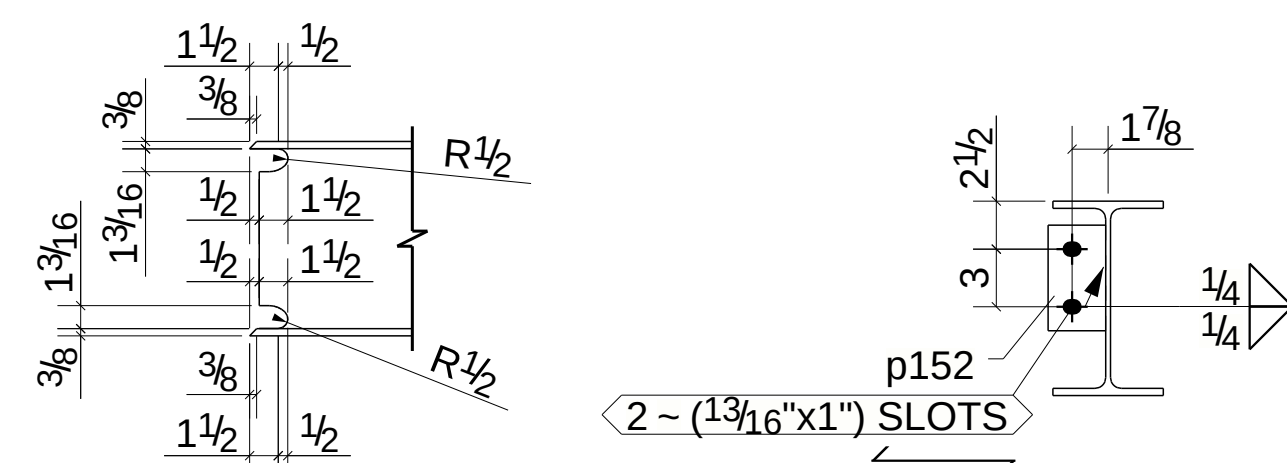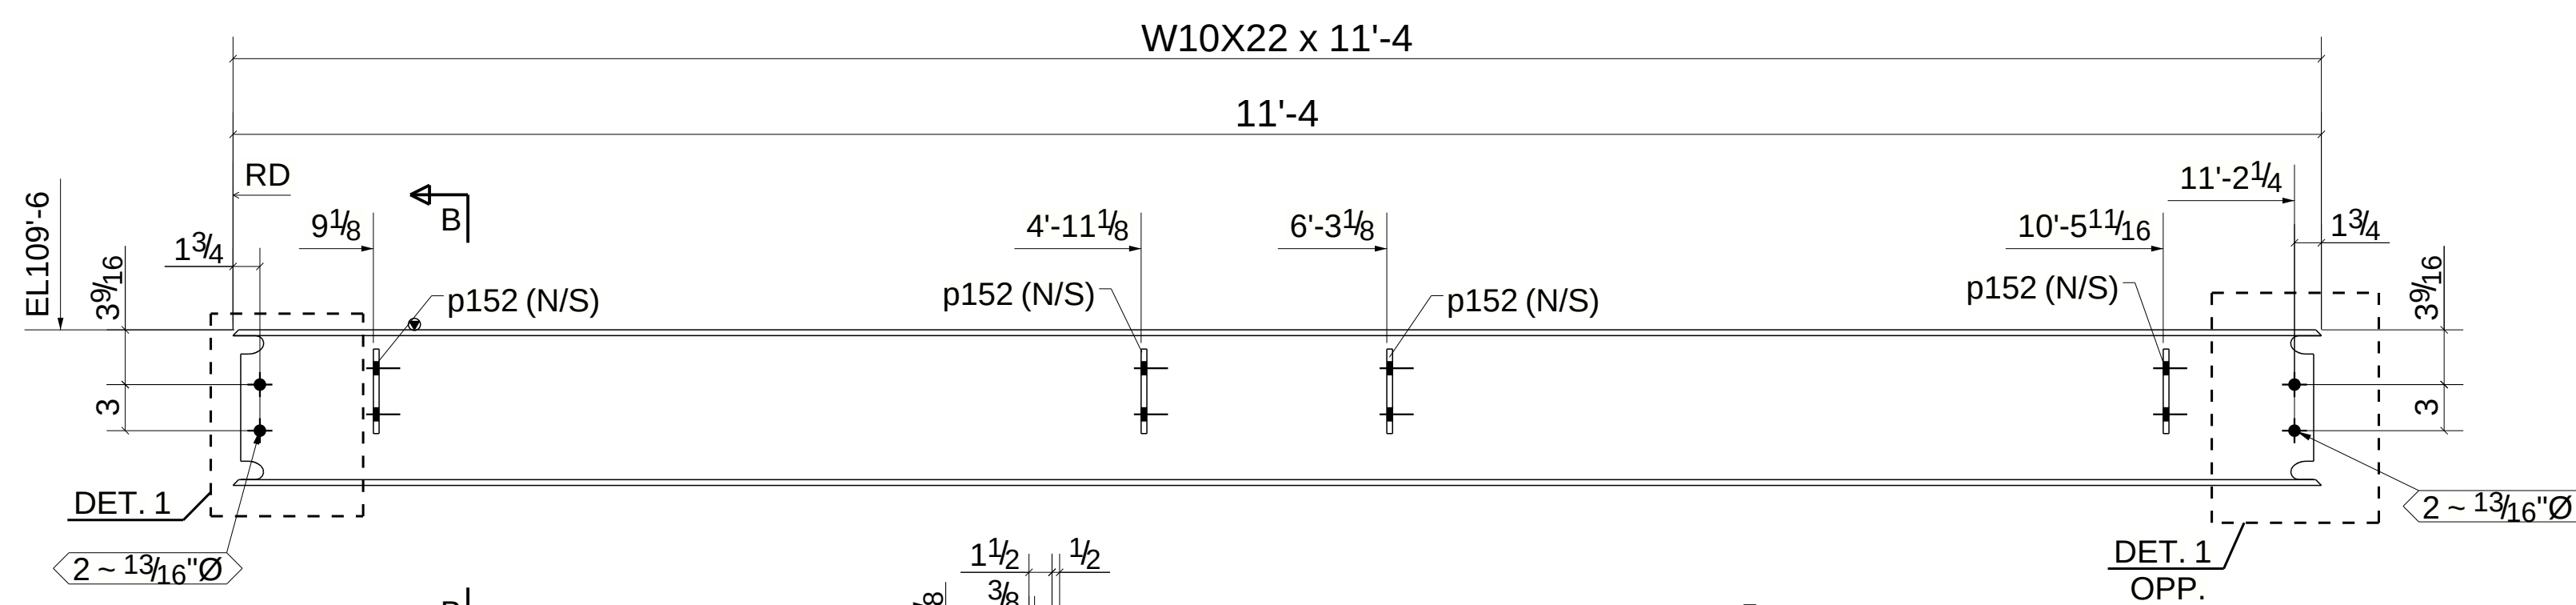

DETAIL 1

ONE - BEAM - 614B3

										TOLERANCES UNLESS NOTED										Miguel Hidalgo, Mexico City										CUSTOMER INFORMATION										1523 HARRISON ST. 1523 HARRISON ST., OAKLAND, CA 94612										DRAWING NUMBER										REVISION																			
	614										0																			
0 ISSUED FOR FABRICATION	06/09/2026																													
REV DESCRIPTION										ECO DWN APPR APPR DATE	
PROPRIETARY AND CONFIDENTIAL: THIS DRAWING AND ALL INFORMATION AND KNOWLEDGE CONTAINED OR REFERRED HEREIN ARE THE CONFIDENTIAL AND PROPRIETARY PROPERTY OF PRIMA AND AS SUCH ARE INSTRUMENTS OF SERVICE FOR USE SOLELY WITH RESPECT TO THIS PROJECT. THESE INSTRUMENTS OF SERVICE SHALL NOT BE REPRODUCED, TRANSMITTED, DISCLOSED OR USED OTHERWISE IN WHOLE OR IN PART, WITHOUT PRIOR WRITTEN AGREEMENT BY PRIMA, AND MUST BE IMMEDIATELY RETURNED OR DESTROYED UPON REQUEST.	
																														PROJECT NO.										PART/MATERIAL NO.										SCALE										SIZE										SHEET									
																														5220										BEAM										1:12										D										1 OF 1									