



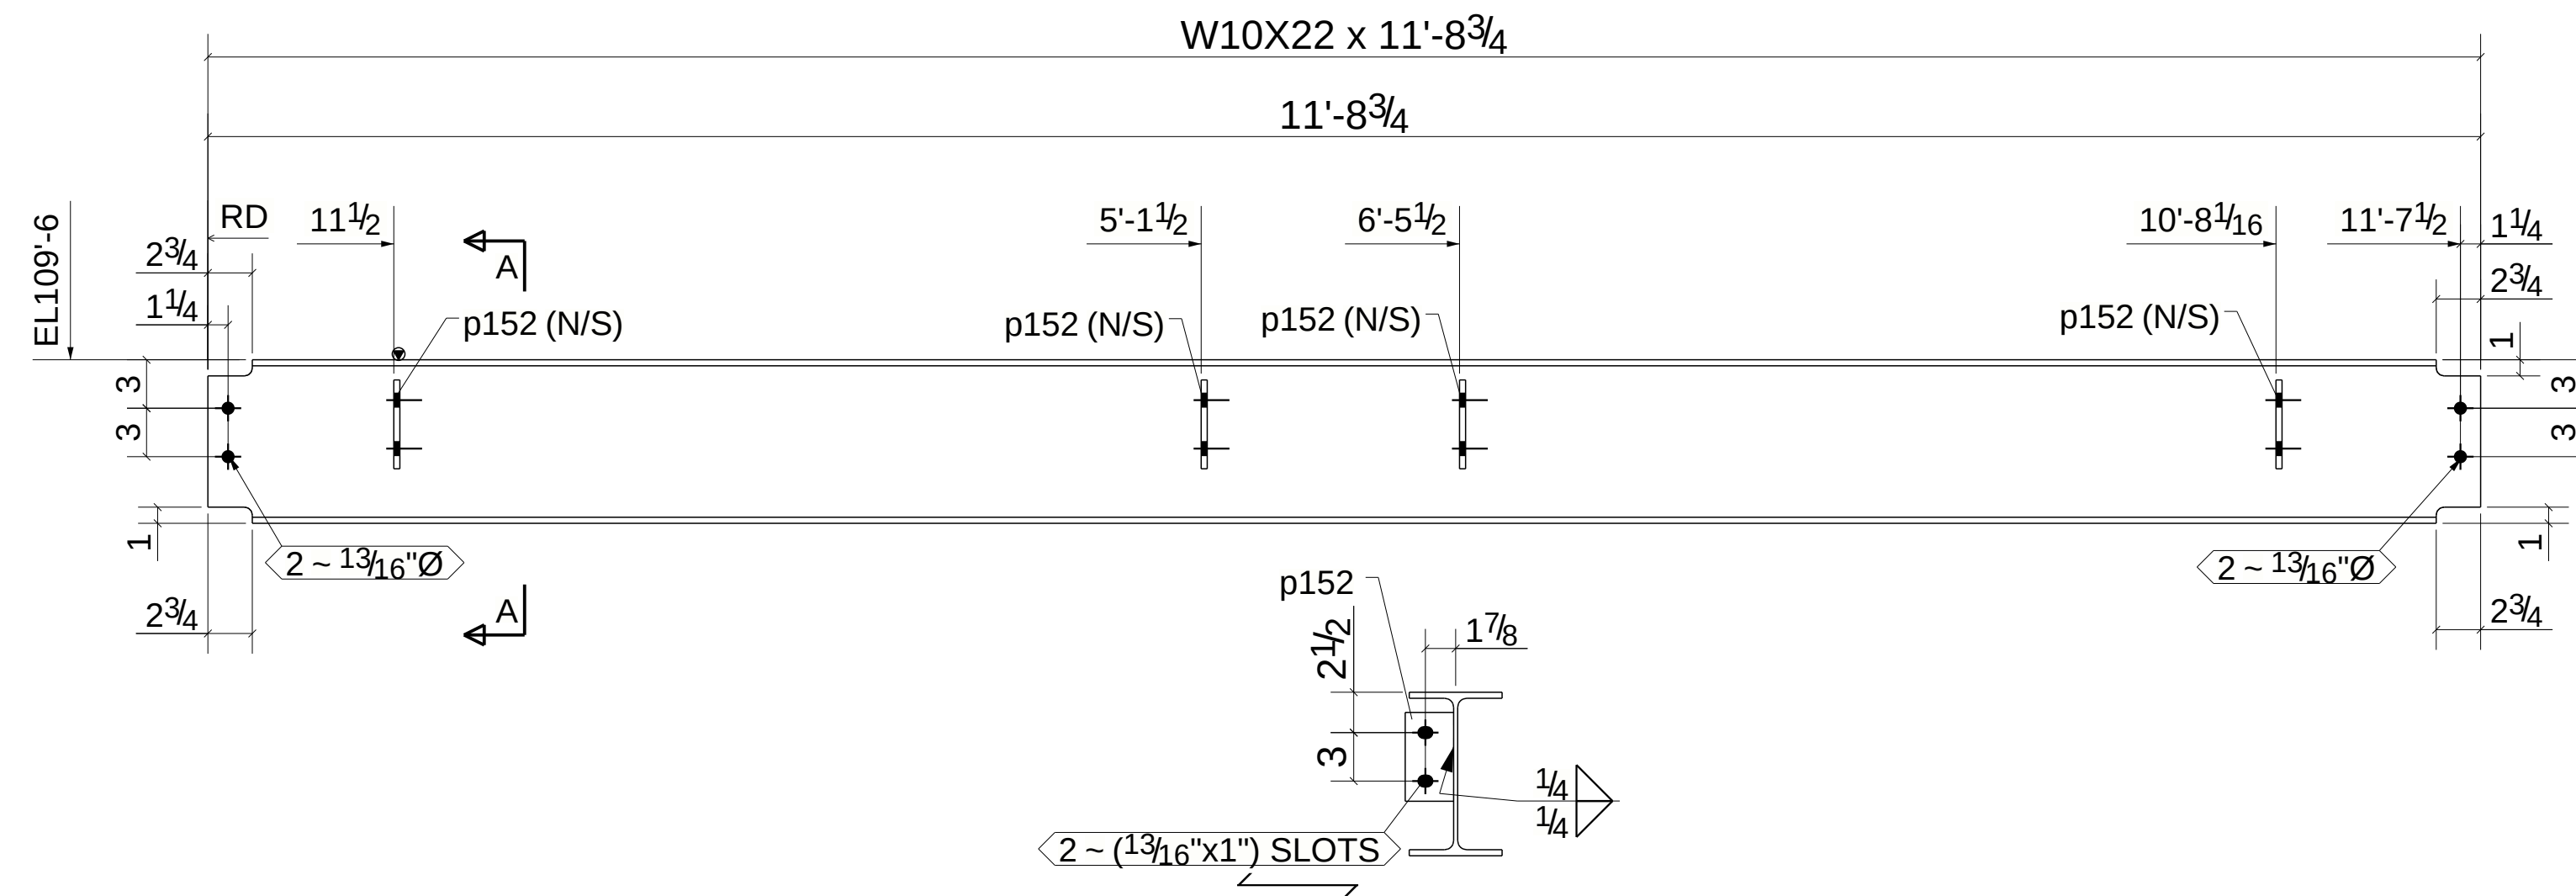


ONE - BEAM - 615B1

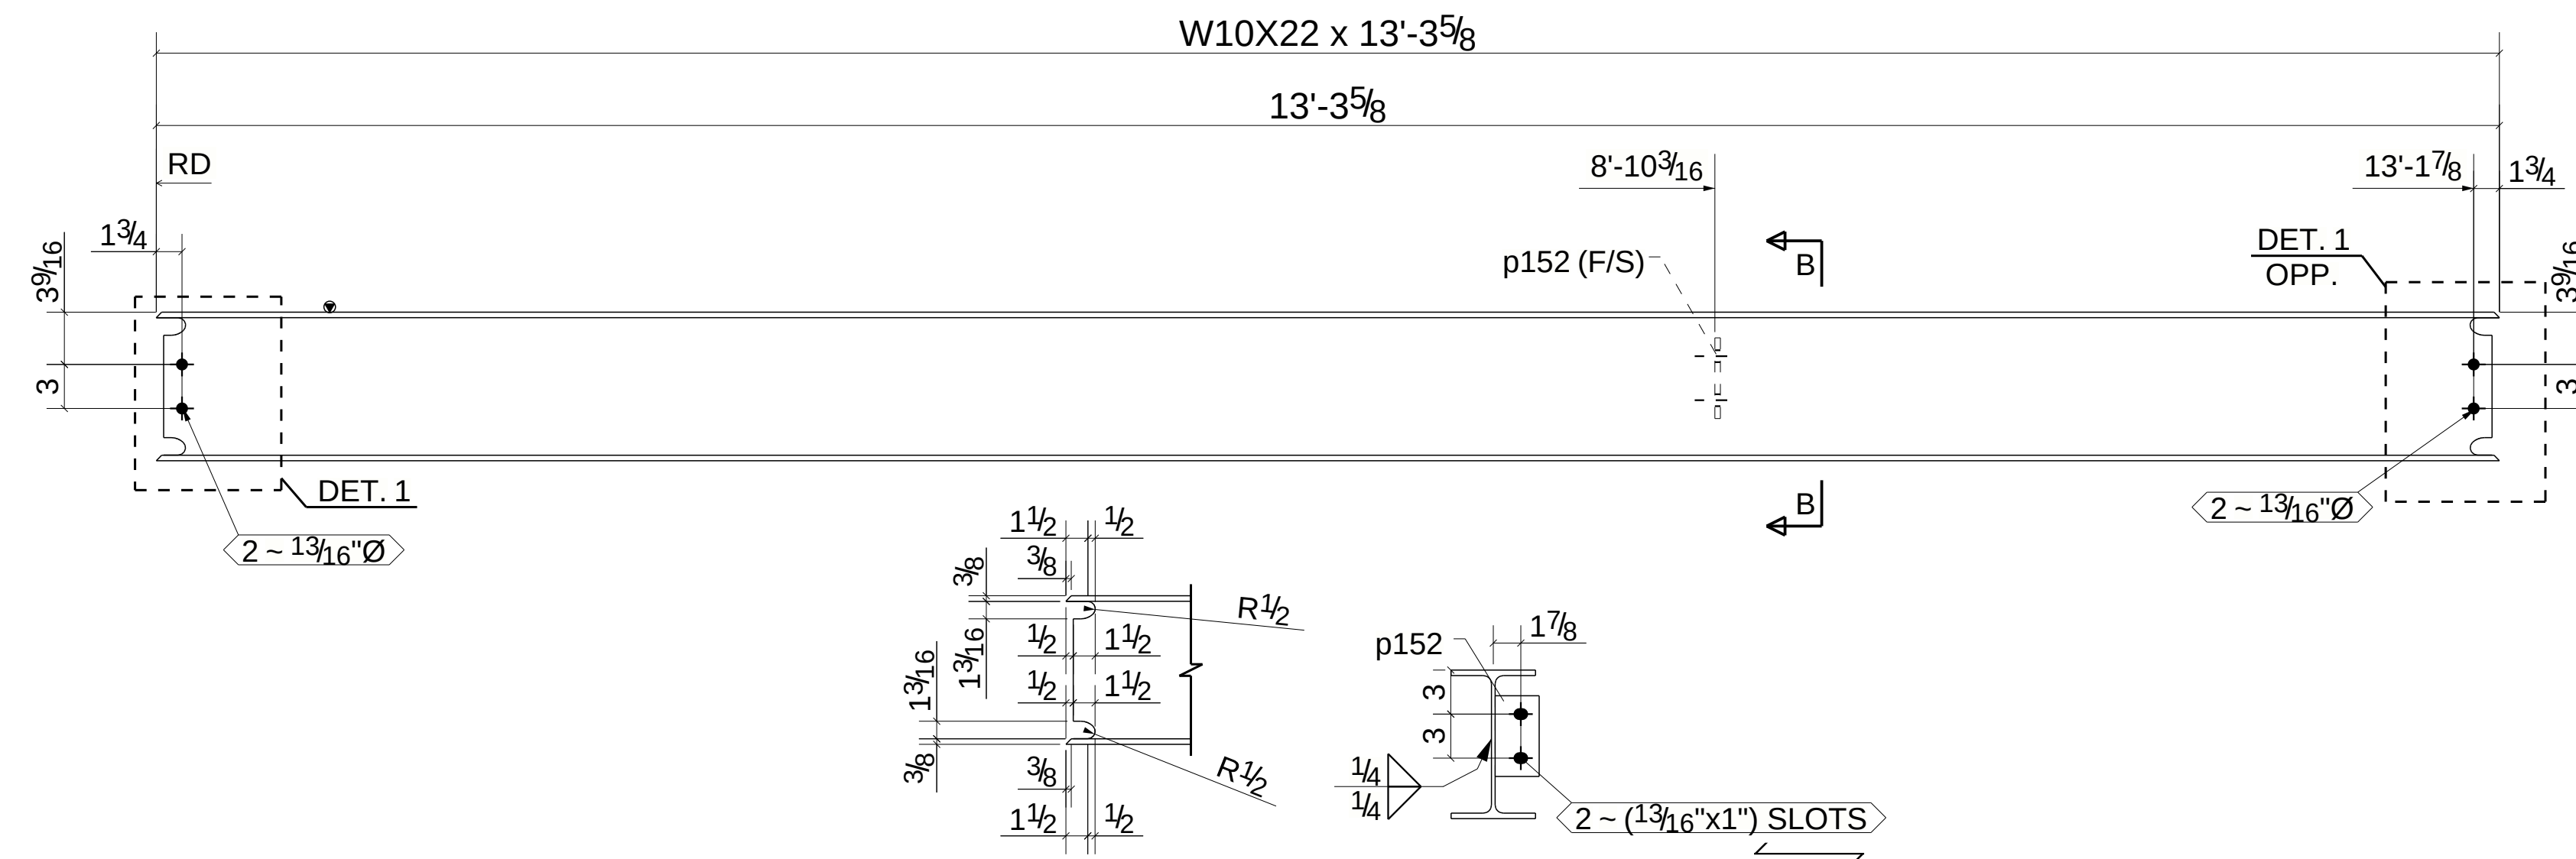


DETAIL 1

ONE - BEAM - 615B2

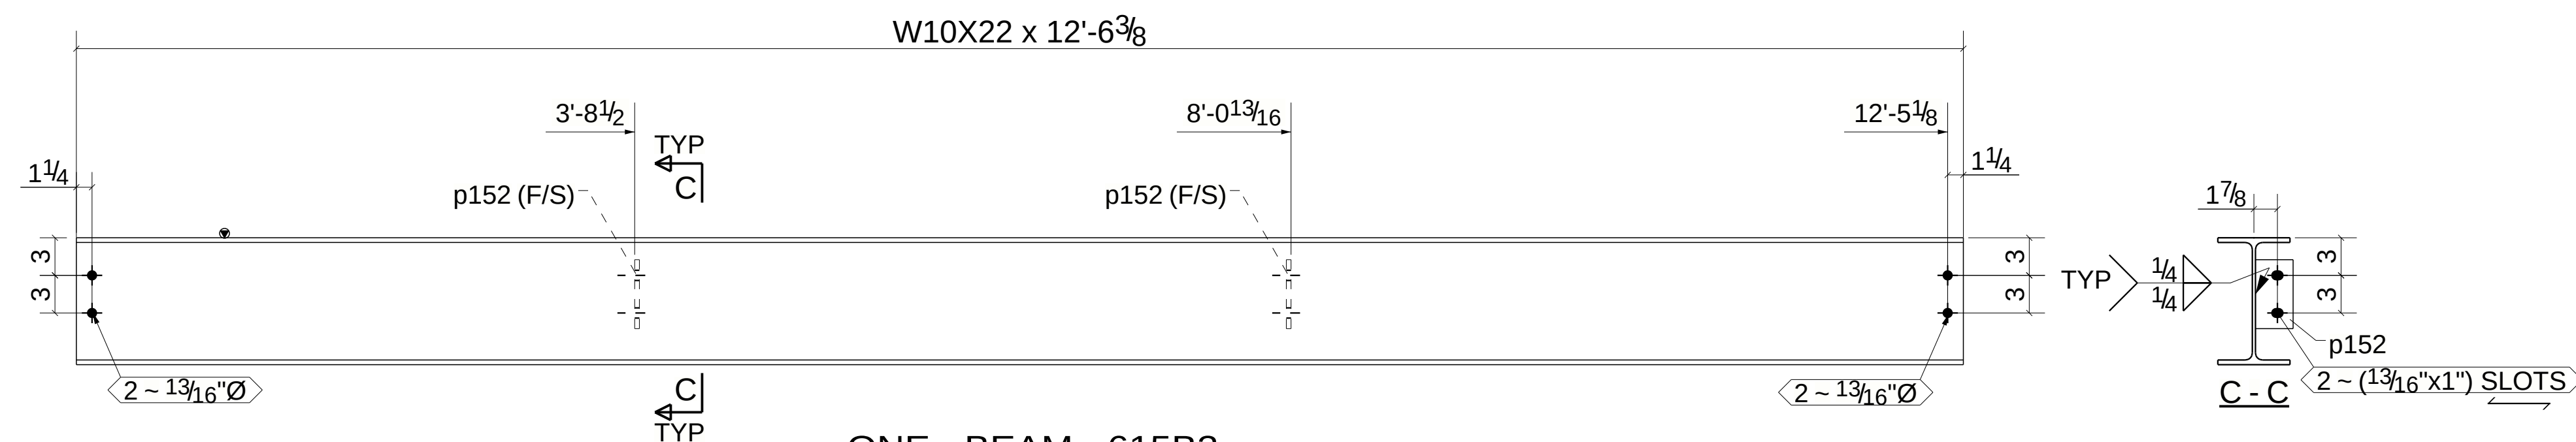

ONE - BEAM - 615B3

BILL OF MATERIAL					
MARK	QTY	DESCRIPTION	LENGTH	WEIGHT	REMARKS
615B1	1	BEAM			SQ-2
615B1	1	W10X22	11'-8 3/4"	259	GALVANIZED A992
p152	4	PL3/8"x3"	0'-5 1/2"	7	A572-GR.50
615B2	1	BEAM			SQ-2
615B2	1	W10X22	13'-3 5/8"	294	GALVANIZED A992
p152	1	PL3/8"x3"	0'-5 1/2"	2	A572-GR.50
615B3	1	BEAM			SQ-2
615B3	1	W10X22	12'-6 3/8"	277	GALVANIZED A992
p152	2	PL3/8"x3"	0'-5 1/2"	4	A572-GR.50
TOTAL WEIGHT THIS DRAWING				842	

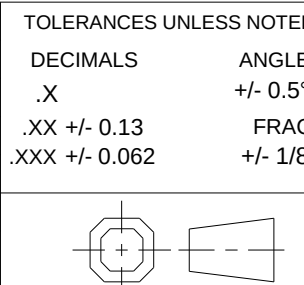[illegible]

Miguel Hidalgo,
Mexico City

CUSTOMER INFORMATION

1523 HARRISON ST.
1523 HARRISON ST., OAKLAND, CA 94612

DRAWING NUMBER

615

REVISION

0

REF.:		DOC. OWNER:		
PROJECT NO. 5220	PART/MATERIAL NO. BEAM	SCALE 1:12	SIZE D	SHEET 1 OF 1