



WT4X15.5 x 11'-2

ONE - BEAM - 616B1

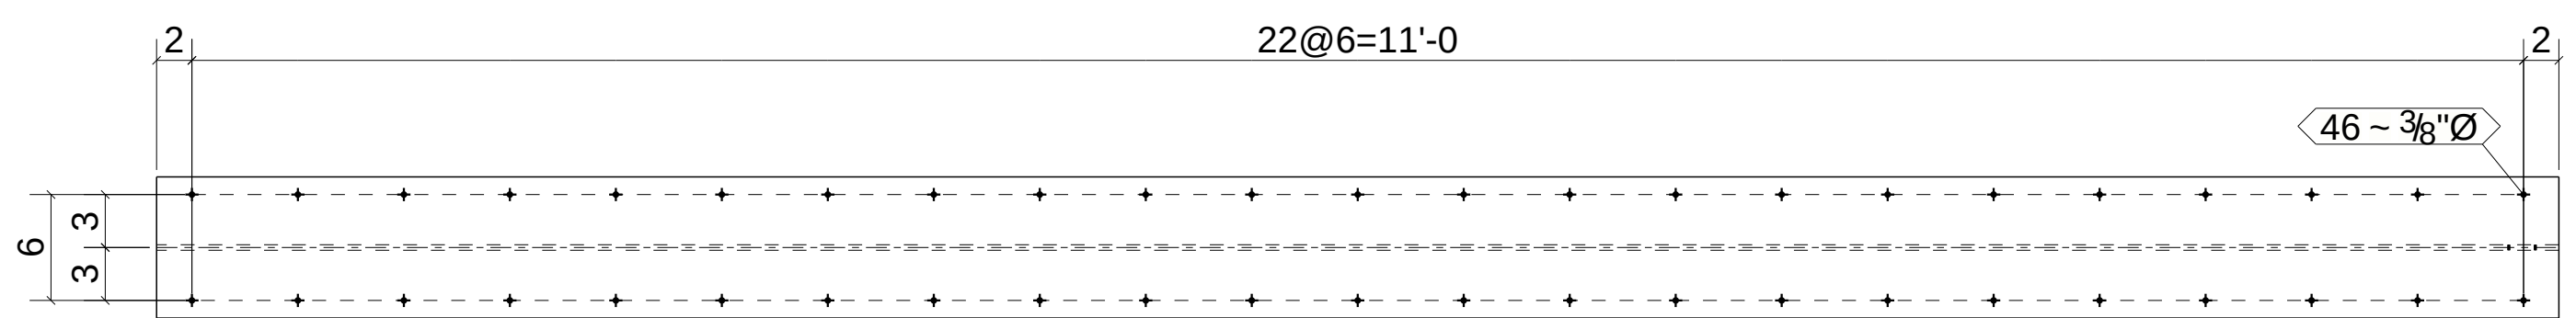


WT4X15.5 x 11'-4

ONE - BEAM - 616B3

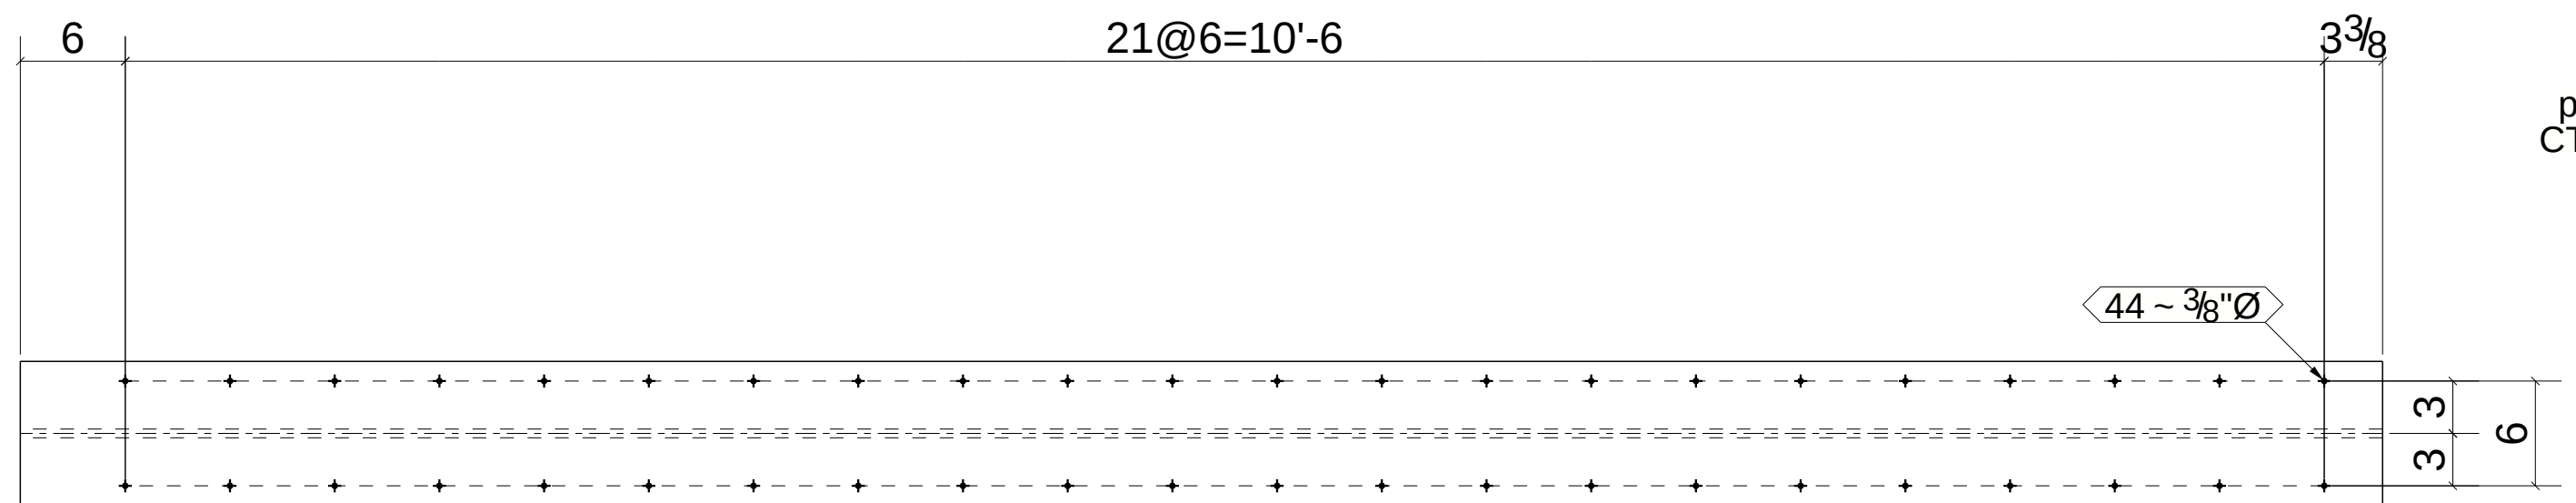WT4X29 x 11'-3³/₈

ONE - BEAM - 616B5

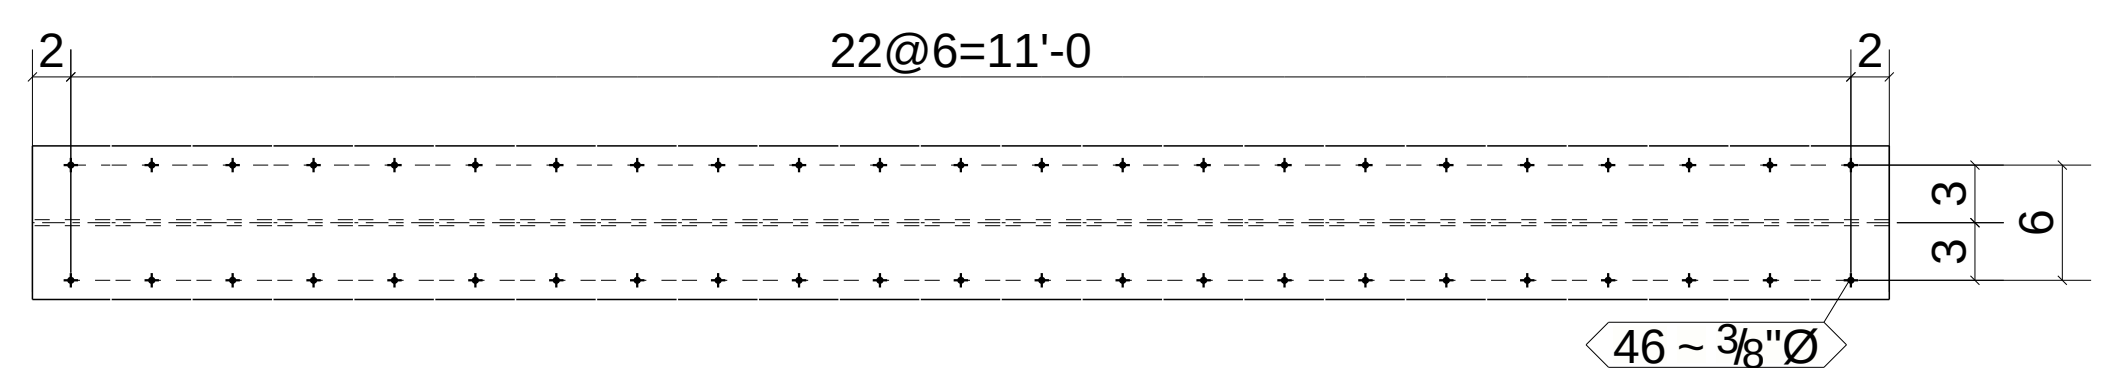


WT4X15.5 x 11'-4

3 - BEAMS - 616B2



BILL OF MATERIAL					
MARK	QTY	DESCRIPTION	LENGTH	WEIGHT	REMARKS
616B1	1	BEAM			SQ-2
616B1	1	WT4X15.5	11'-2"	173	SHOP_PRIMER A992
616B2	3	BEAMS			SQ-2
616B2	3	WT4X15.5	11'-4"	528	SHOP_PRIMER A992
616B3	1	BEAM			SQ-2
616B3	1	WT4X15.5	11'-4"	176	SHOP_PRIMER A992
616B5	1	BEAM			SQ-2
616B5	1	WT4X29	11'-3 3/8"	328	SHOP_PRIMER A992
616B6	1	BEAM			SQ-2
616B6	1	HSS8X4X5/16	6'-10 13/16"	151	SHOP_PRIMER A500-GR.B
z285	4	L6X3-1/2X1/2	0'-4"	20	A572-GR.50
p140	2	PL1/4"x4"	0'-8"	5	A572-GR.50
z259	4	PL1/4"x3"	0'-4"	3	A572-GR.50
		TOTAL WEIGHT THIS DRAWING		1384	

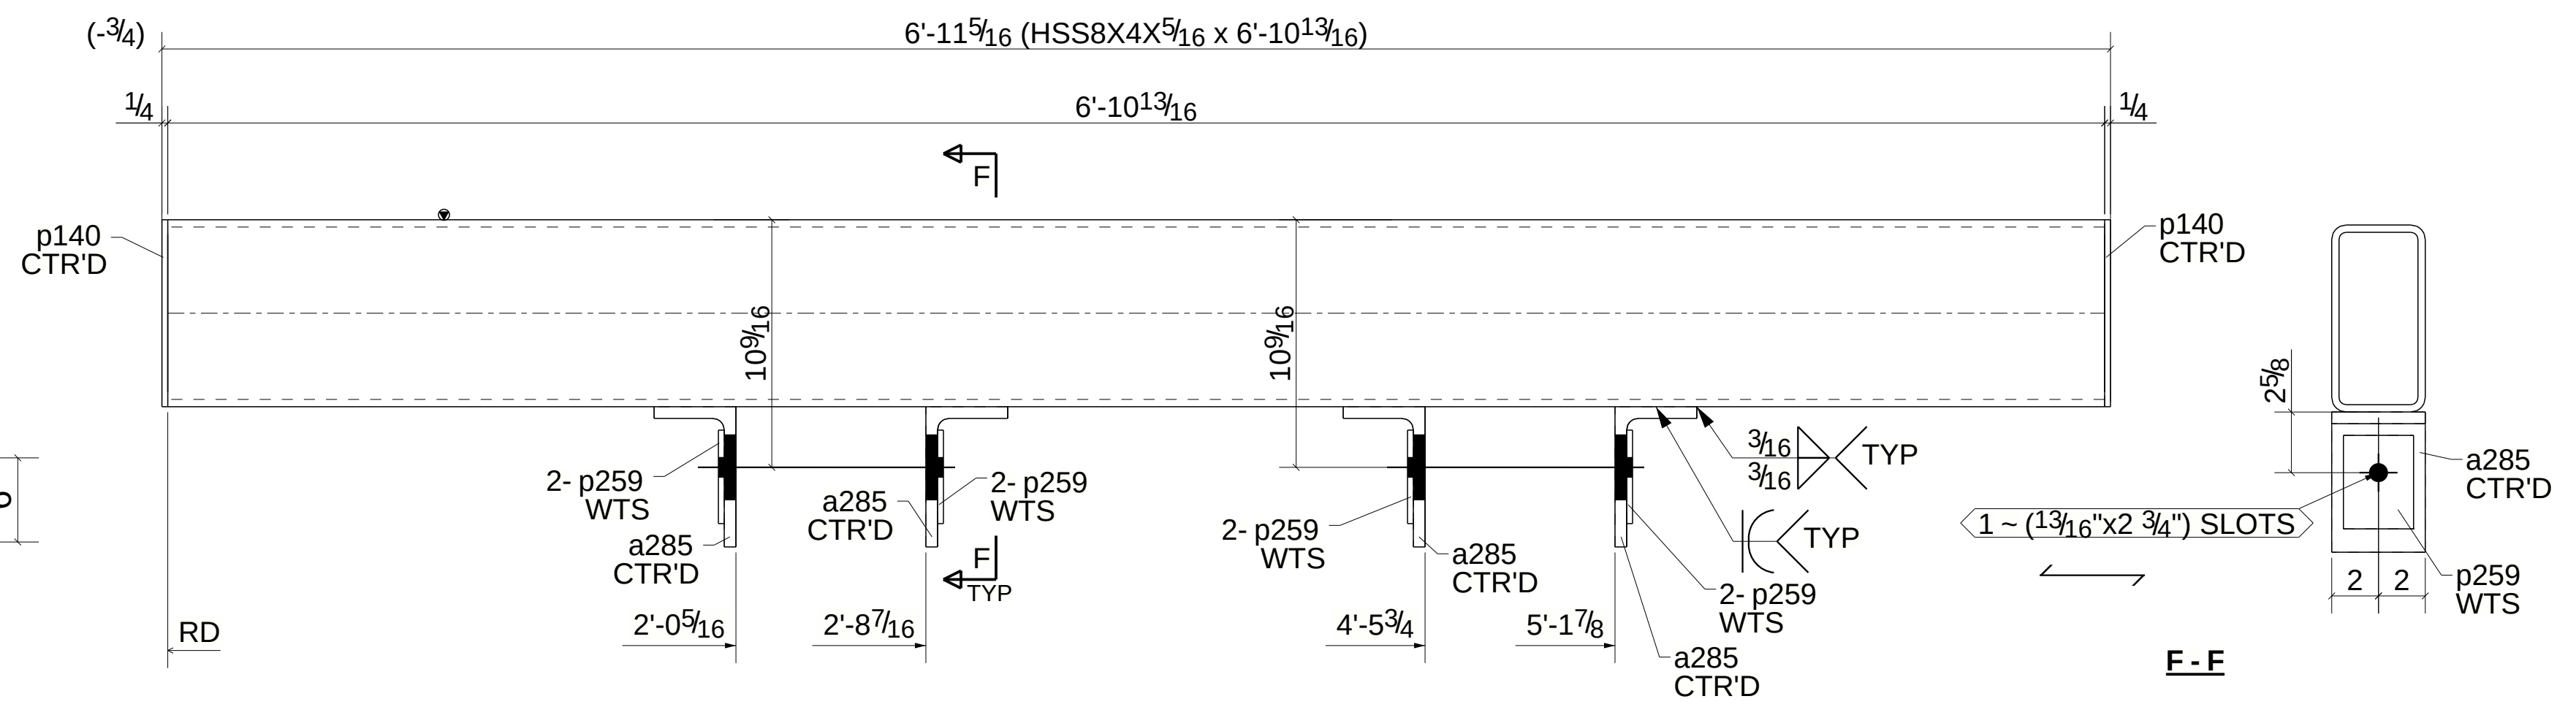

ONE - BEAM - 616B6

--	--	