




ONE - PERIMETER ANGLE - 622A1

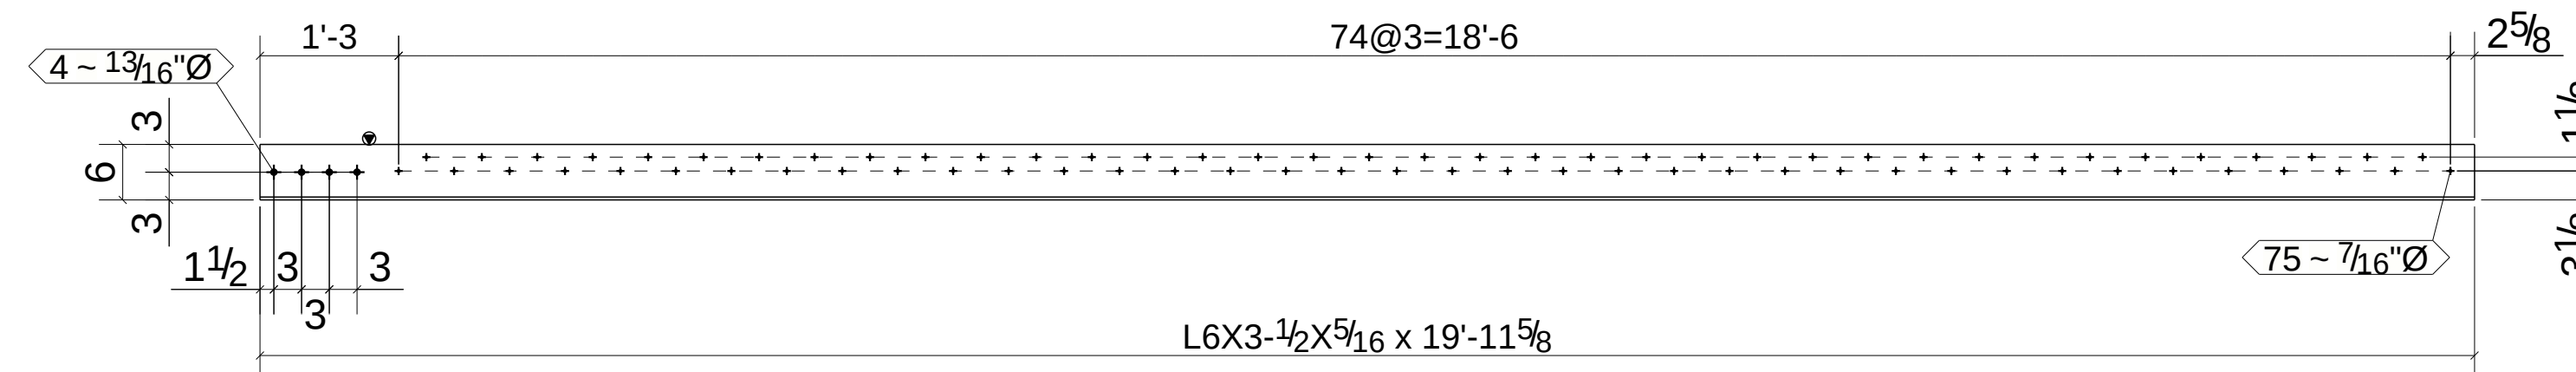


ONE - PERIMETER ANGLE - 622A2

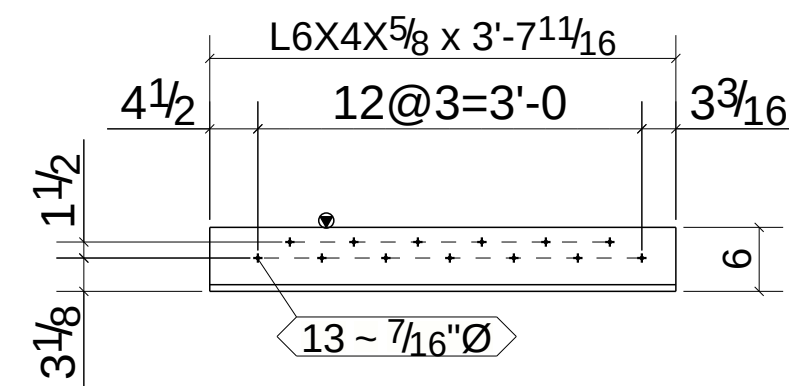

ONE - PERIMETER ANGLE - 622A3

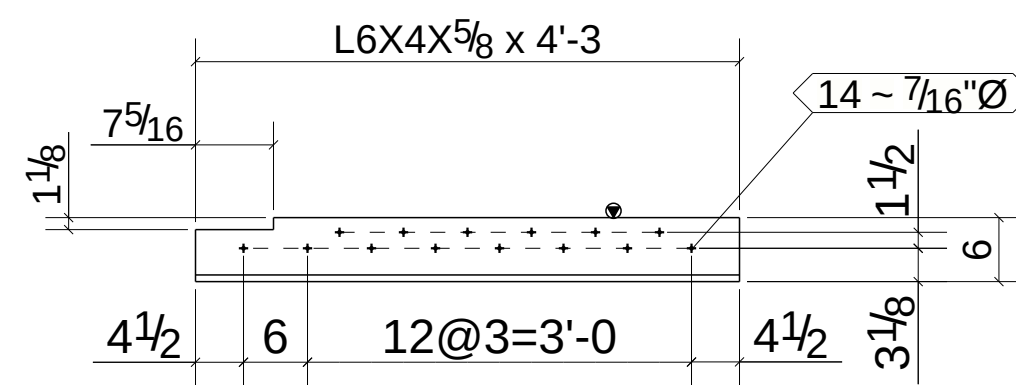

ONE - PERIMETER ANGLE - 622A4

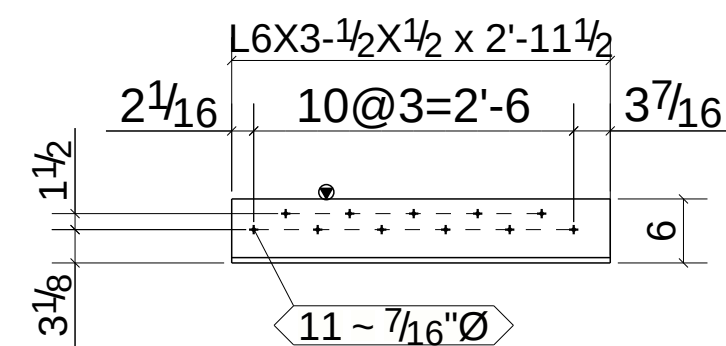

ONE - PERIMETER ANGLE - 622A5

BILL OF MATERIAL					
MARK	QTY	DESCRIPTION	LENGTH	WEIGHT	REMARKS
622A1	1	PERIMETER ANGLE			SQ-2
622A1	1	L6X3-1/2X5/16	20'-0"	197	SHOP_PRIMER A572-GR 50
622A2	1	PERIMETER ANGLE			SQ-2
622A2	1	L6X3-1/2X5/16	19'-11 5/8"	196	SHOP_PRIMER A572-GR 50
622A3	1	PERIMETER ANGLE			SQ-2
622A3	1	L6X4X5/8	3'-7 11/16"	73	SHOP_PRIMER A572-GR 50
622A4	1	PERIMETER ANGLE			SQ-2
622A4	1	L6X4X5/8	4'-3"	85	SHOP_PRIMER A572-GR 50
622A5	1	PERIMETER ANGLE			SQ-2
622A5	1	L6X3-1/2X3/2	2'-11 1/2"	45	SHOP_PRIMER A572-GR 50
		TOTAL WEIGHT THIS DRAWING		596	

--	--	