




2 - PERIMETER ANGLES - 623A1

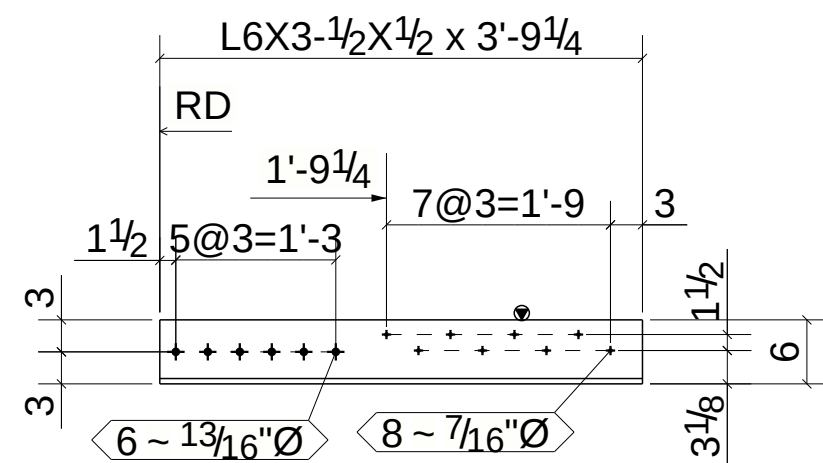


ONE - PERIMETER ANGLE - 623A2

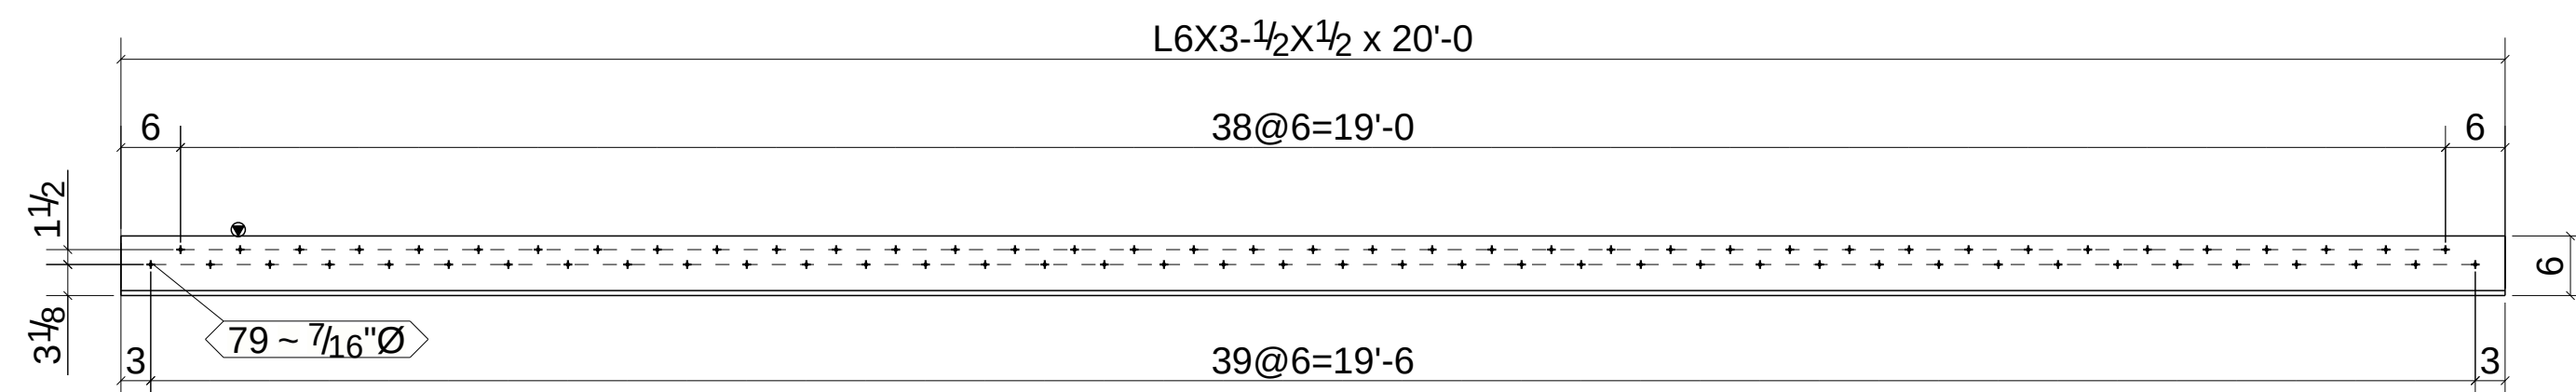

3 - PERIMETER ANGLES - 623A3

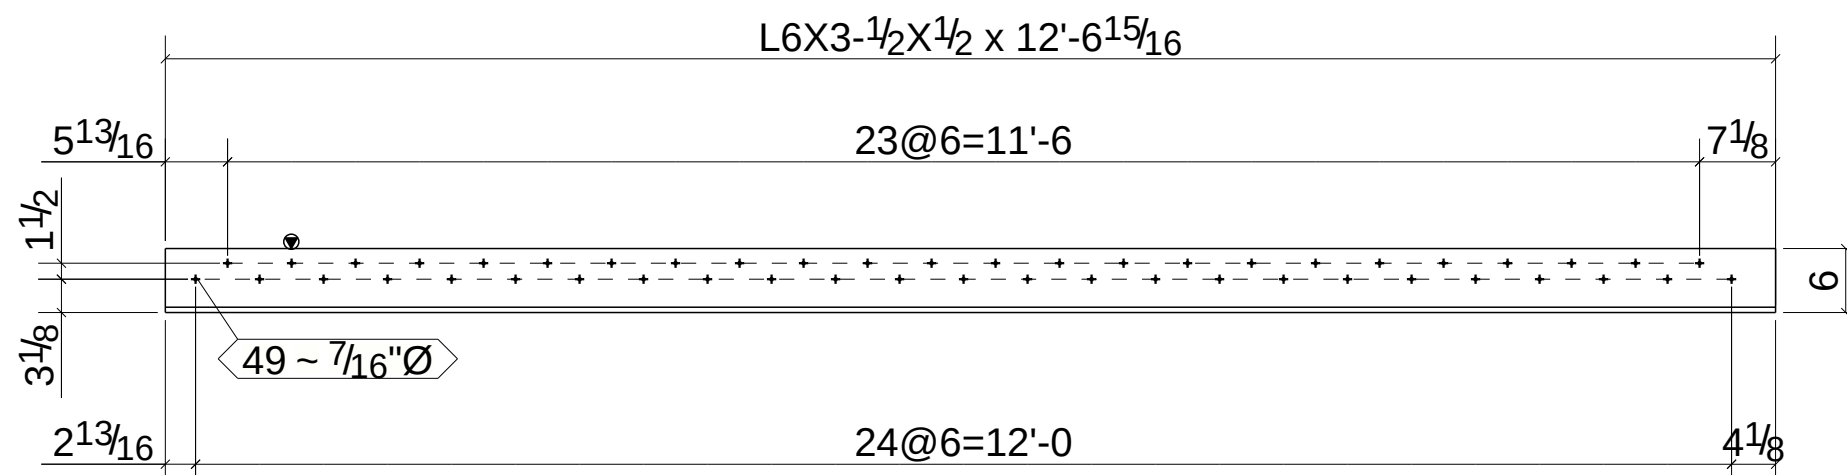

ONE - PERIMETER ANGLE - 623A4

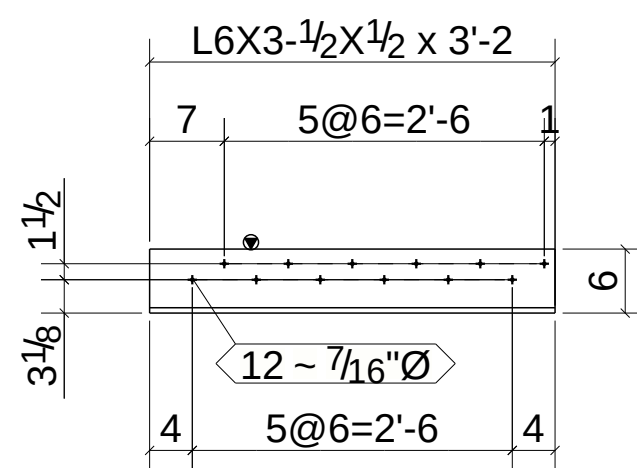

ONE - PERIMETER ANGLE - 623A5

BILL OF MATERIAL						
MARK	QTY	DESCRIPTION	LENGTH	WEIGHT	REMARKS	
623A1	2	PERIMETER ANGLES			SQ-2	
623A1	2	L6X3-1/2X5/16	20'-0"	393	SHOP_PRIMER	A572-GR.50
623A2	1	PERIMETER ANGLE			SQ-2	
623A2	1	L6X3-1/2X1/2	3'-9 1/4"	58	SHOP_PRIMER	A572-GR.50
623A3	3	PERIMETER ANGLES			SQ-2	
623A3	3	L6X3-1/2X1/2	20'-0"	919	SHOP_PRIMER	A572-GR.50
623A4	1	PERIMETER ANGLE			SQ-2	
623A4	1	L6X3-1/2X1/2	12'-6 15/16"	193	SHOP_PRIMER	A572-GR.50
623A5	1	PERIMETER ANGLE			SQ-2	
623A5	1	L6X3-1/2X1/2	3'-2"	49	SHOP_PRIMER	A572-GR.50
		TOTAL WEIGHT THIS DRAWING			1611	

--	--	