




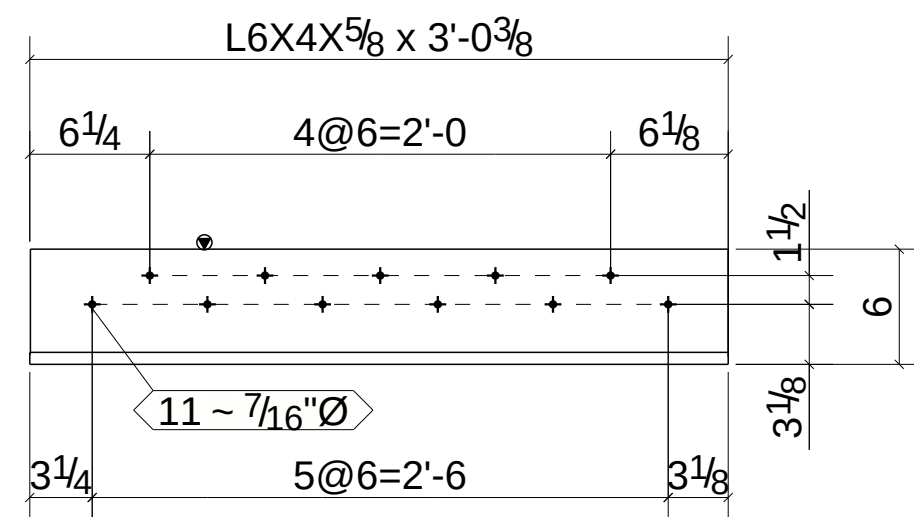


ONE - PERIMETER ANGLE - 624A1

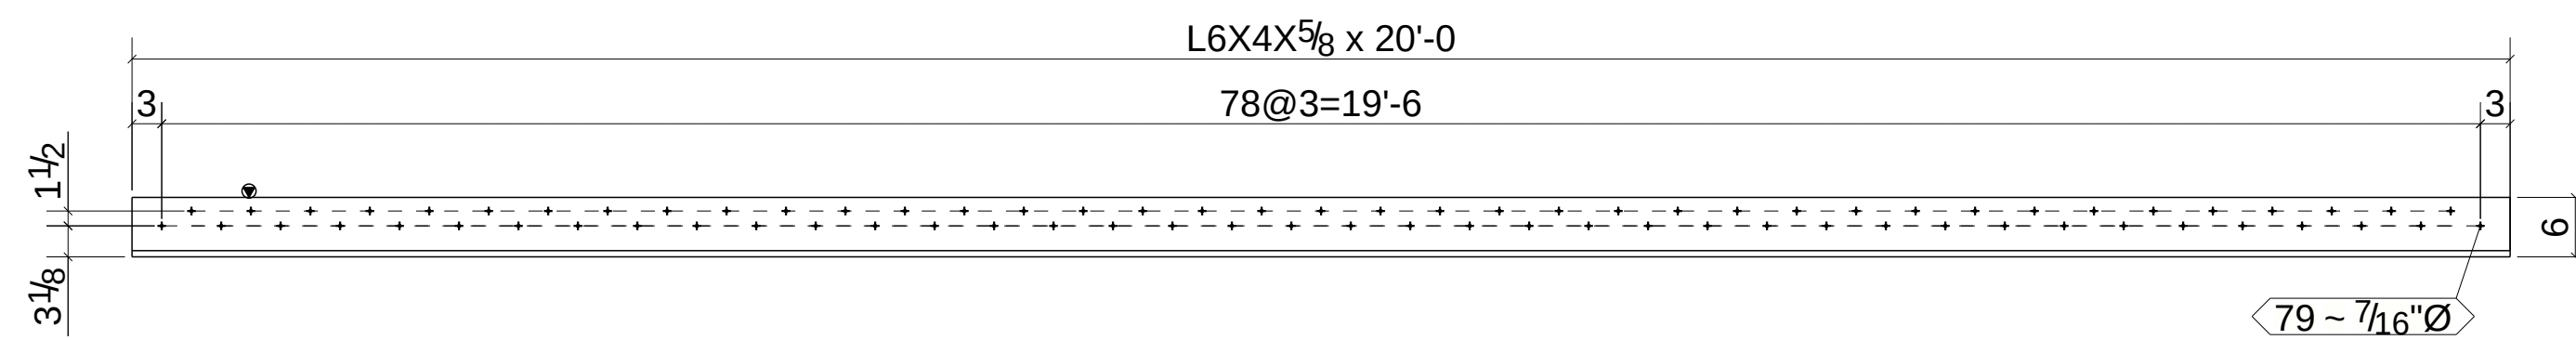


ONE - PERIMETER ANGLE - 624A2

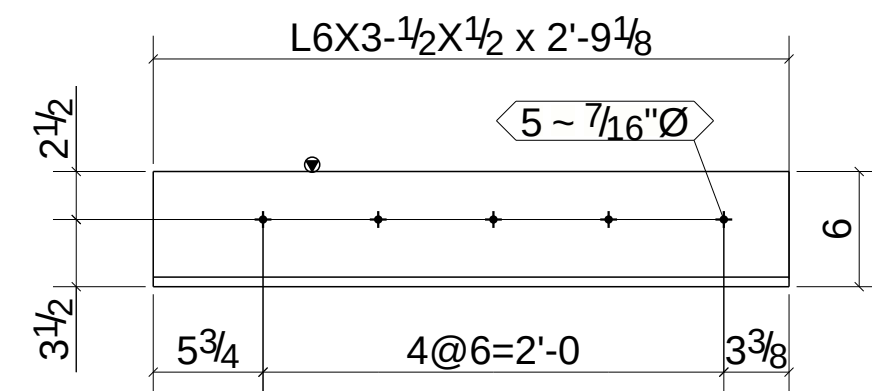


ONE - PERIMETER ANGLE - 624A3

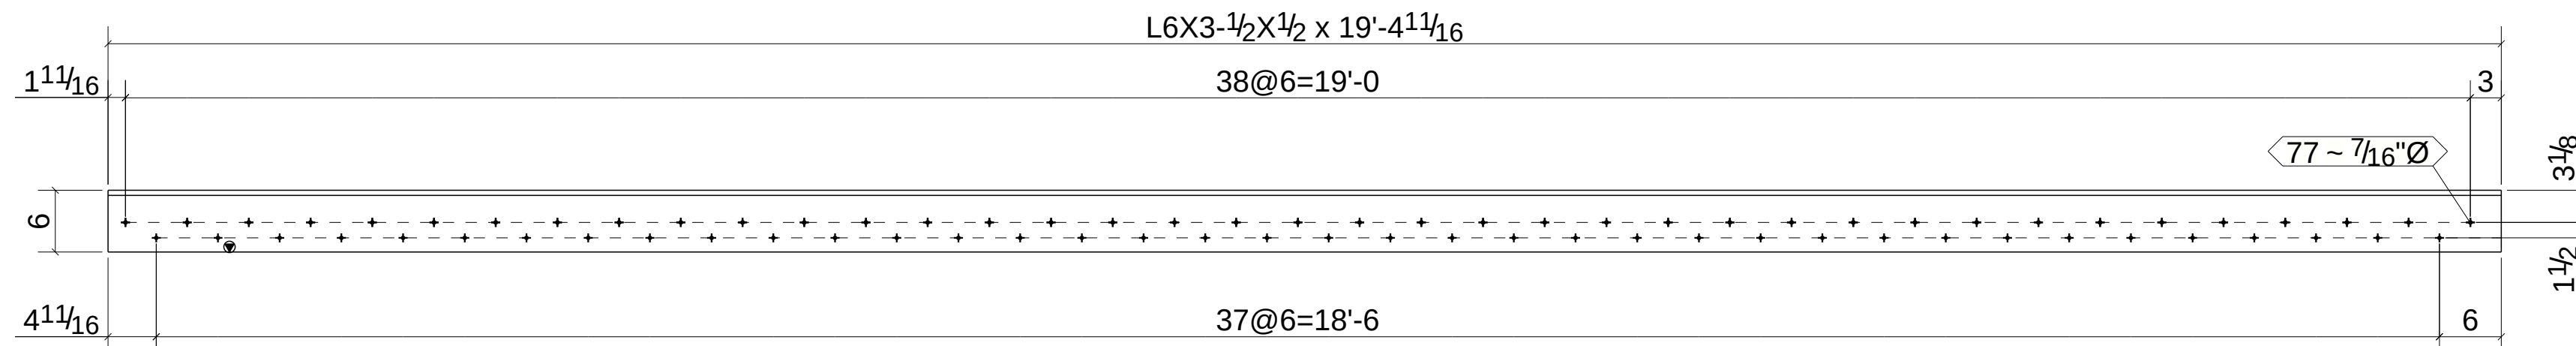


ONE - PERIMETER ANGLE - 624A4

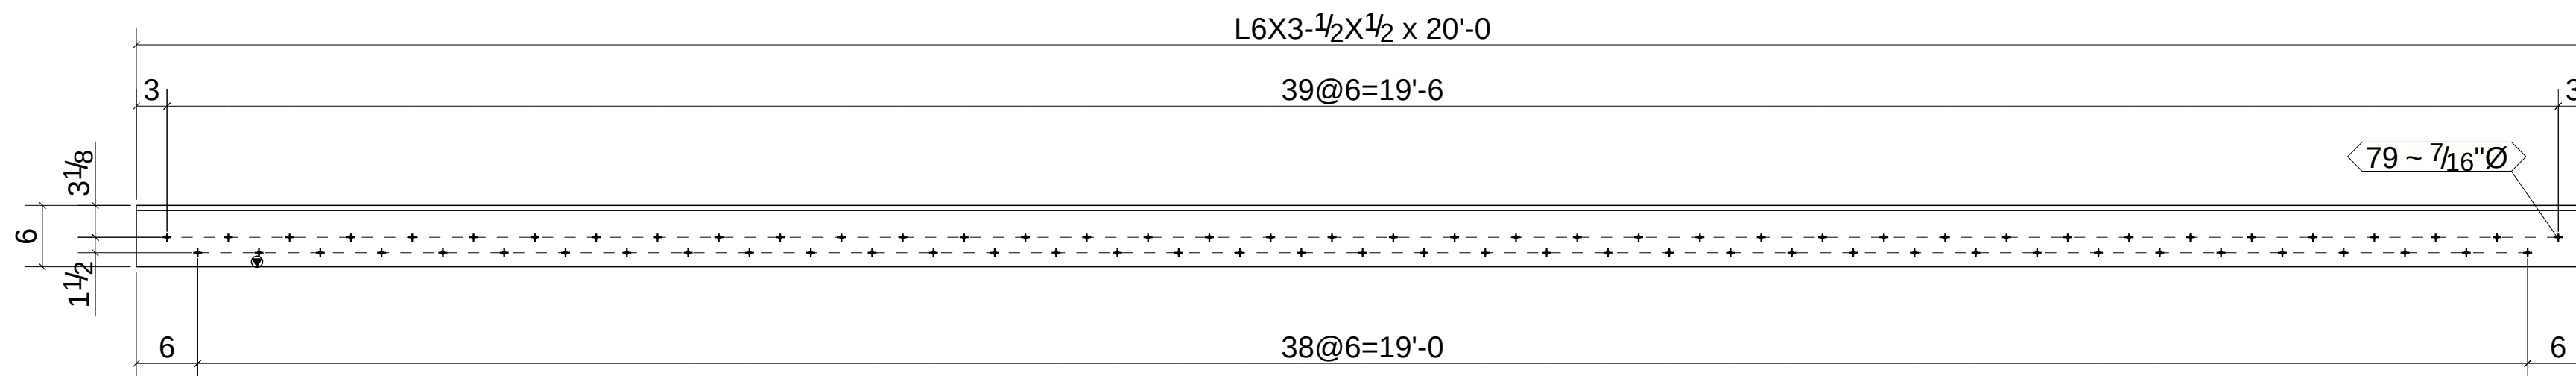

2 - PERIMETER ANGLES - 624A5

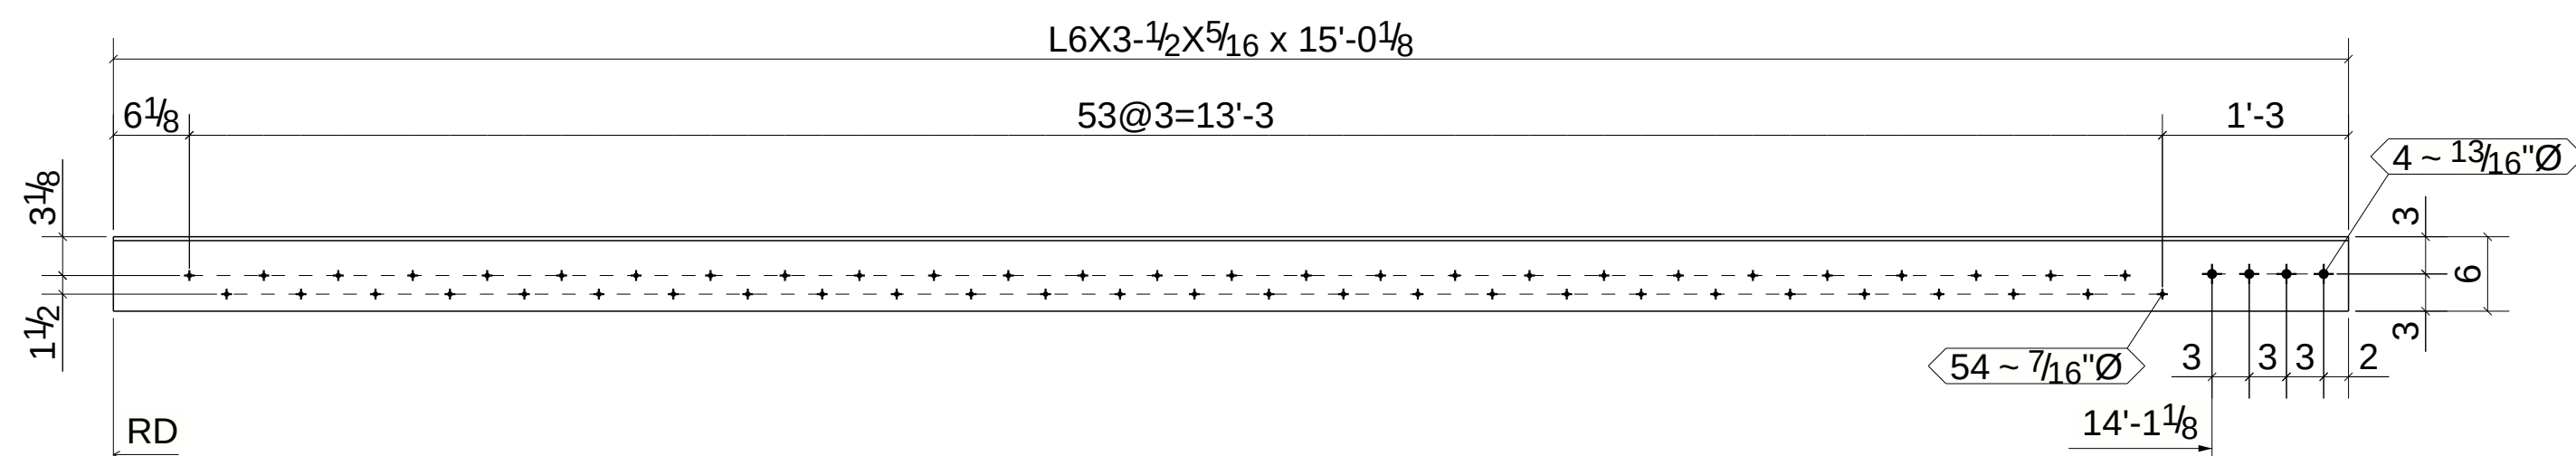


ONE - PERIMETER ANGLE - 624A6

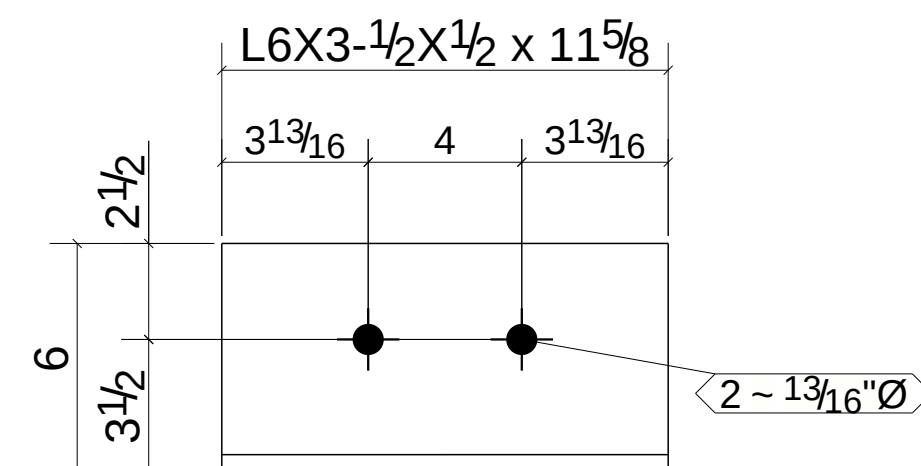

ONE - PERIMETER ANGLE - 624A7

BILL OF MATERIAL					
MARK	QTY	DESCRIPTION	LENGTH	WEIGHT	REMARKS
624A1	1	PERIMETER ANGLE			SQ-2
624A1	1	L6X4X5/8	3'-0 3/8"	60	SHOP_PRIMER A572-GR 50
624A2	1	PERIMETER ANGLE			SQ-2
624A2	1	L6X4X5/8	20'-0"	399	SHOP_PRIMER A572-GR 50
624A3	1	PERIMETER ANGLE			SQ-2
624A3	1	L6X3-1/2X1/2	2'-9 1/8"	42	SHOP_PRIMER A572-GR 50
624A4	1	PERIMETER ANGLE			SQ-2
624A4	1	L6X3-1/2X1/2	19'-4 11/16"	297	SHOP_PRIMER A572-GR 50
624A5	2	PERIMETER ANGLES			SQ-2
624A5	2	L6X3-1/2X1/2	20'-0"	613	SHOP_PRIMER A572-GR 50
624A6	1	PERIMETER ANGLE			SQ-2
624A6	1	L6X3-1/2X5/16	15'-0 1/8"	148	SHOP_PRIMER A572-GR 50
624A7	1	PERIMETER ANGLE			SQ-2
624A7	1	L6X3-1/2X1/2	0'-11 5/8"	15	SHOP_PRIMER A572-GR 50
		TOTAL WEIGHT THIS DRAWING		1574	

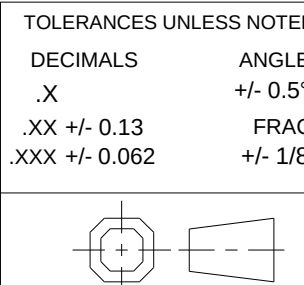[illegible]

Miguel Hidalgo,
Mexico City

CUSTOMER INFORMATION

1523 HARRISON ST.
1523 HARRISON ST., OAKLAND, CA 94612

DRAWING NUMBER

REVISION

624

0

REF.:		DOC. OWNER:		
PROJECT NO. 5220	PART/MATERIAL NO. ANGLE	SCALE 1:12	SIZE D	SHEET 1 OF 1

D

C

B

A

Tekla Structures