


BILL OF MATERIAL					
MARK	QTY	DESCRIPTION	LENGTH	WEIGHT	REMARKS
629C1	2	POSTS			SQ-2
629C1	2	HSS4X4X1/4	6'-6 3/4"	151	GALVANIZED A500-GR.B
a287	8	L4X3X3/8	0'-4"	23	A572-GR.50
p56	2	PL3/8"x12"	1'-0"	31	A572-GR.50
p58	2	PL3/8"x4 1/4"	0'-4 1/4"	4	A572-GR.50
p262	2	PL3/8"x4"	0'-4"	3	A572-GR.50
629C2	1	POST			SQ-2
629C2	1	HSS4X4X1/4	6'-6 3/4"	75	GALVANIZED A500-GR.B
a286	2	L4X3X3/8	0'-4"	6	A572-GR.50
a287	3	L4X3X3/8	0'-4"	8	A572-GR.50
a288	1	L4X3X3/8	0'-4"	3	A572-GR.50
p56	1	PL3/8"x12"	1'-0"	15	A572-GR.50
p262	1	PL3/8"x4"	0'-4"	2	A572-GR.50
TOTAL WEIGHT THIS DRAWING				320	

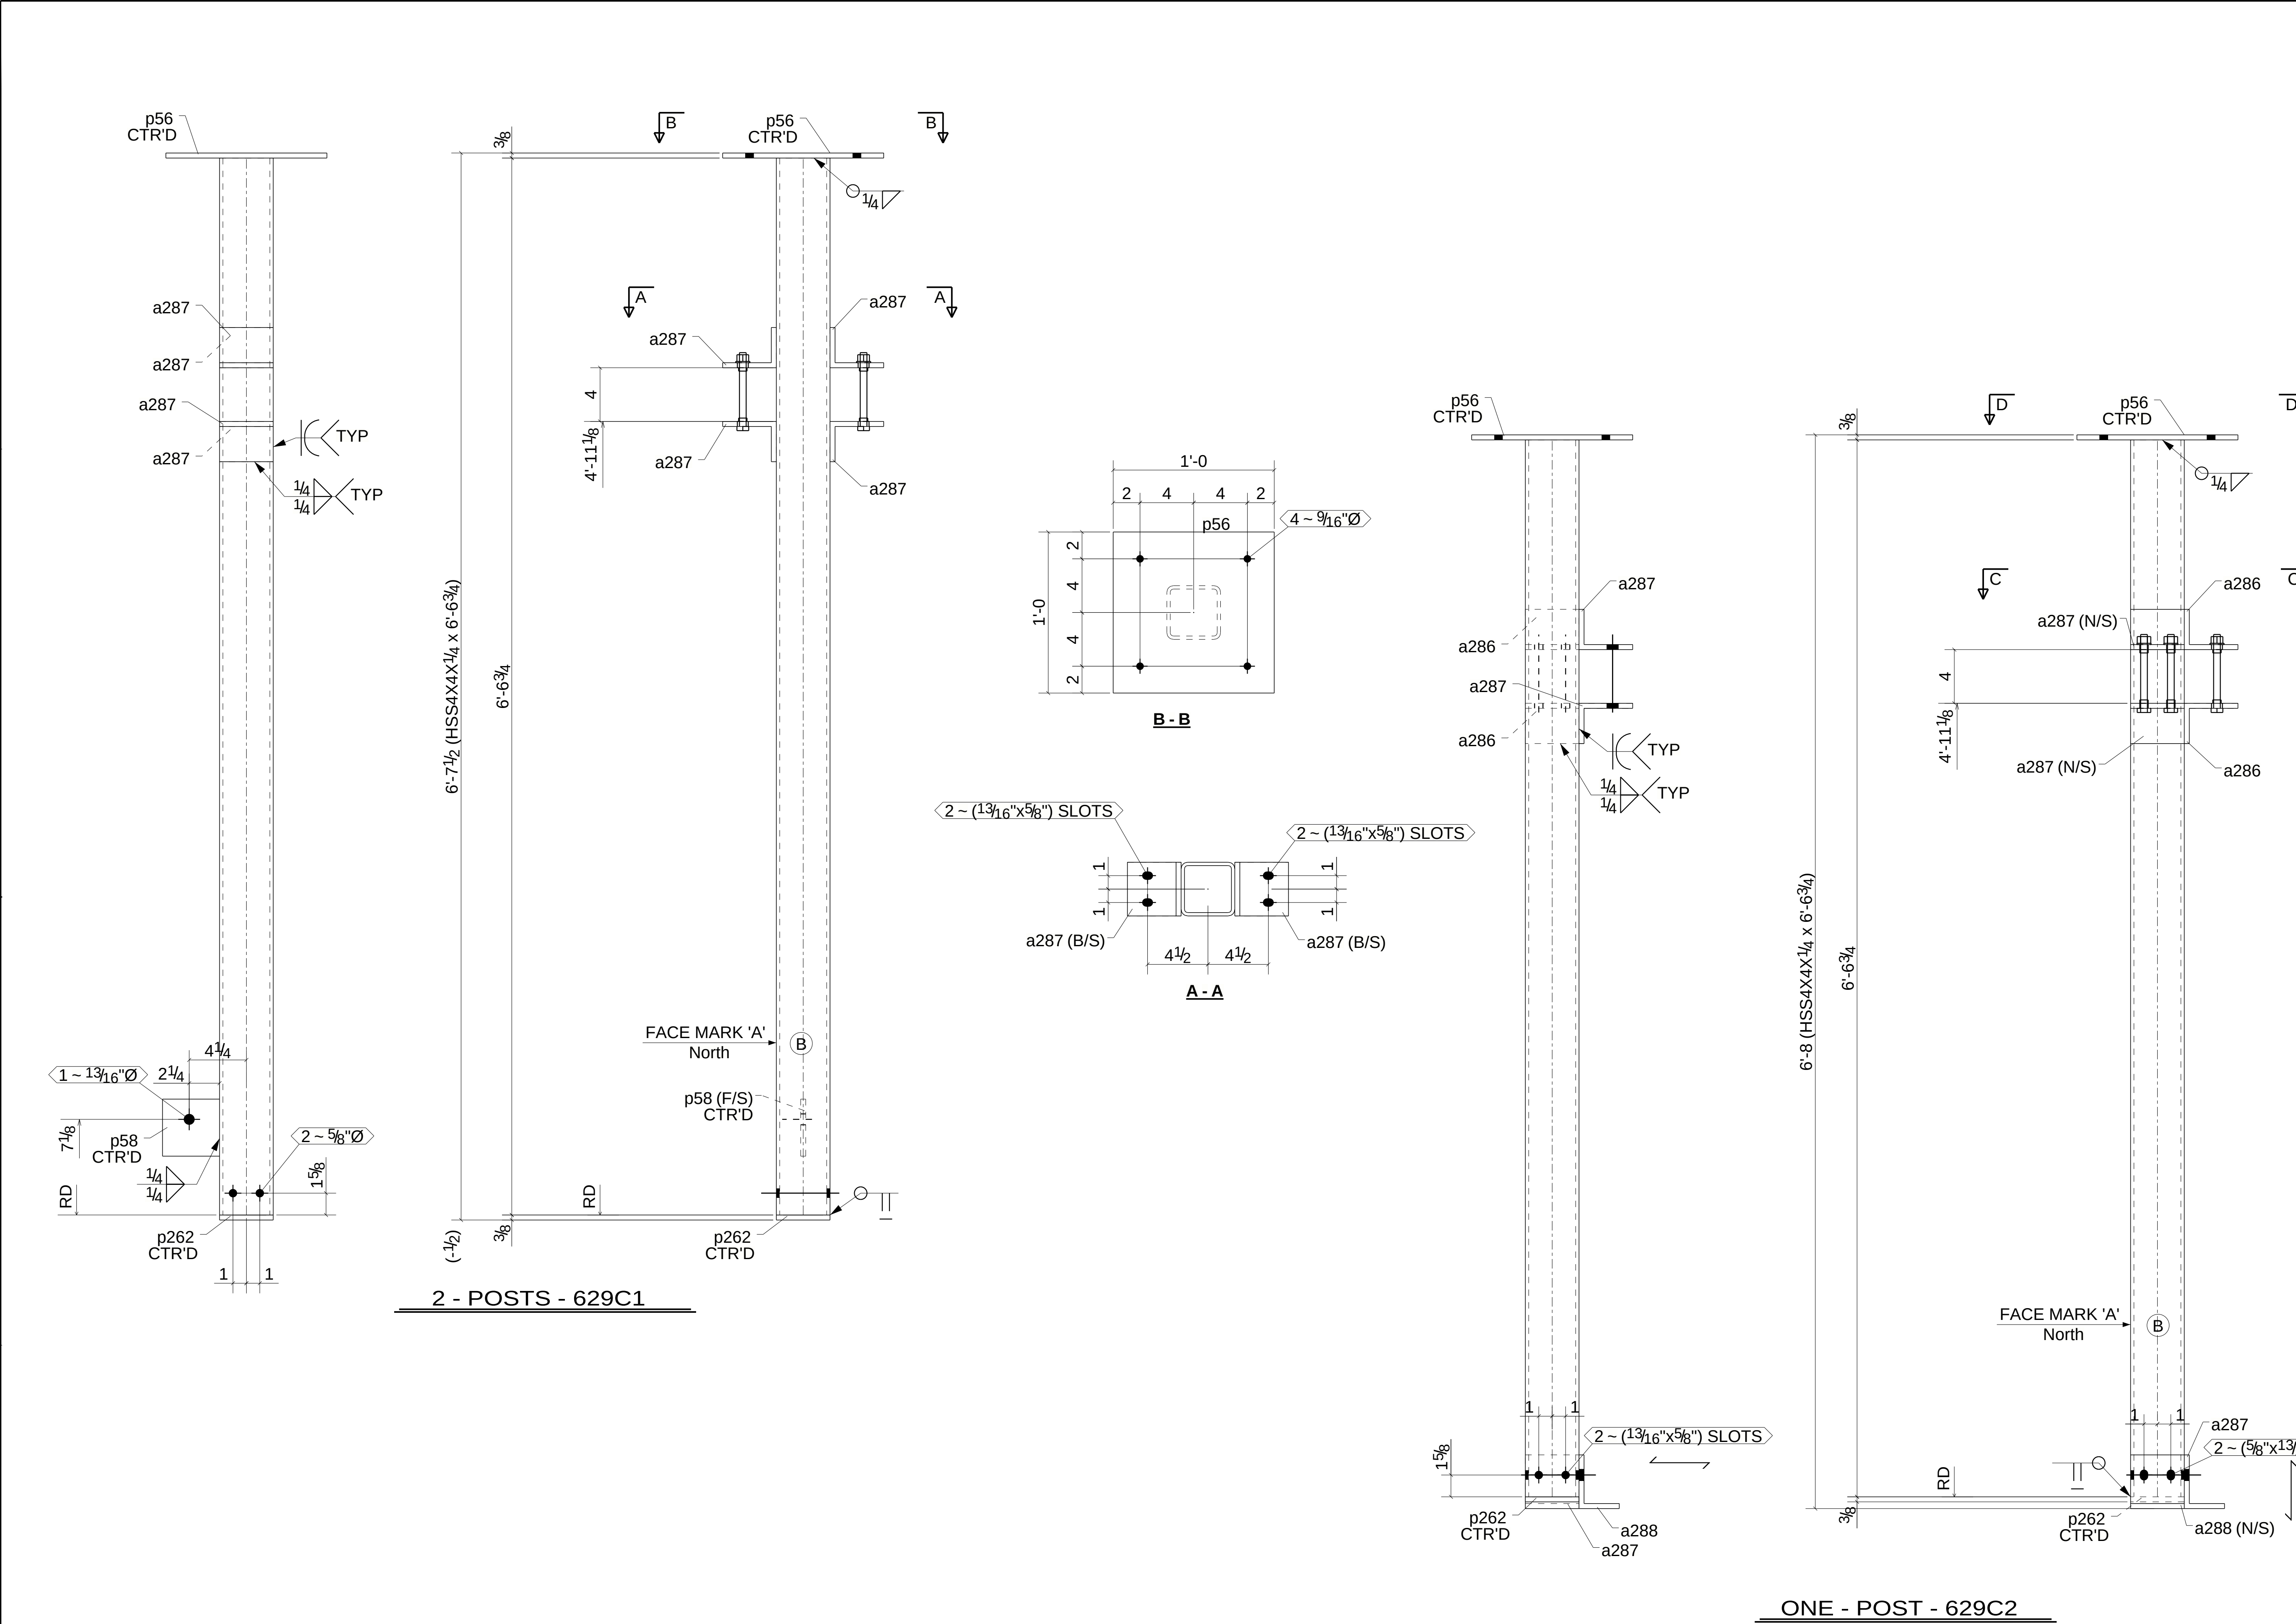

DRAWING NUMBER										REVISION		
629										0		
REF.:					DOC. OWNER:							
PROJECT NO. 5220					PART/MATERIAL NO. POST					SCALE 1:12	SIZE D	SHEET 1 OF 1

0	ISSUED FOR FABRICATION	ECO	DWN	APPR	APPR	DATE 06/09/2026	TOLERANCES UNLESS NOTED DECIMALS .XX +/- 0.13 XXX +/- 0.062 ANGLES +/- 0.5° FRAC +/- 1/8"		Miguel Hidalgo, Mexico City	CUSTOMER INFORMATION			1523 HARRISON ST. 1523 HARRISON ST., OAKLAND, CA 94612		
---	------------------------	-----	-----	------	------	--------------------	--	--	--------------------------------	----------------------	--	--	---	--	--

PROPRIETARY AND CONFIDENTIAL: THIS DRAWING AND ALL INFORMATION AND KNOWLEDGE CONTAINED OR REFERRED HEREIN ARE THE CONFIDENTIAL AND PROPRIETARY PROPERTY OF PRIMA AND AS SUCH ARE INSTRUMENTS OF SERVICE FOR USE SOLELY WITH RESPECT TO THIS PROJECT. THESE INSTRUMENTS OF SERVICE SHALL NOT BE REPRODUCED, TRANSMITTED, DISCLOSED OR USED OTHERWISE IN WHOLE OR IN PART, WITHOUT PRIOR WRITTEN AGREEMENT BY PRIMA AND MUST BE IMMEDIATELY RETURNED OR DESTROYED UPON REQUEST.