
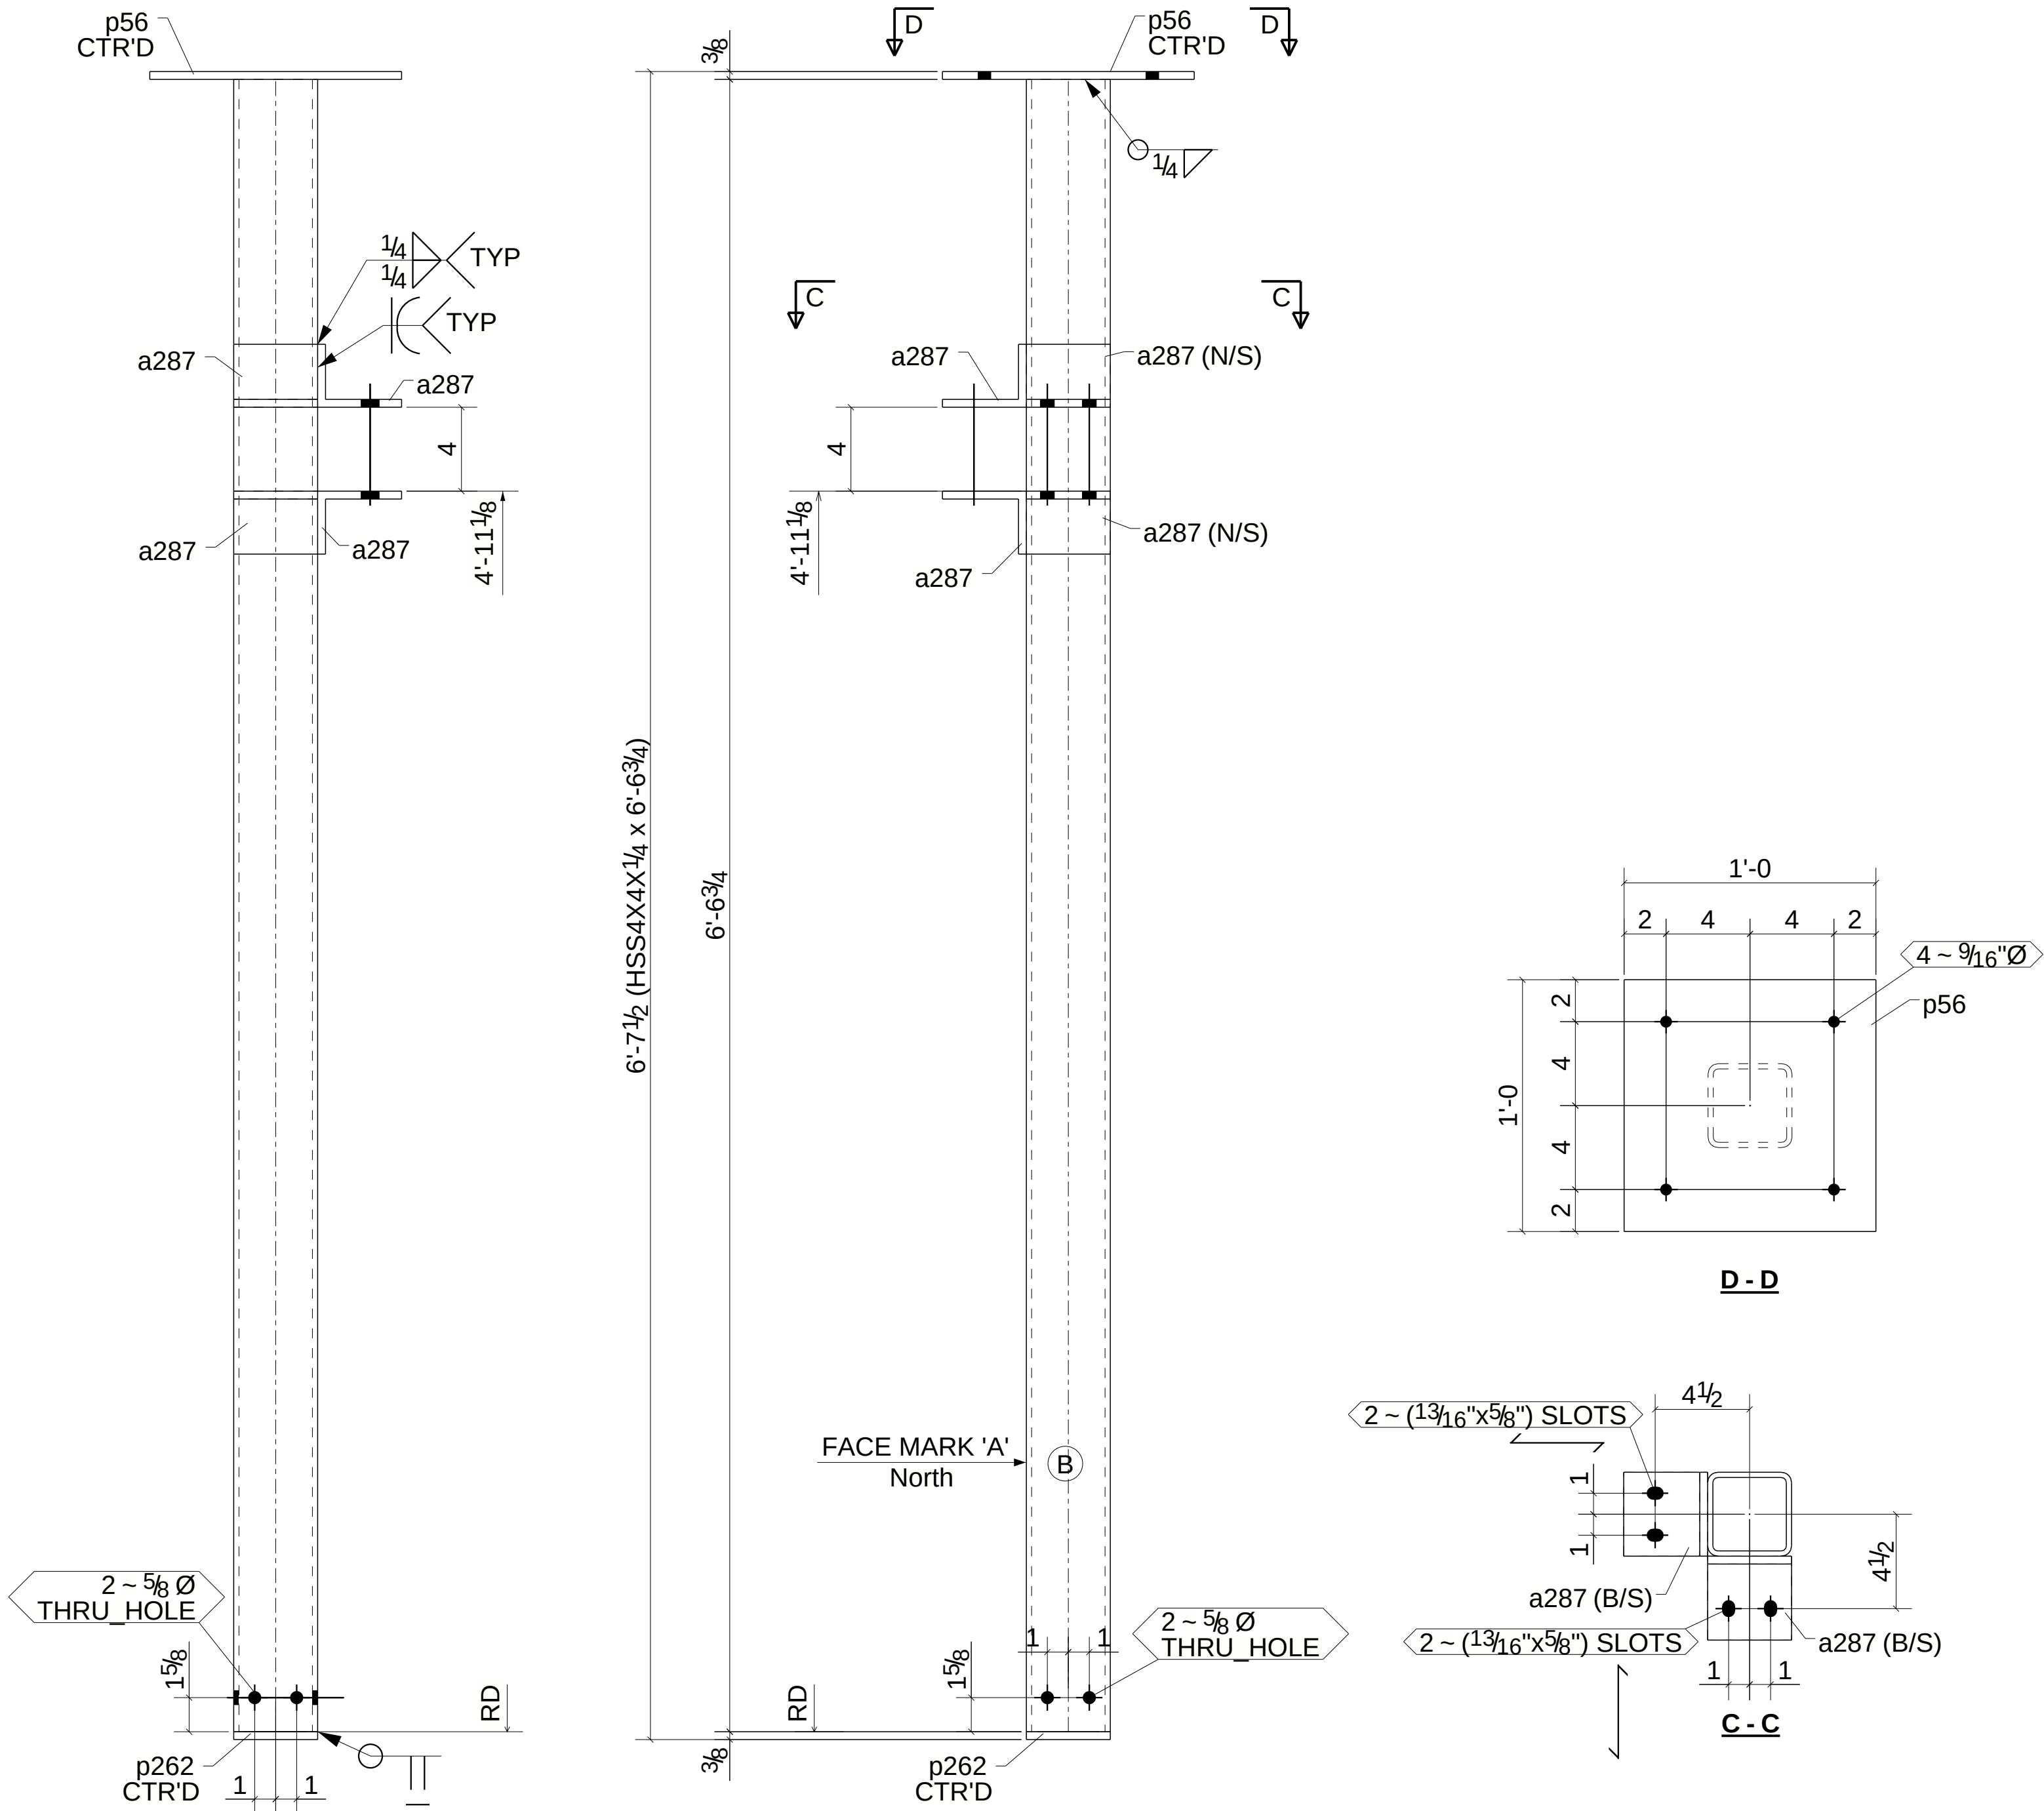


BILL OF MATERIAL					
MARK	QTY	DESCRIPTION	LENGTH	WEIGHT	REMARKS
636C1	1	POST			SQ-2
636C1	1	HSS4X4X1/4	6'-6 3/4"	75	GALVANIZED A500-GR.B
a287	2	L4X3X3/8	0'-4"	6	A572-GR.50
p56	1	PL3/8"x12"	1'-0"	15	A572-GR.50
p58	1	PL3/8"x4 1/4"	0'-4 1/4"	2	A572-GR.50
p262	1	PL3/8"x4"	0'-4"	2	A572-GR.50
636C2	1	POST			SQ-2
636C2	1	HSS4X4X1/4	6'-6 3/4"	75	GALVANIZED A500-GR.B
a287	4	L4X3X3/8	0'-4"	11	A572-GR.50
p56	1	PL3/8"x12"	1'-0"	15	A572-GR.50
p262	1	PL3/8"x4"	0'-4"	2	A572-GR.50
TOTAL WEIGHT THIS DRAWING				203	

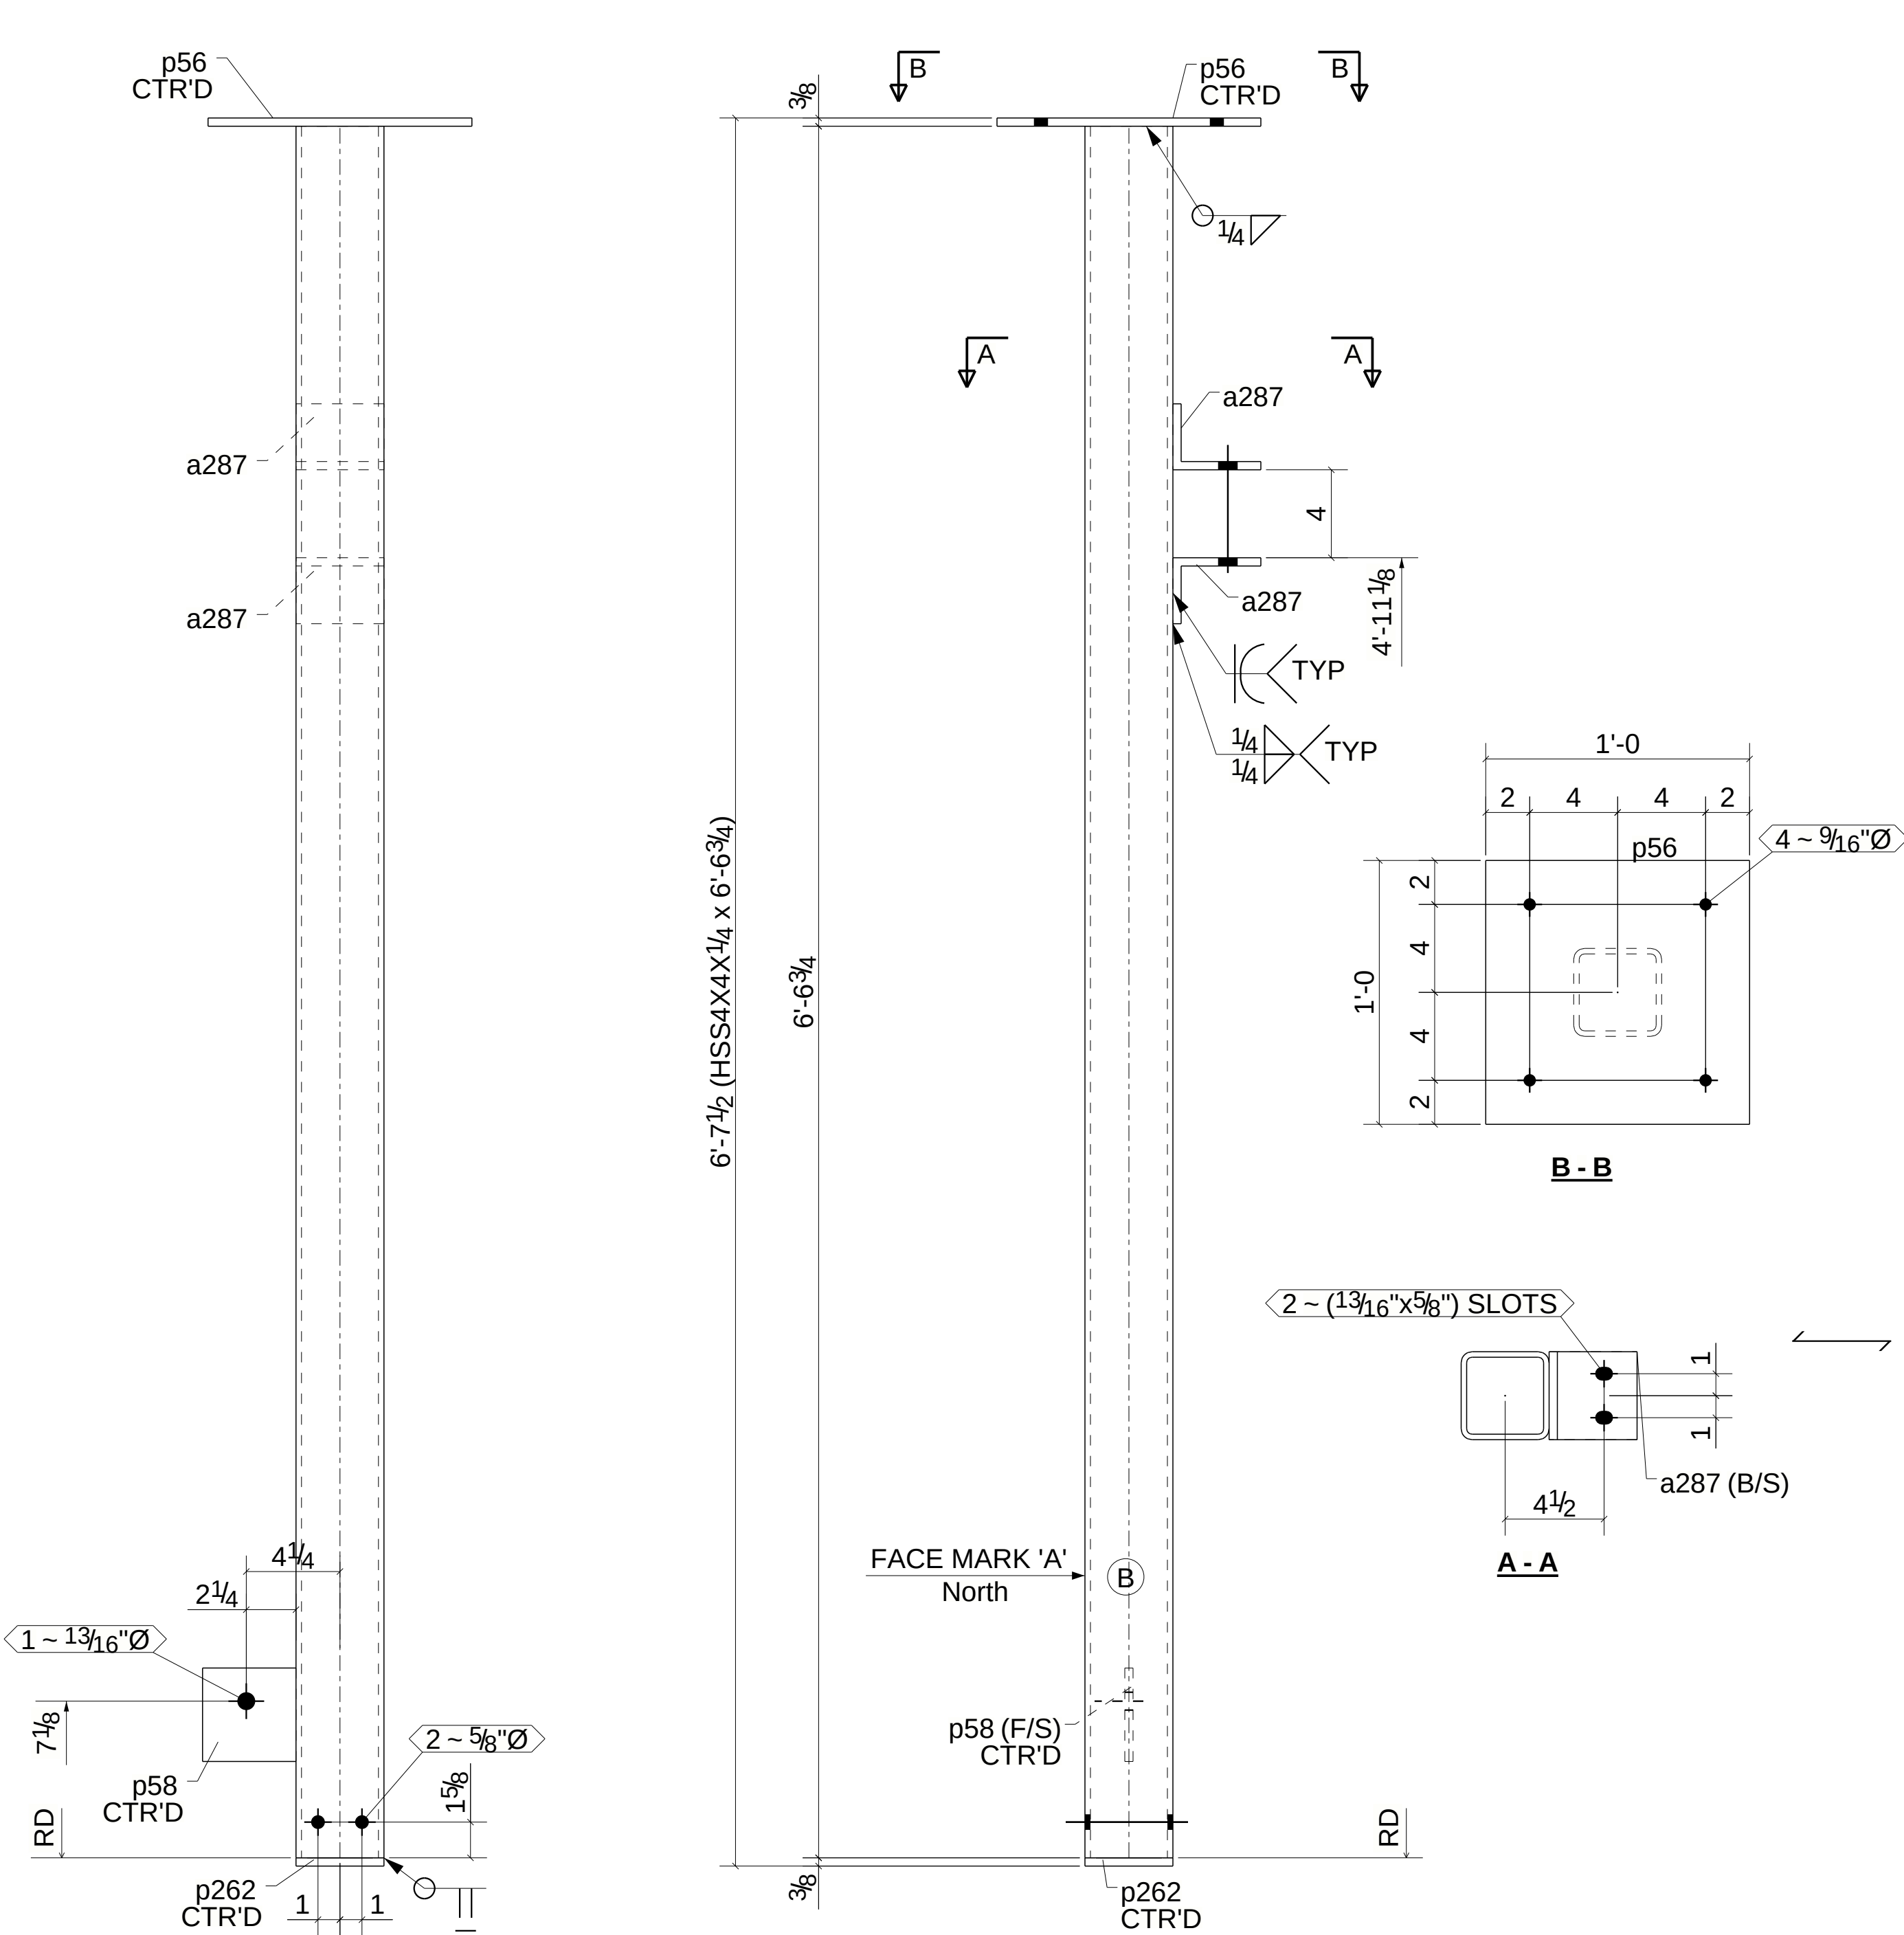

REV	DESCRIPTION	ECO	DWN	APPR	APPR	DATE
0	ISSUED FOR FABRICATION					06/09/2026

PROPRIETARY AND CONFIDENTIAL: THIS DRAWING AND ALL INFORMATION AND KNOWLEDGE CONTAINED OR REFERRED HEREIN ARE THE CONFIDENTIAL AND PROPRIETARY PROPERTY OF PRIMA AND AS SUCH ARE INSTRUMENTS OF SERVICE FOR USE SOLELY WITH RESPECT TO THIS PROJECT. THESE INSTRUMENTS OF SERVICE SHALL NOT BE REPRODUCED, TRANSMITTED, DISCLOSED OR USED OTHERWISE IN WHOLE OR IN PART, WITHOUT PRIOR WRITTEN AGREEMENT BY PRIMA AND MUST BE IMMEDIATELY RETURNED OR DESTROYED UPON REQUEST.

TOLERANCES UNLESS NOTED
DECIMALS .X .XX +/- 0.13 XXX +/- 0.062
ANGLES +/- 0.5° FRAC +/- 1/8"



Miguel Hidalgo,
Mexico City

CUSTOMER INFORMATION

1523 HARRISON ST.
1523 HARRISON ST., OAKLAND, CA 94612

DRAWING NUMBER		REVISION
636		0
REF.:	DOC. OWNER:	
PROJECT NO. 5220	PART/MATERIAL NO. POST	SCALE 1:12
		SHEET D 1 OF 1