




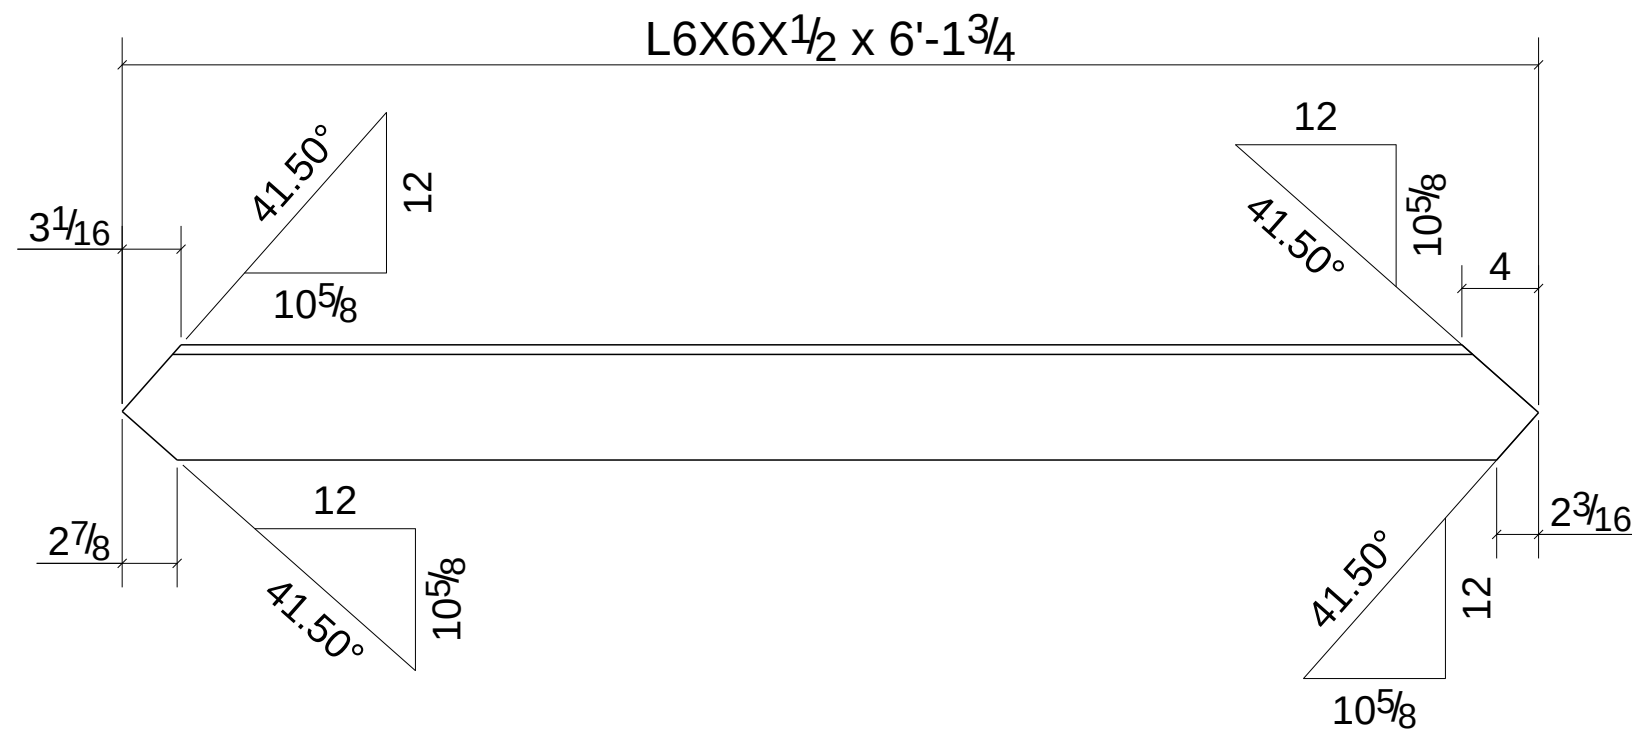


2 - HORIZONTAL BRACES - 640HB1

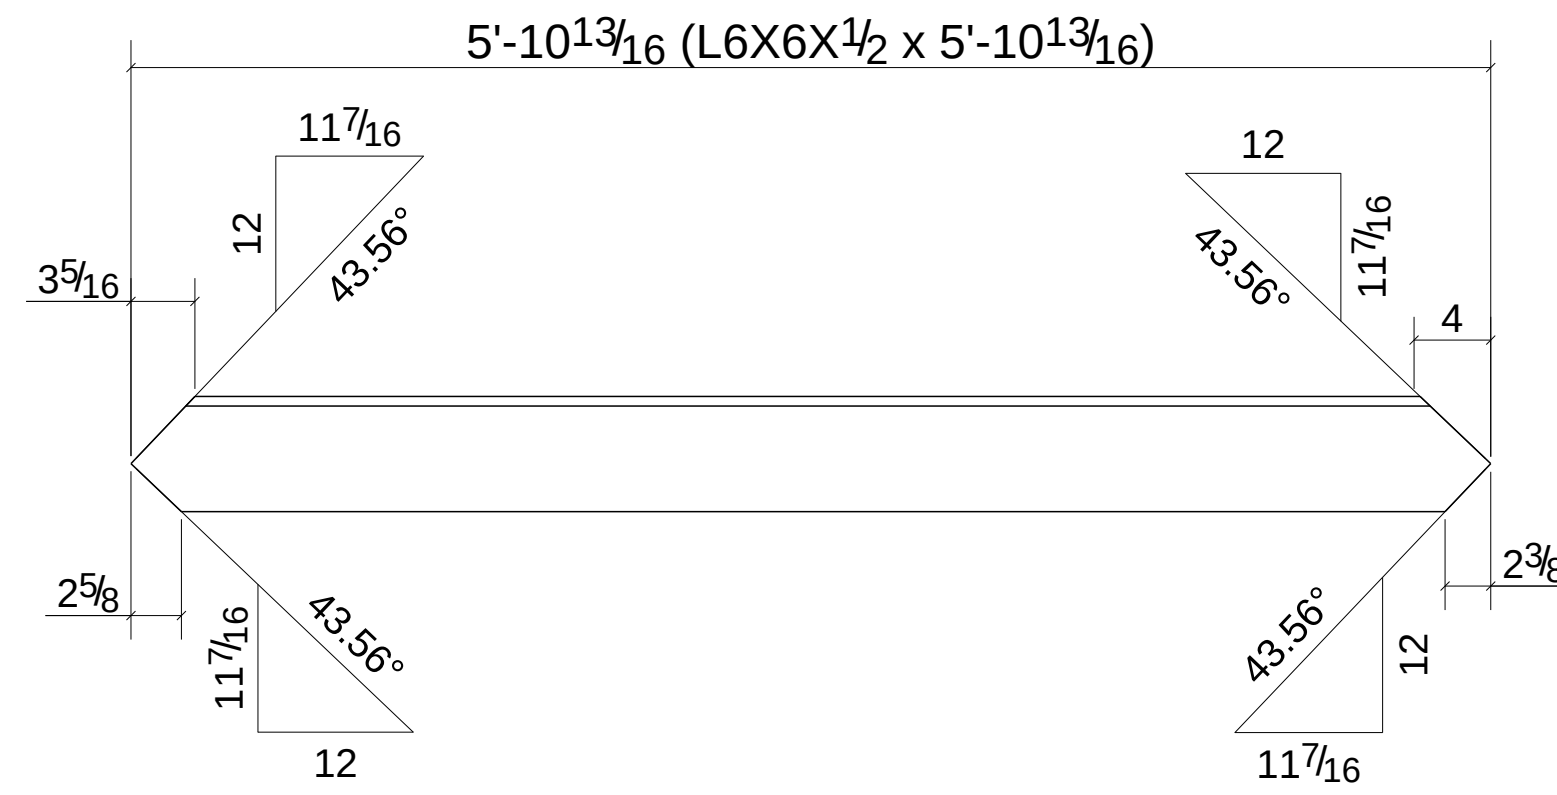


2 - HORIZONTAL BRACES - 640HB2

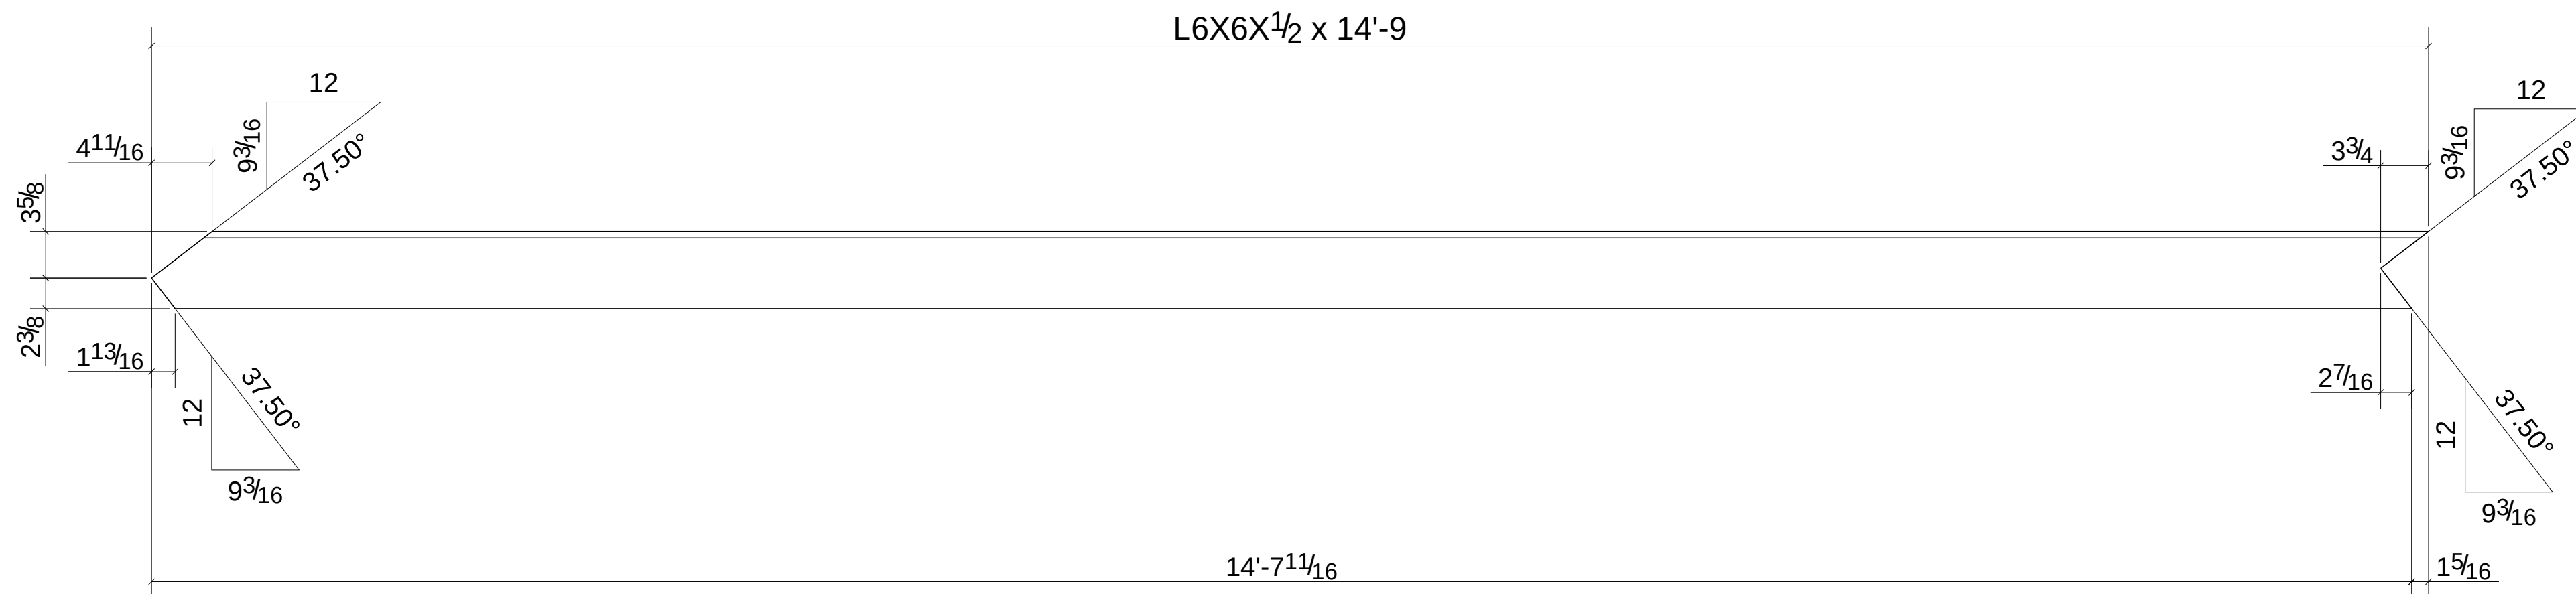

ONE - HORIZONTAL BRACE - 640HB3

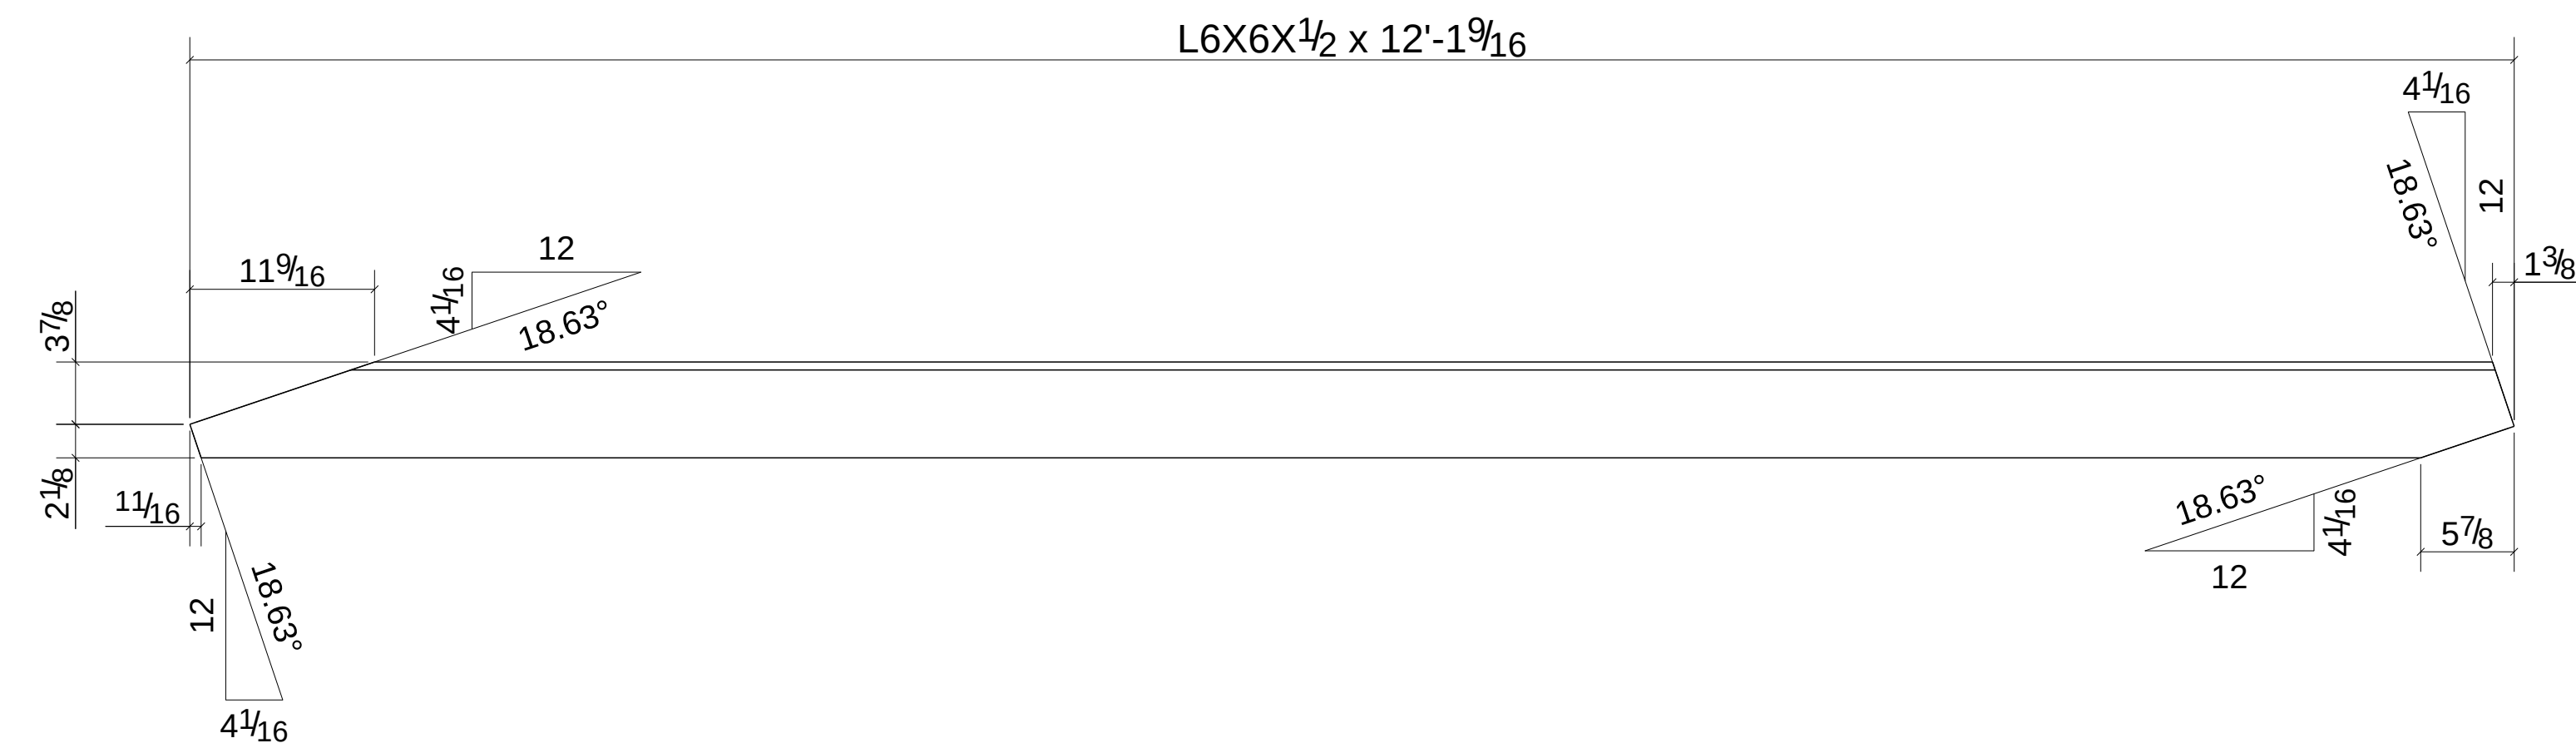


ONE - HORIZONTAL BRACE - 640HB4

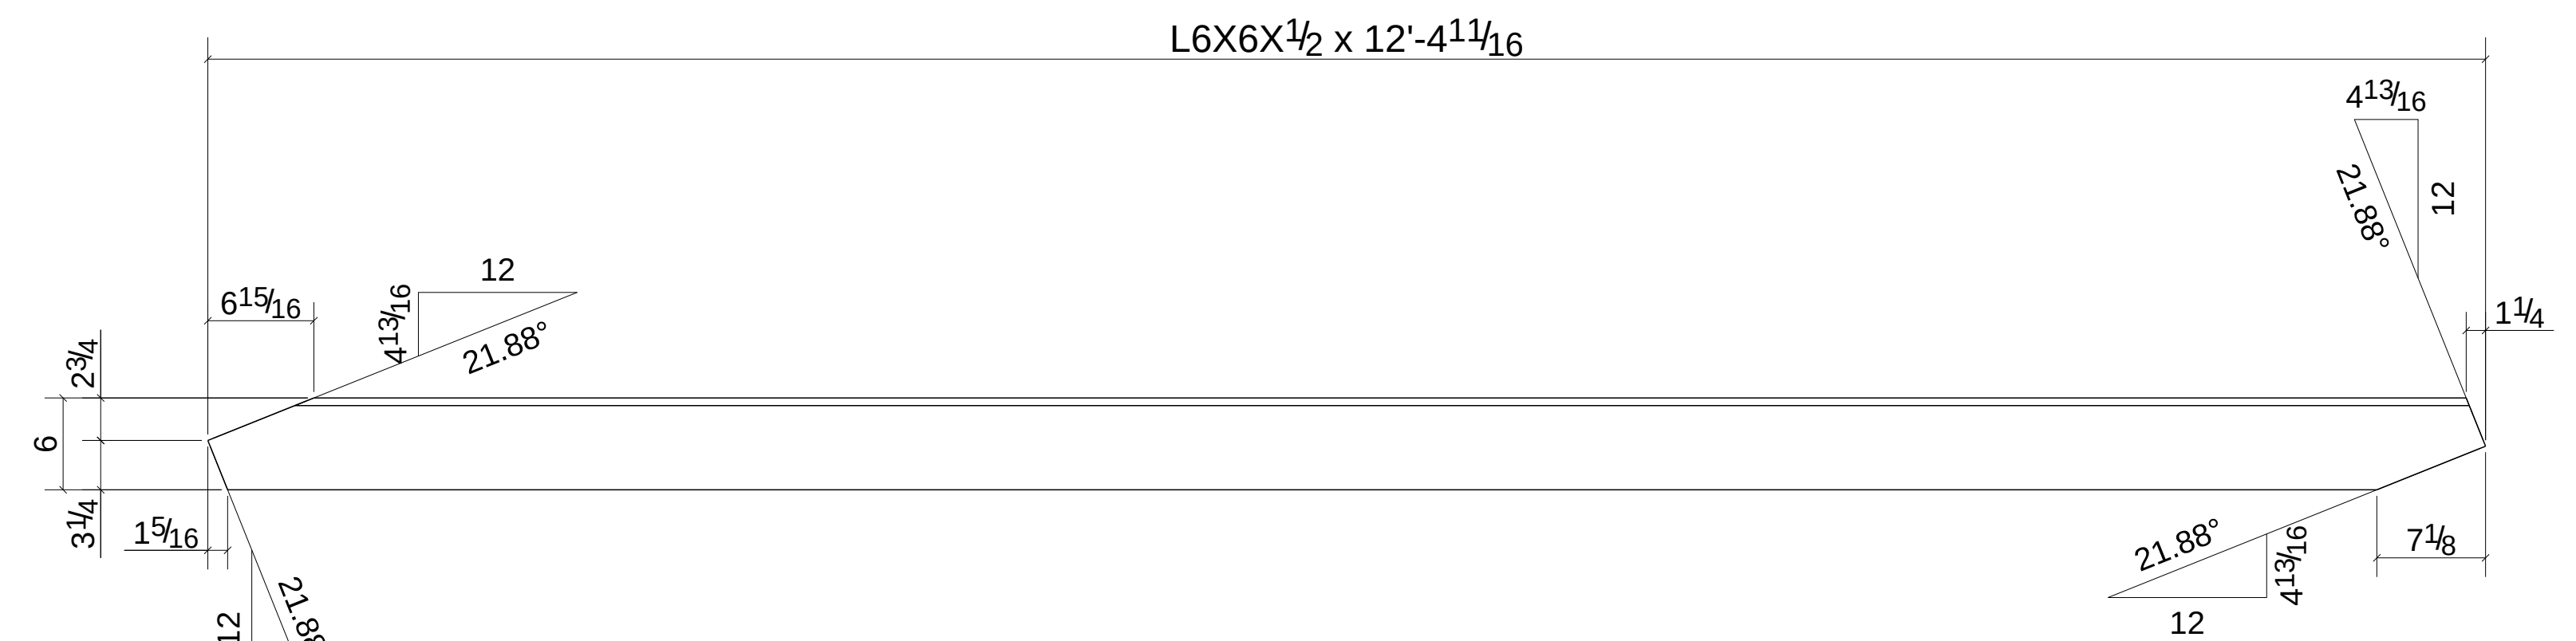

ONE - HORIZONTAL BRACE - 640HB5

BILL OF MATERIAL					
MARK	QTY	DESCRIPTION	LENGTH	WEIGHT	REMARKS
640HB1	2	HORIZONTAL_BRACES			BEV-2
640HB1	2	L6X6X1/2	6'-1 3/4"	241	GALVANIZED A572
640HB2	2	HORIZONTAL_BRACES			BEV-2
640HB2	2	L6X6X1/2	5'-10 13/16"	232	GALVANIZED A572
640HB3	1	HORIZONTAL_BRACE			SQ-1/BEV-1
640HB3	1	L6X6X1/2	14'-9"	290	GALVANIZED A572
640HB4	1	HORIZONTAL_BRACE			BEV-2
640HB4	1	L6X6X1/2	12'-1 9/16"	238	GALVANIZED A572
640HB5	1	HORIZONTAL_BRACE			BEV-2
640HB5	1	L6X6X1/2	12'-4 11/16"	243	SALVANIZED A572
		TOTAL WEIGHT THIS DRAWING		1244	

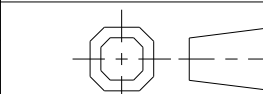[illegible]

TOLERANCES UNLESS NOTED	
DECIMALS	ANGLE
.X	+/- 0.5°
.XX +/- 0.13	FRACTION
.XXX +/- 0.062	+/- 1/8



Miguel Hidalgo,
Mexico City

CUSTOMER INFORMATION

1523 HARRISON ST.
1523 HARRISON ST., OAKLAND, CA 94612

DRAWING NUMBER

REVISION

640

0

REF.:		DOC. OWNER:		
PROJECT NO. 5220	PART/MATERIAL NO. HORIZONTAL BRACE	SCALE 1:12	SIZE D	SHEET 1 OF 1

D

C

B

A

D

C

B

A

Tekla Structures