




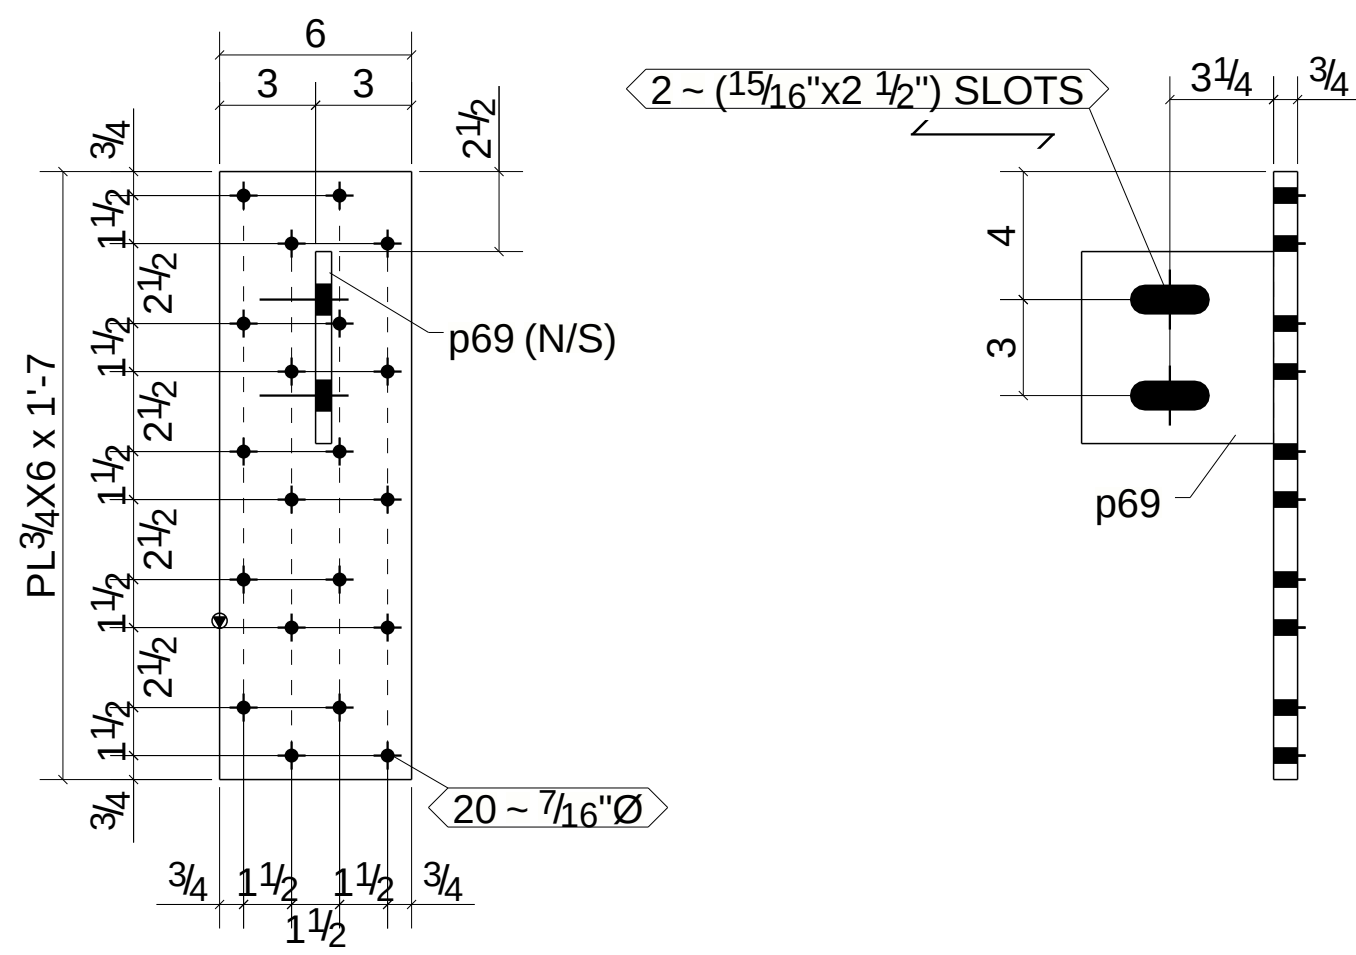



ONE - END PLATE - 643PL1

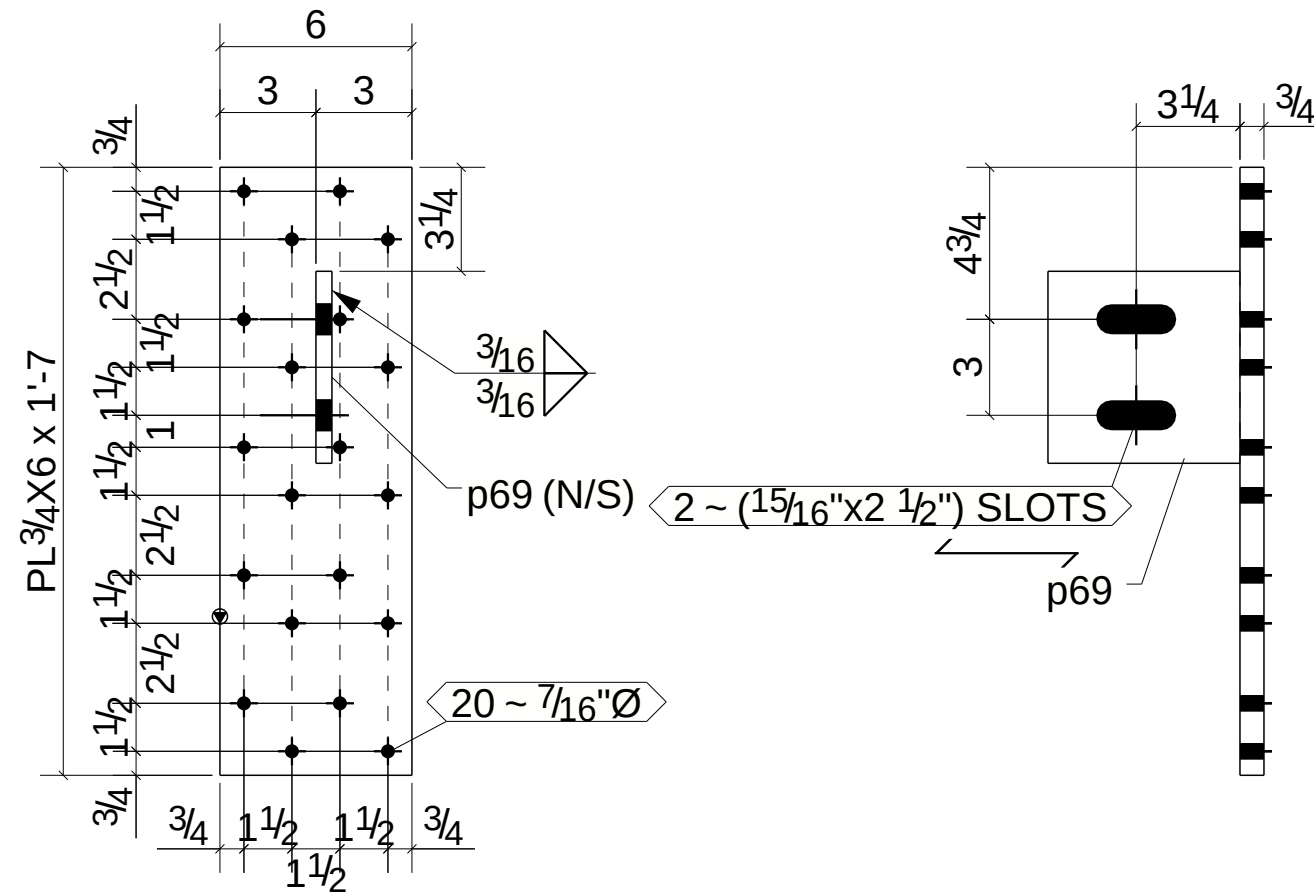


ONE - END PLATE - 643PL2

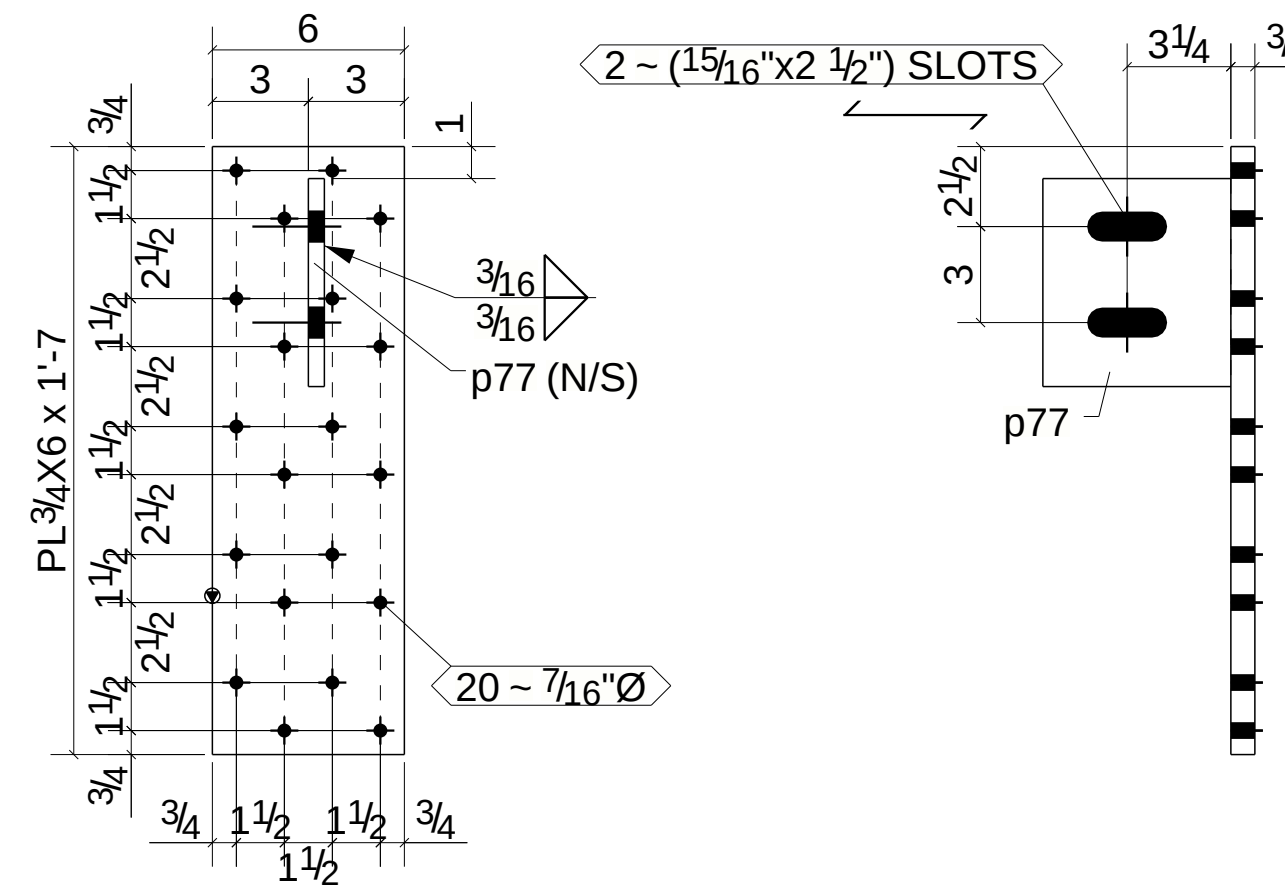


2 - END PLATES - 643PL3

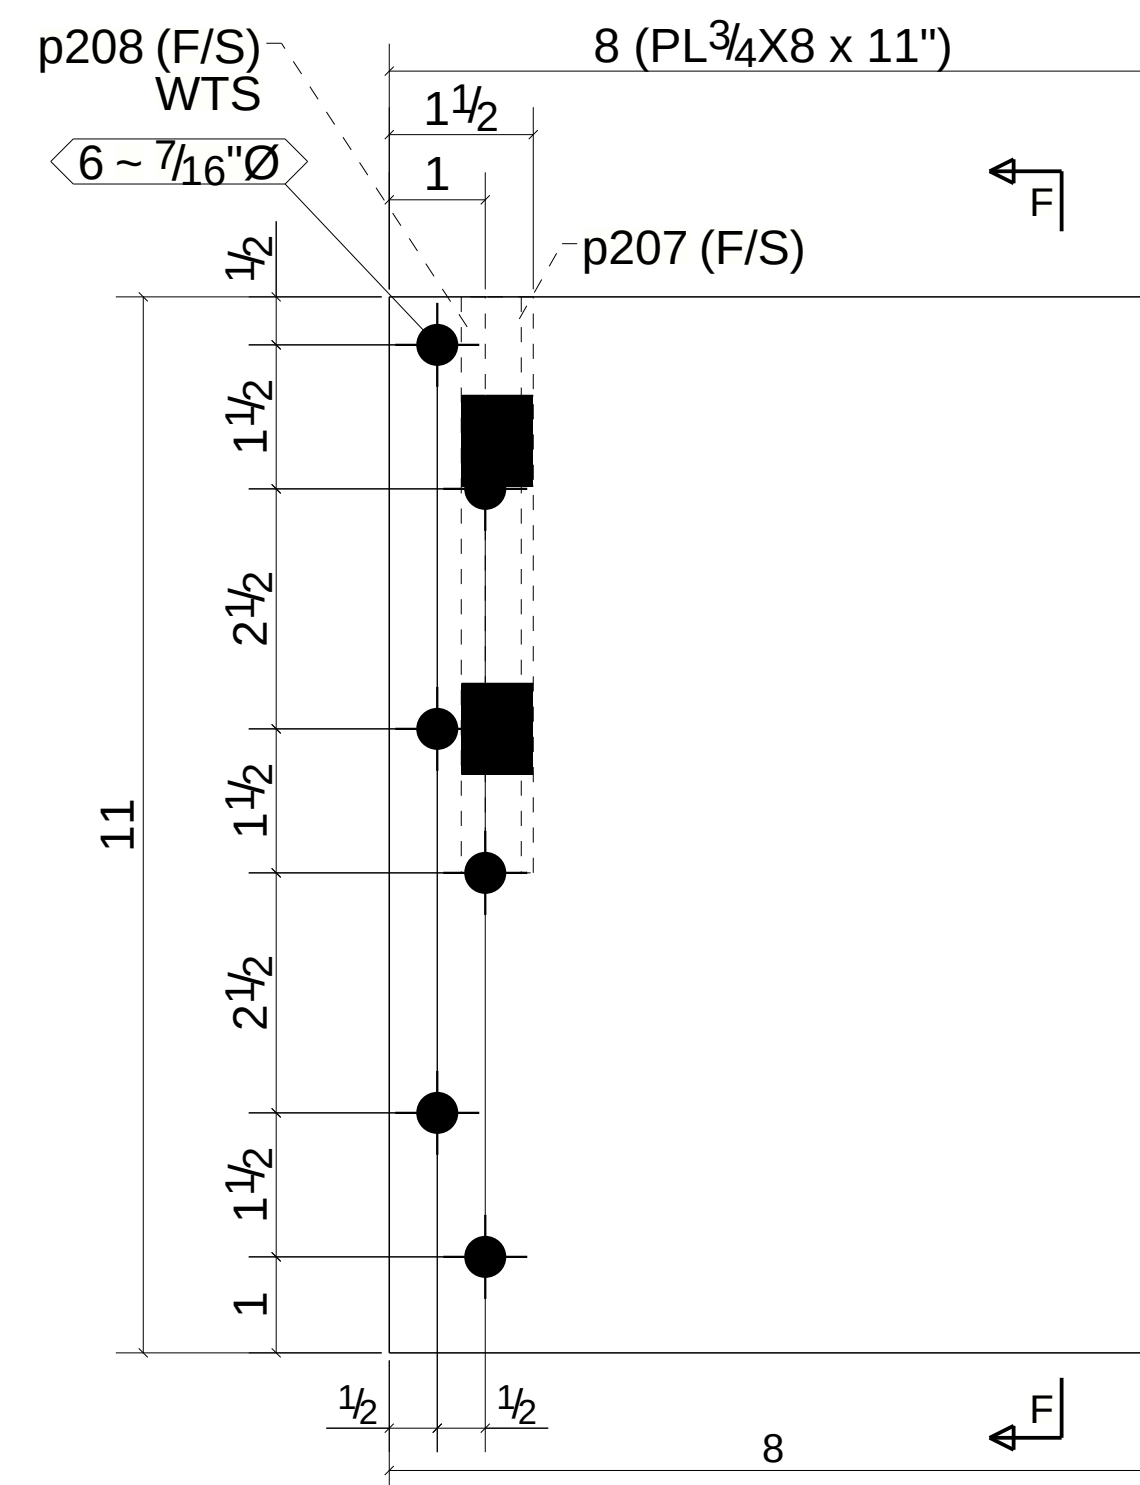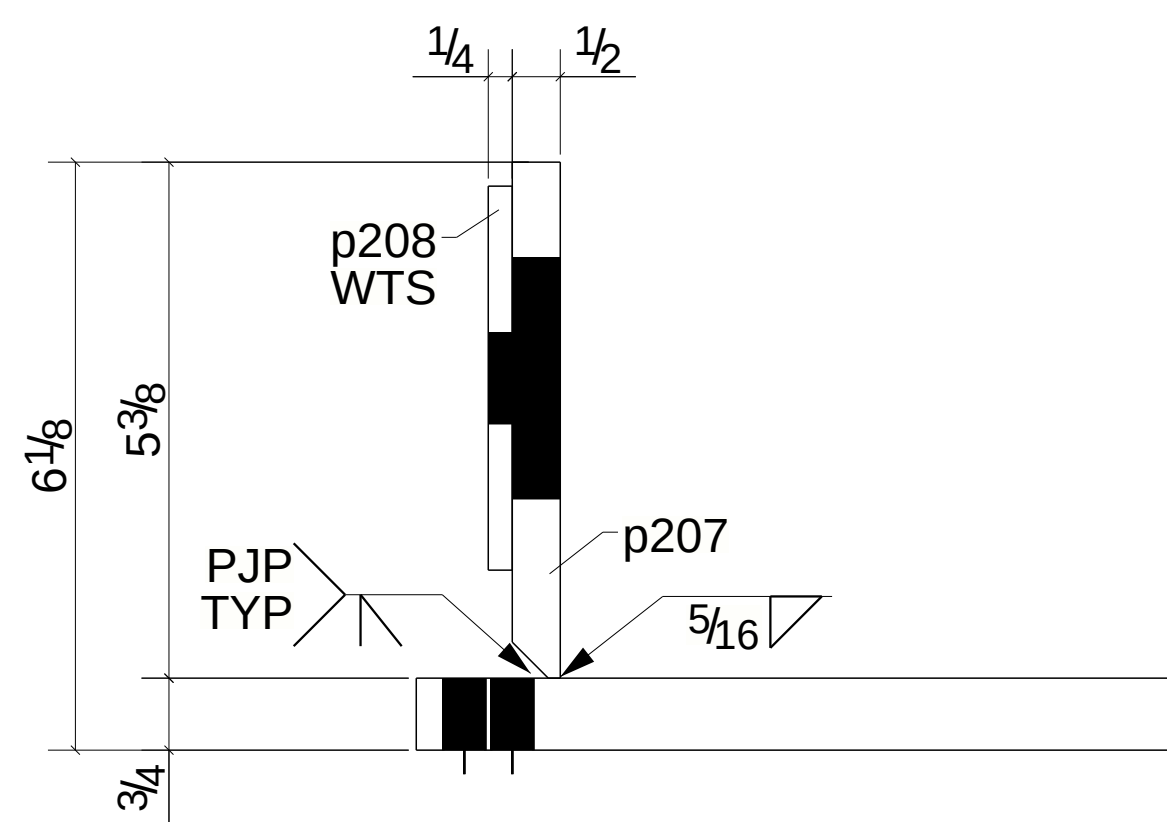

ONE - BASE PLATE - 643PL6


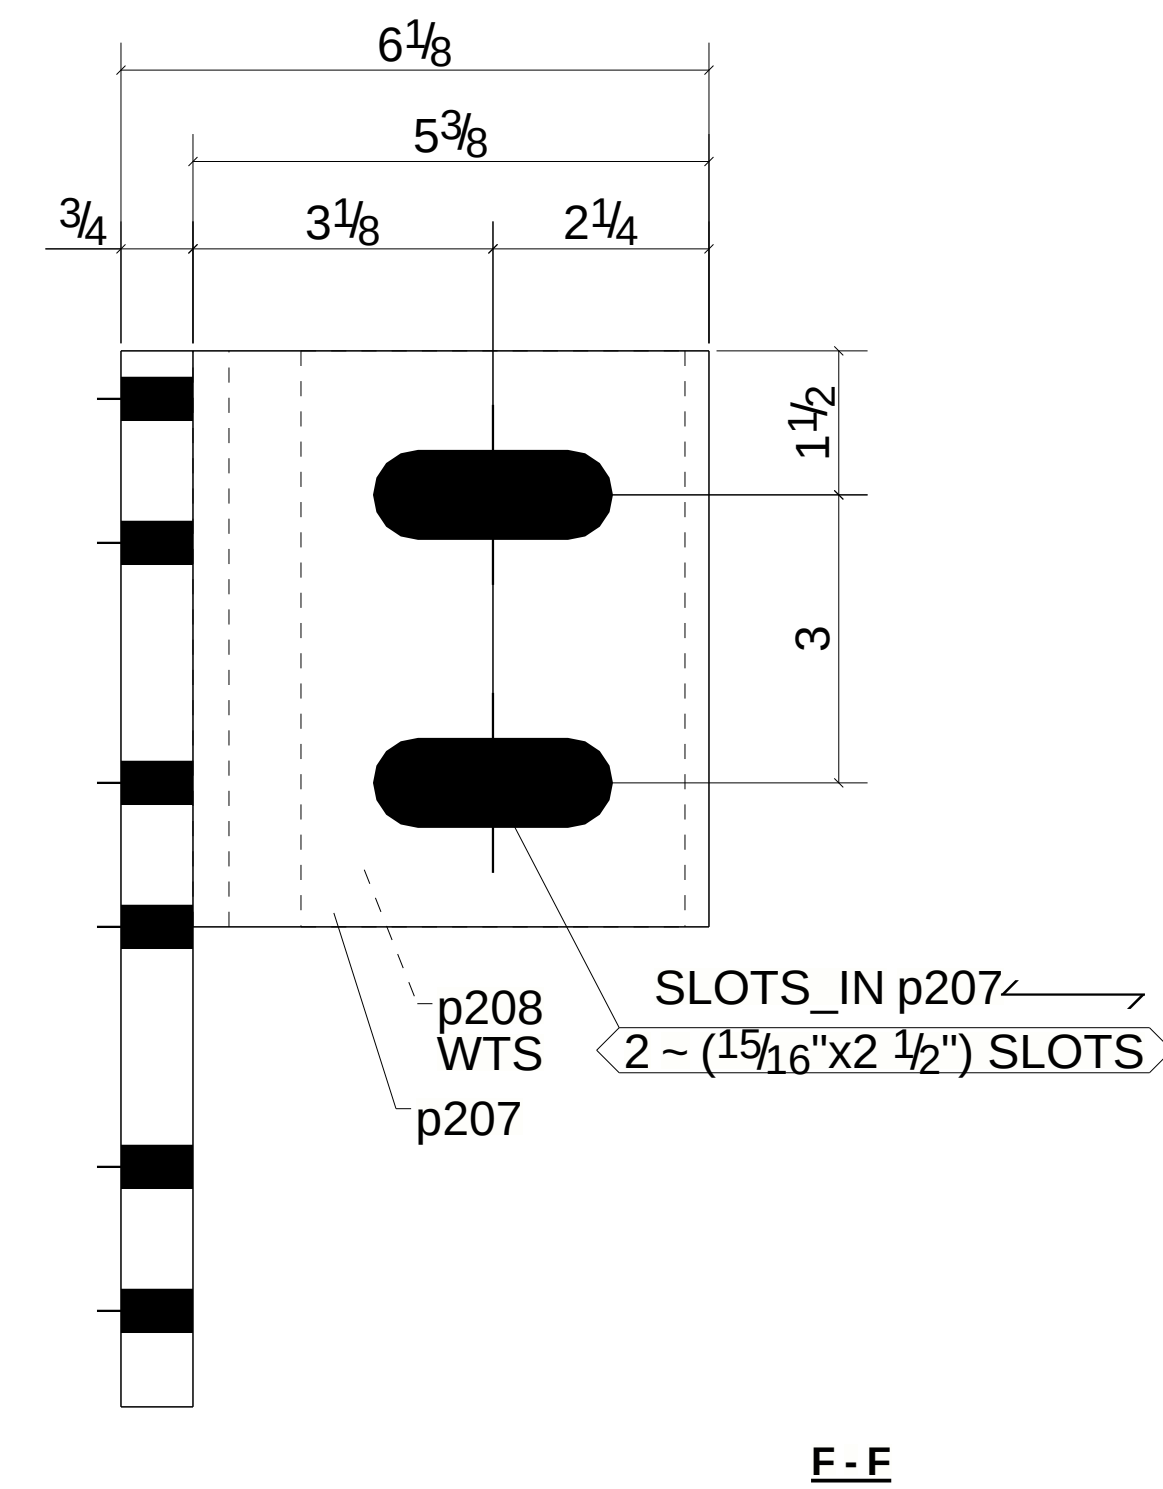


F - F

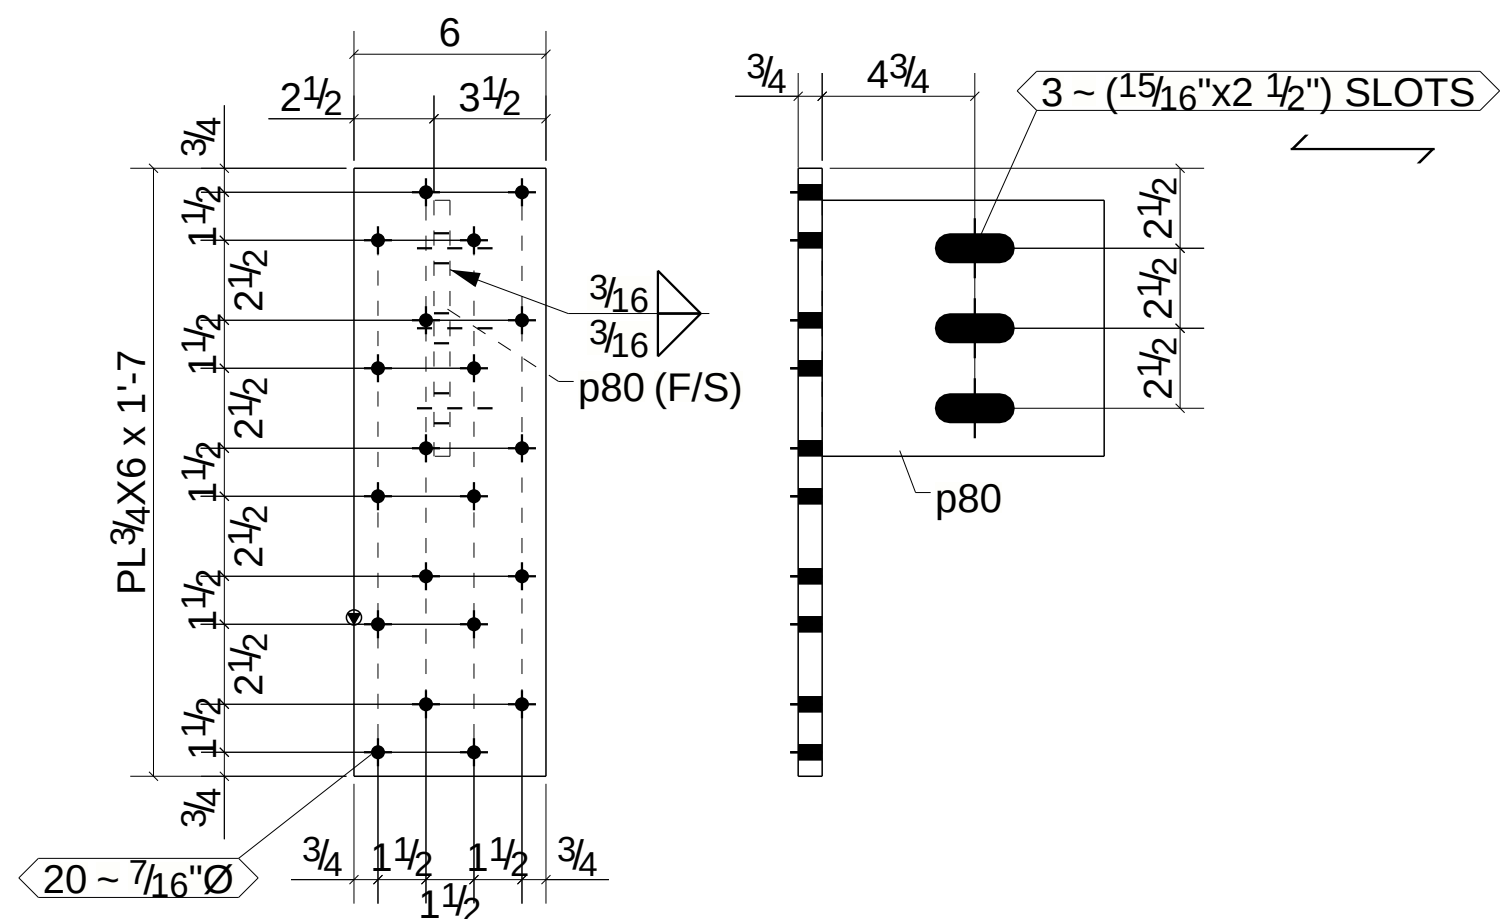

ONE - END PLATE - 643PL4

BILL OF MATERIAL					
MARK	QTY	DESCRIPTION	LENGTH	WEIGHT	REMARKS
643PL1	1	END_PLATE			SQ-2
643PL1	1	PL3/4"x6"	1'-7"	24	SHOP_PRIMER A572-GR.50
669	1	PL1/2"x6"	0'-6"	5	A572-GR.50
643PL2	1	END_PLATE			SQ-2
643PL2	1	PL3/4"x6"	1'-7"	24	SHOP_PRIMER A572-GR.50
669	1	PL1/2"x6"	0'-6"	5	A572-GR.50
643PL3	2	END_PLATES			SQ-2
643PL3	2	PL3/4"x6"	1'-7"	48	SHOP_PRIMER A572-GR.50
777	2	PL1/2"x5 7/8"	0'-6 1/2"	11	A572-GR.50
643PL4	1	END_PLATE			SQ-2
643PL4	1	PL3/4"x6"	1'-7"	24	SHOP_PRIMER A572-GR.50
880	1	PL1/2"x8"	0'-8 13/16"	10	A572-GR.50
643PL6	1	BASE_PLATE			SQ-2
643PL6	1	PL3/4"x8"	0'-11"	19	SHOP_PRIMER A572-GR.50
9207	1	PL1/2"x5 3/8"	0'-6"	4	A572-GR.50
9208	1	PL1/4"x4"	0'-6"	2	A572-GR.50
		TOTAL WEIGHT THIS DRAWING		177	

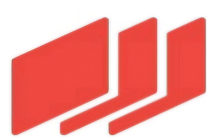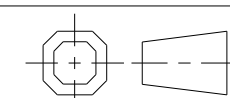[illegible]

Miguel Hidalgo,
Mexico City

CUSTOMER INFORMATION

1523 HARRISON ST.

1523 HARRISON ST., OAKLAND, CA 94612

DRAWING NUMBER

643

REVISION

0

REF.:		DOC. OWNER:		
PROJECT NO. 5220	PART/MATERIAL NO. PLATE	SCALE 1:12	SIZE D	SHEET 1 OF 1

Tekla Structures
